



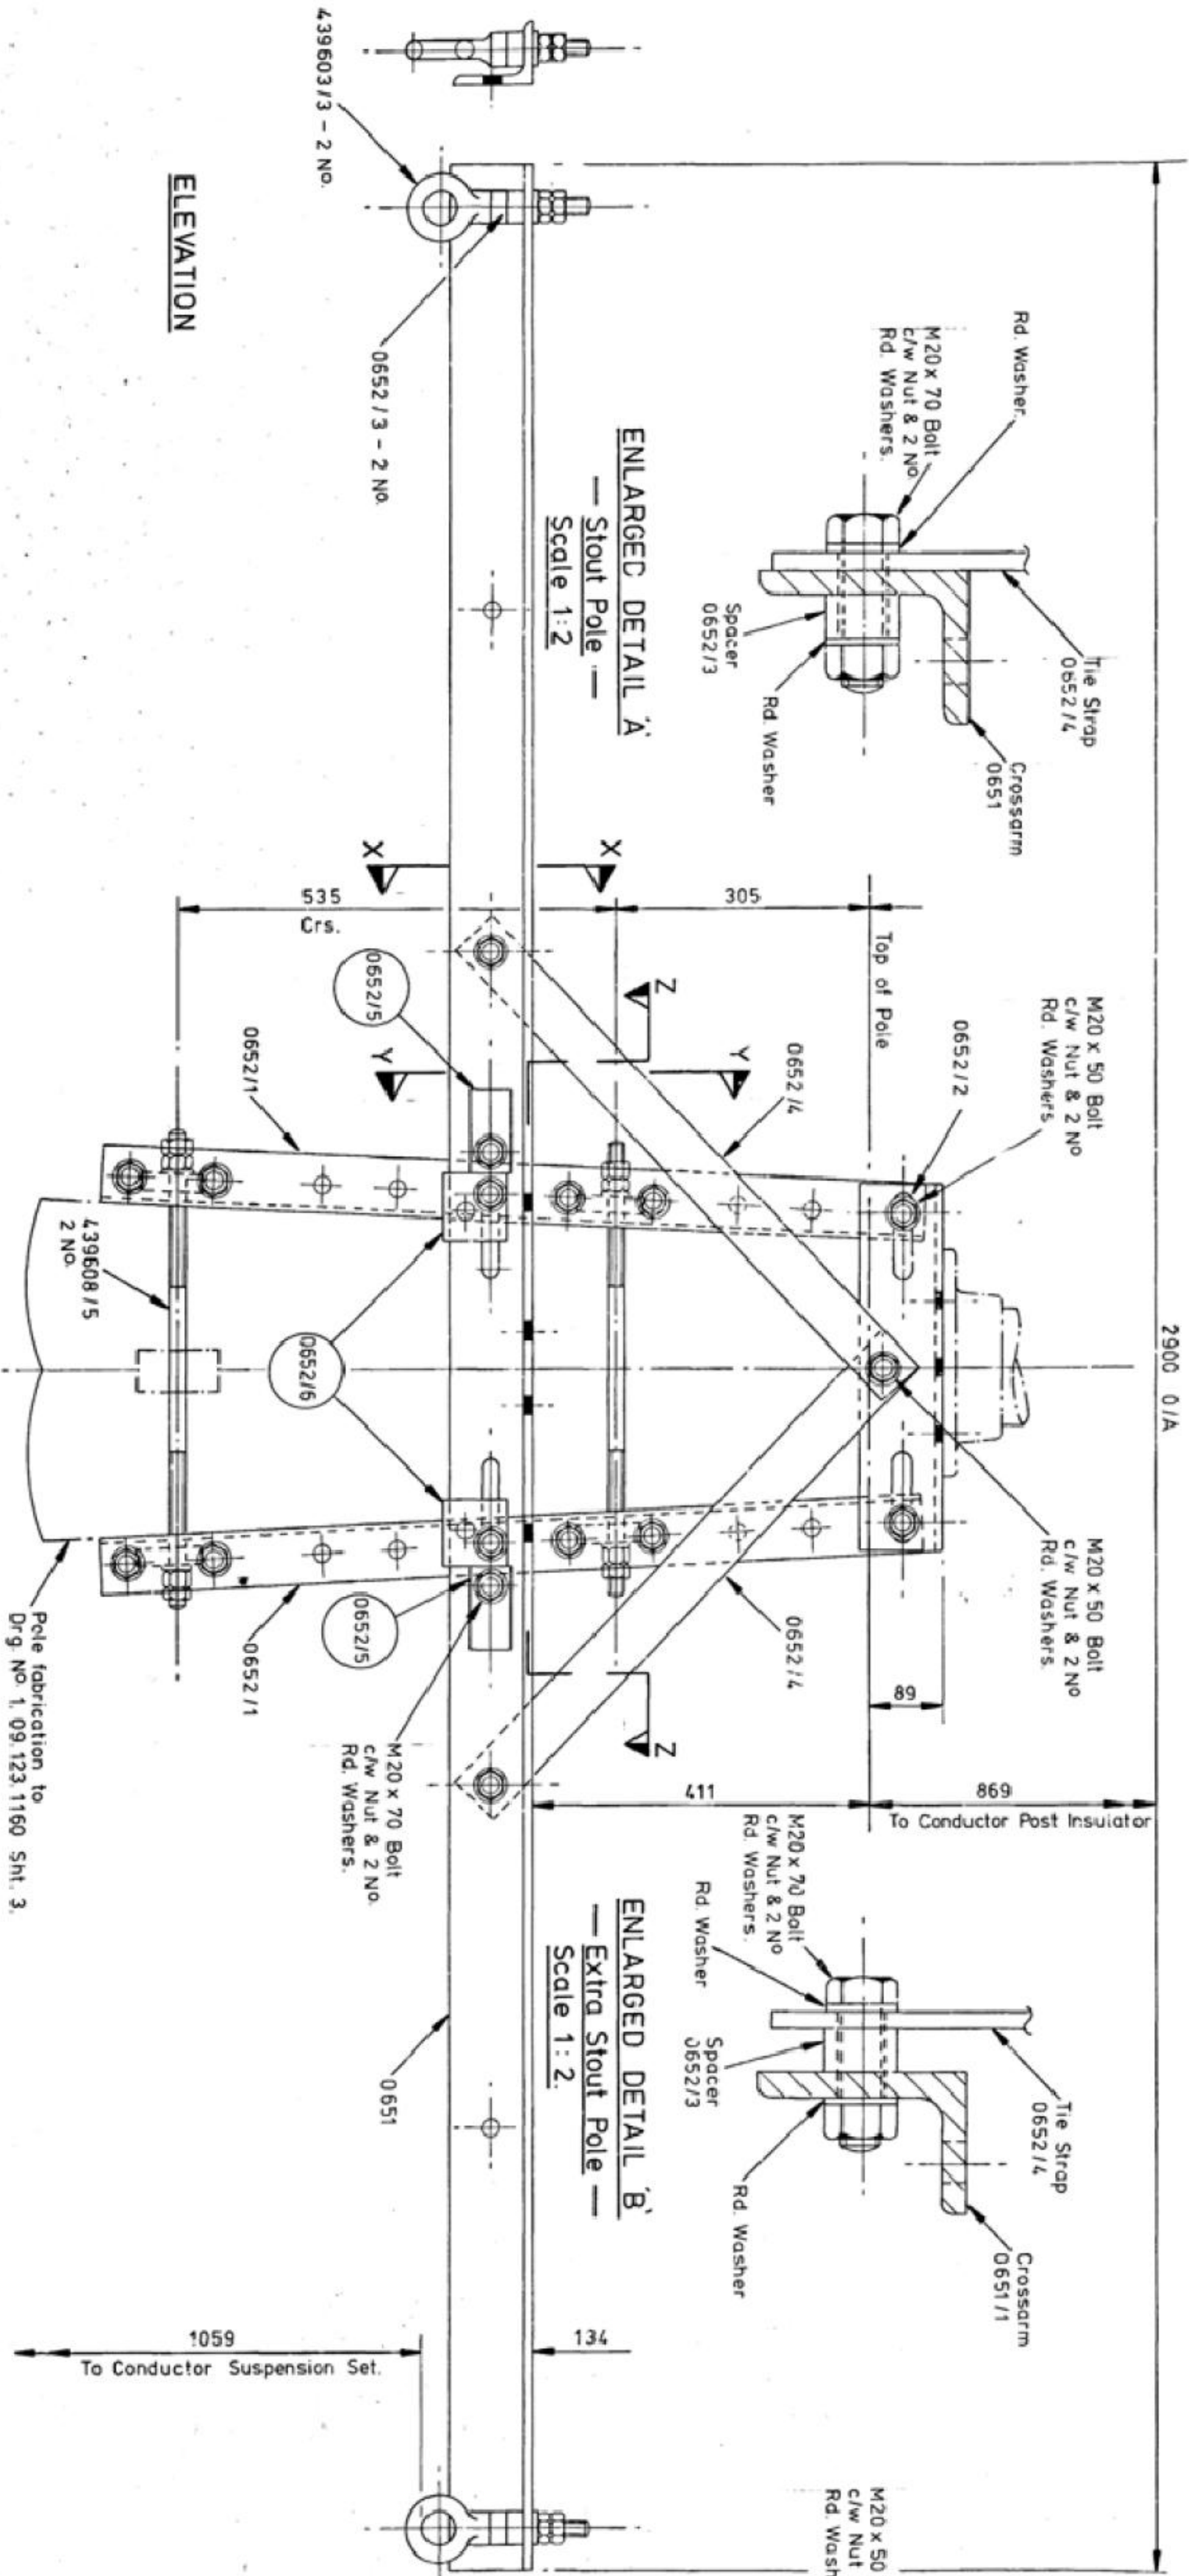


ELEVATION

SECTIONAL PLAN ON Z-Z
— Extra Stout Pole —

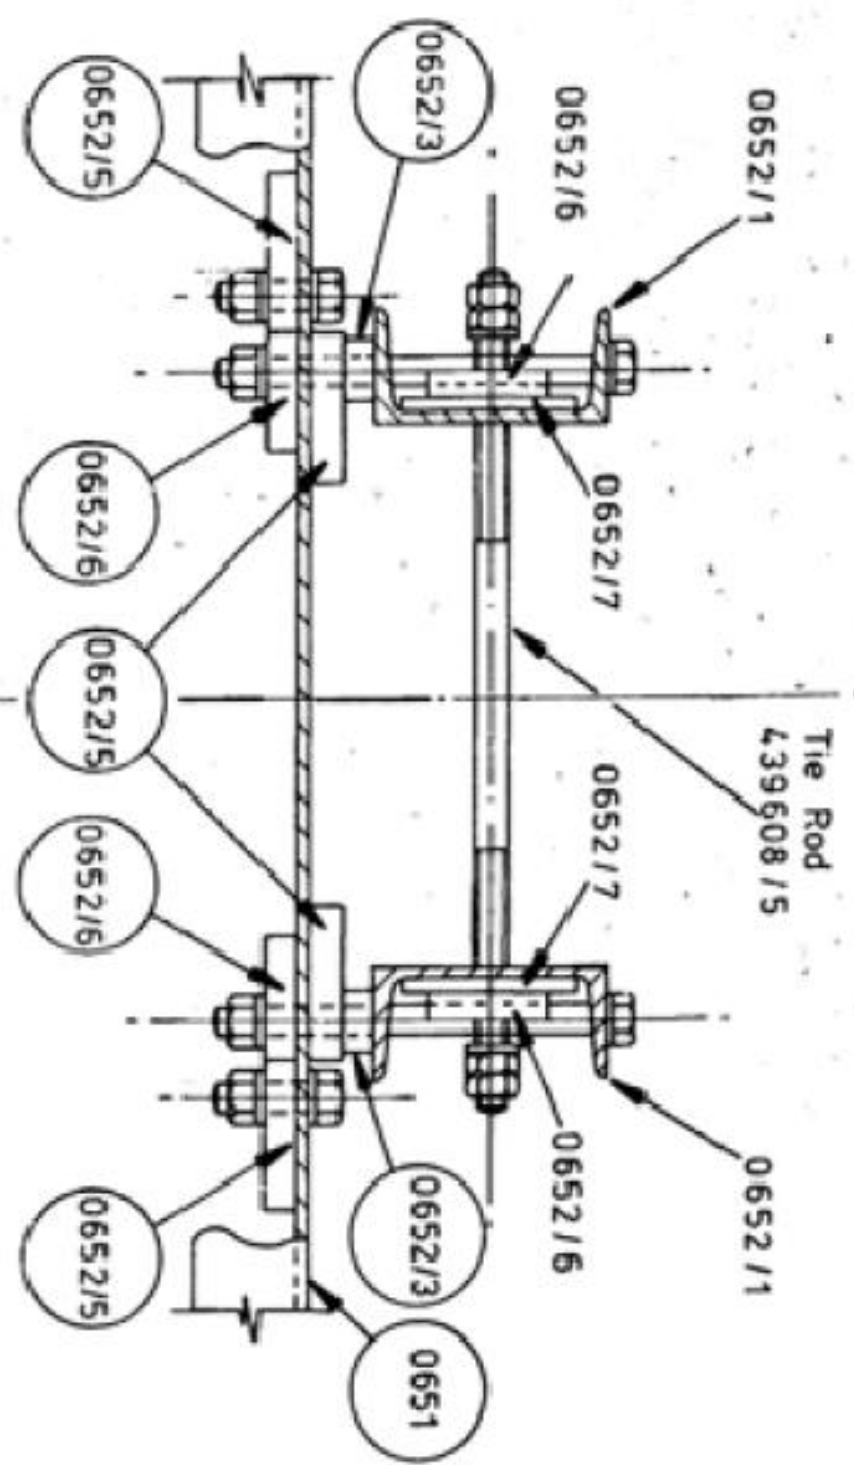


SECTIONAL PLAN ON Z-Z
— Stout Pole —

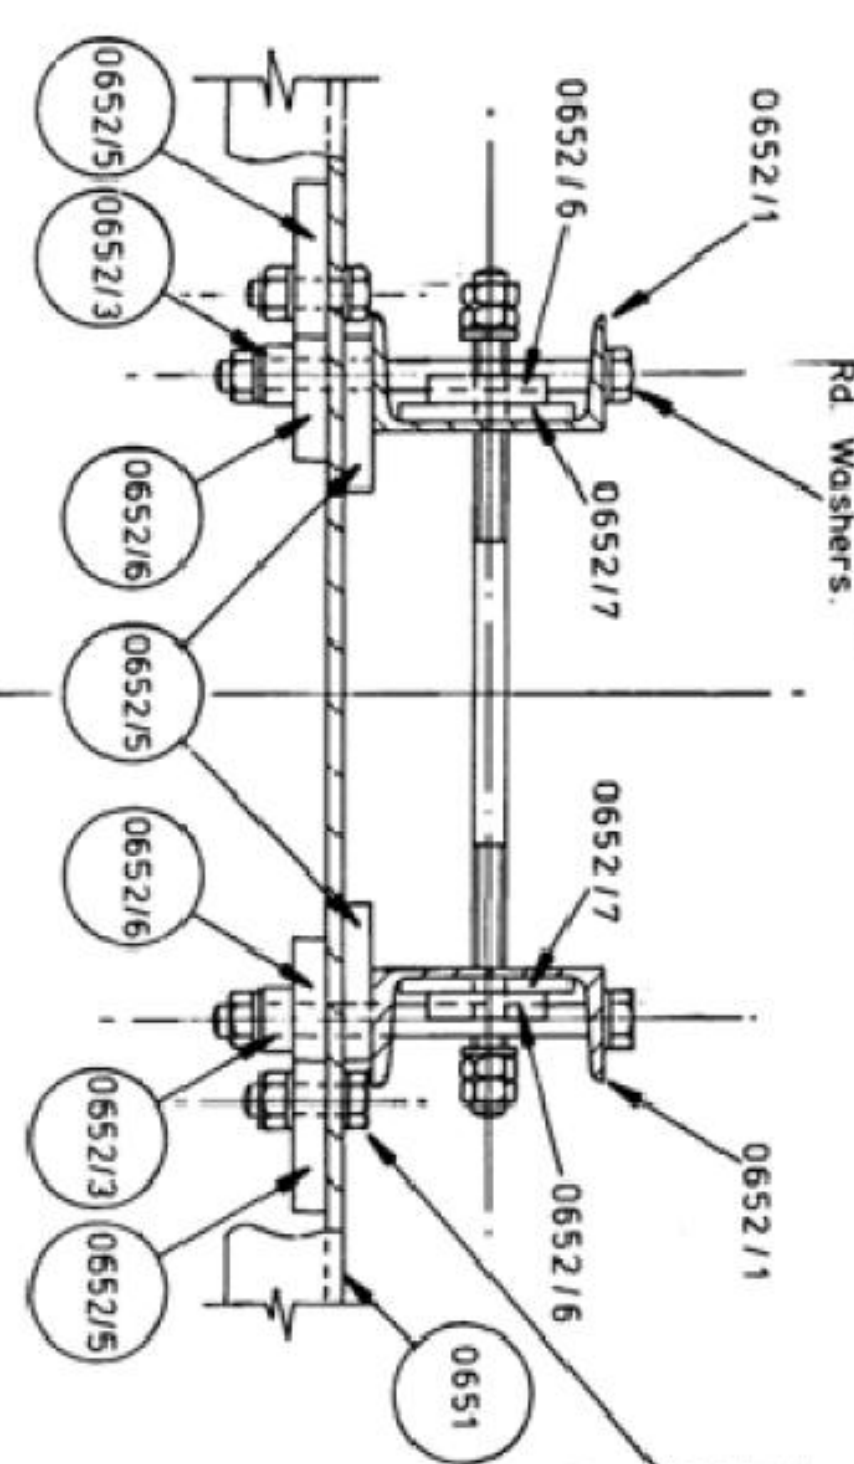


NOTES
Components which MUST be located precisely to cater for variation in Pole sizes shown

To be read in conjunction with Drg. No 1.09.123.1190 Sht. 2.

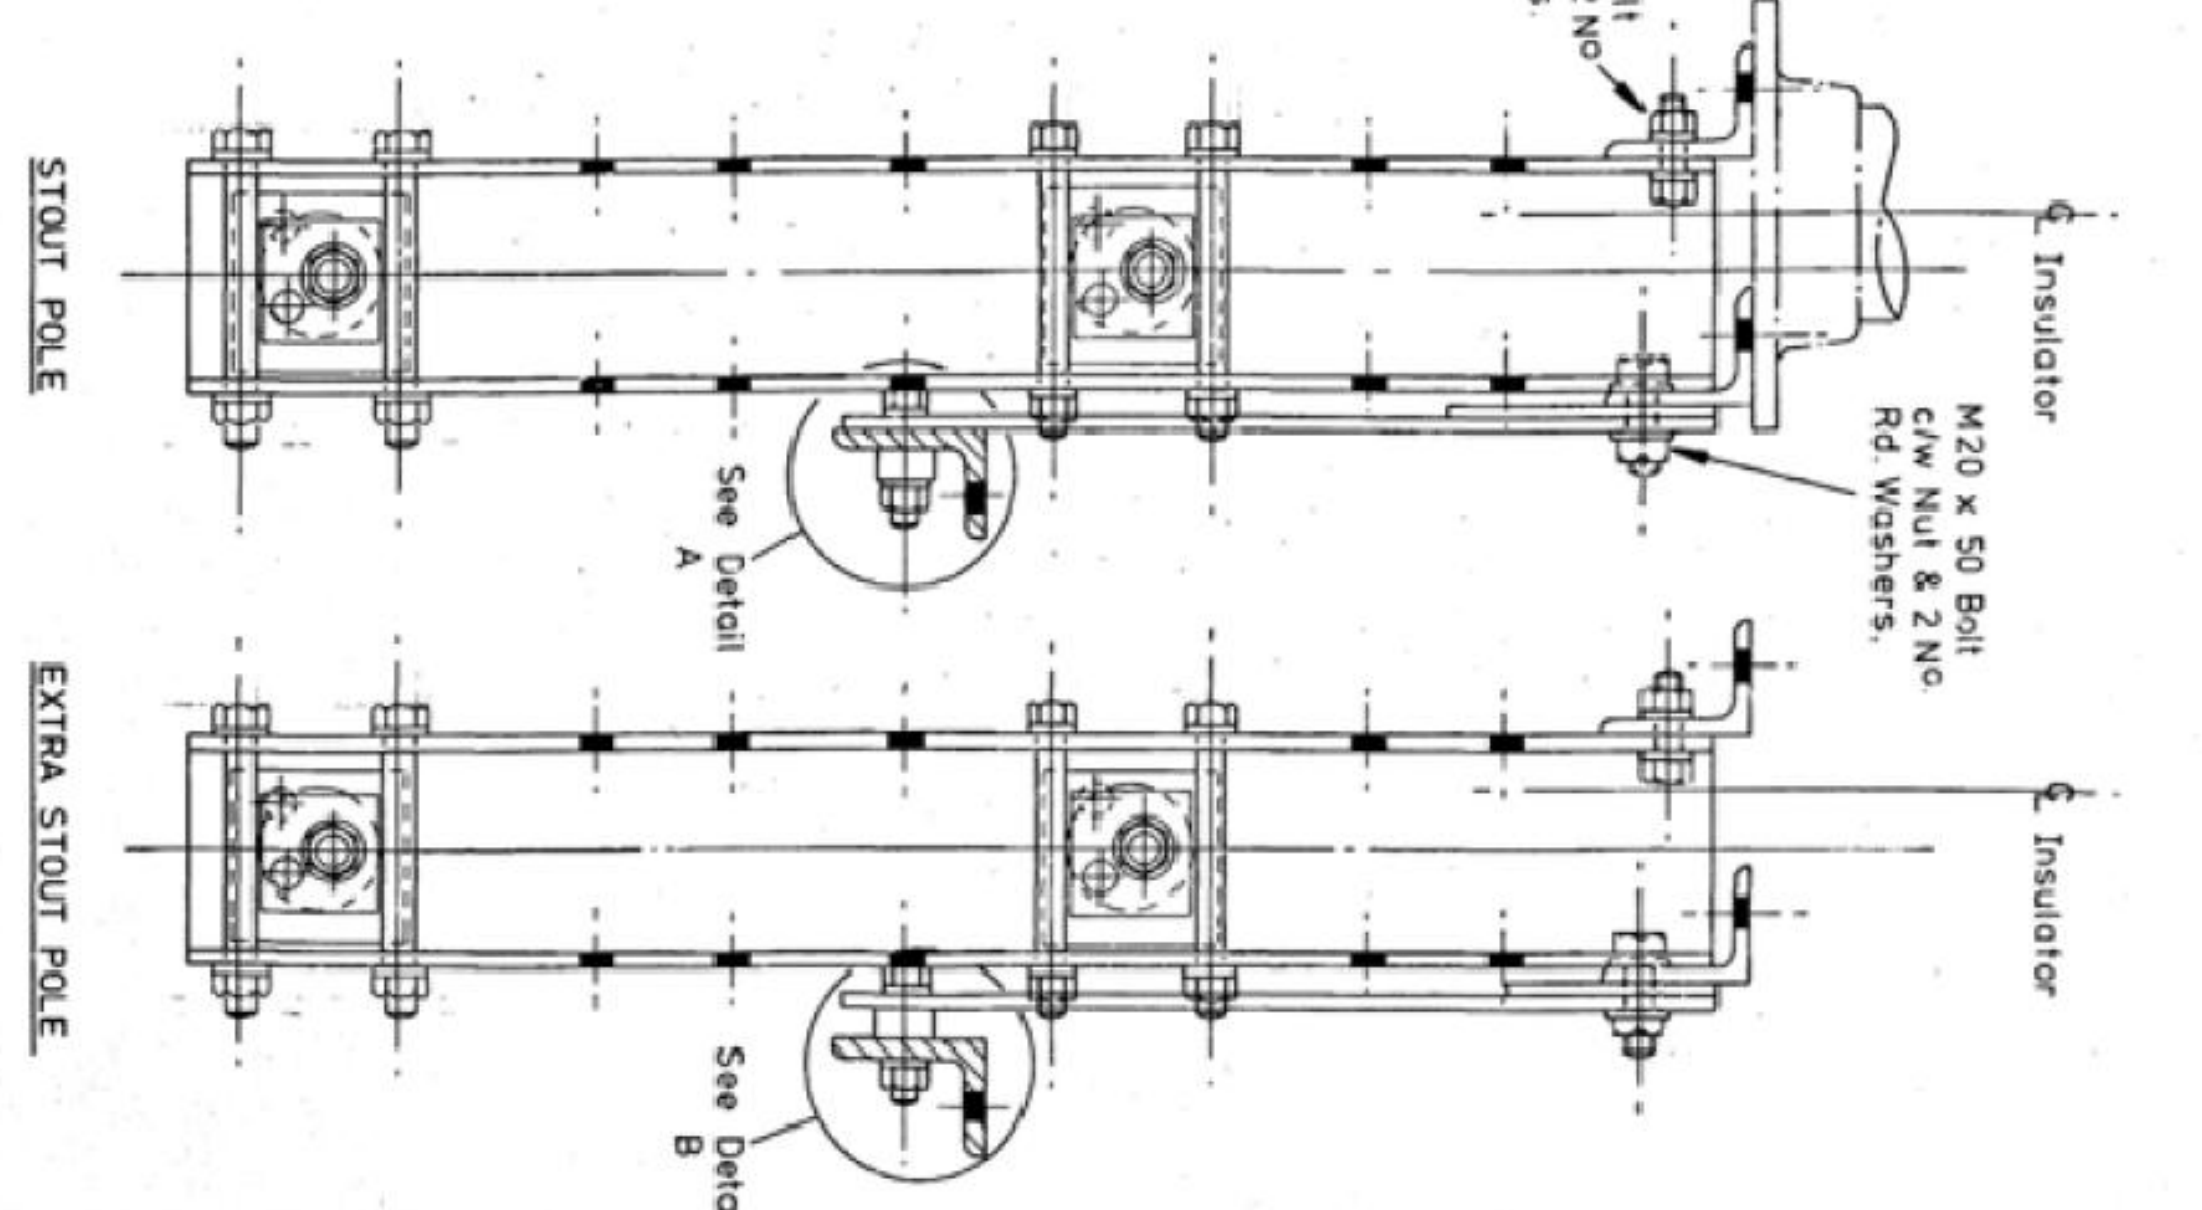

SECTION X-X —

SECTION Y-Y —

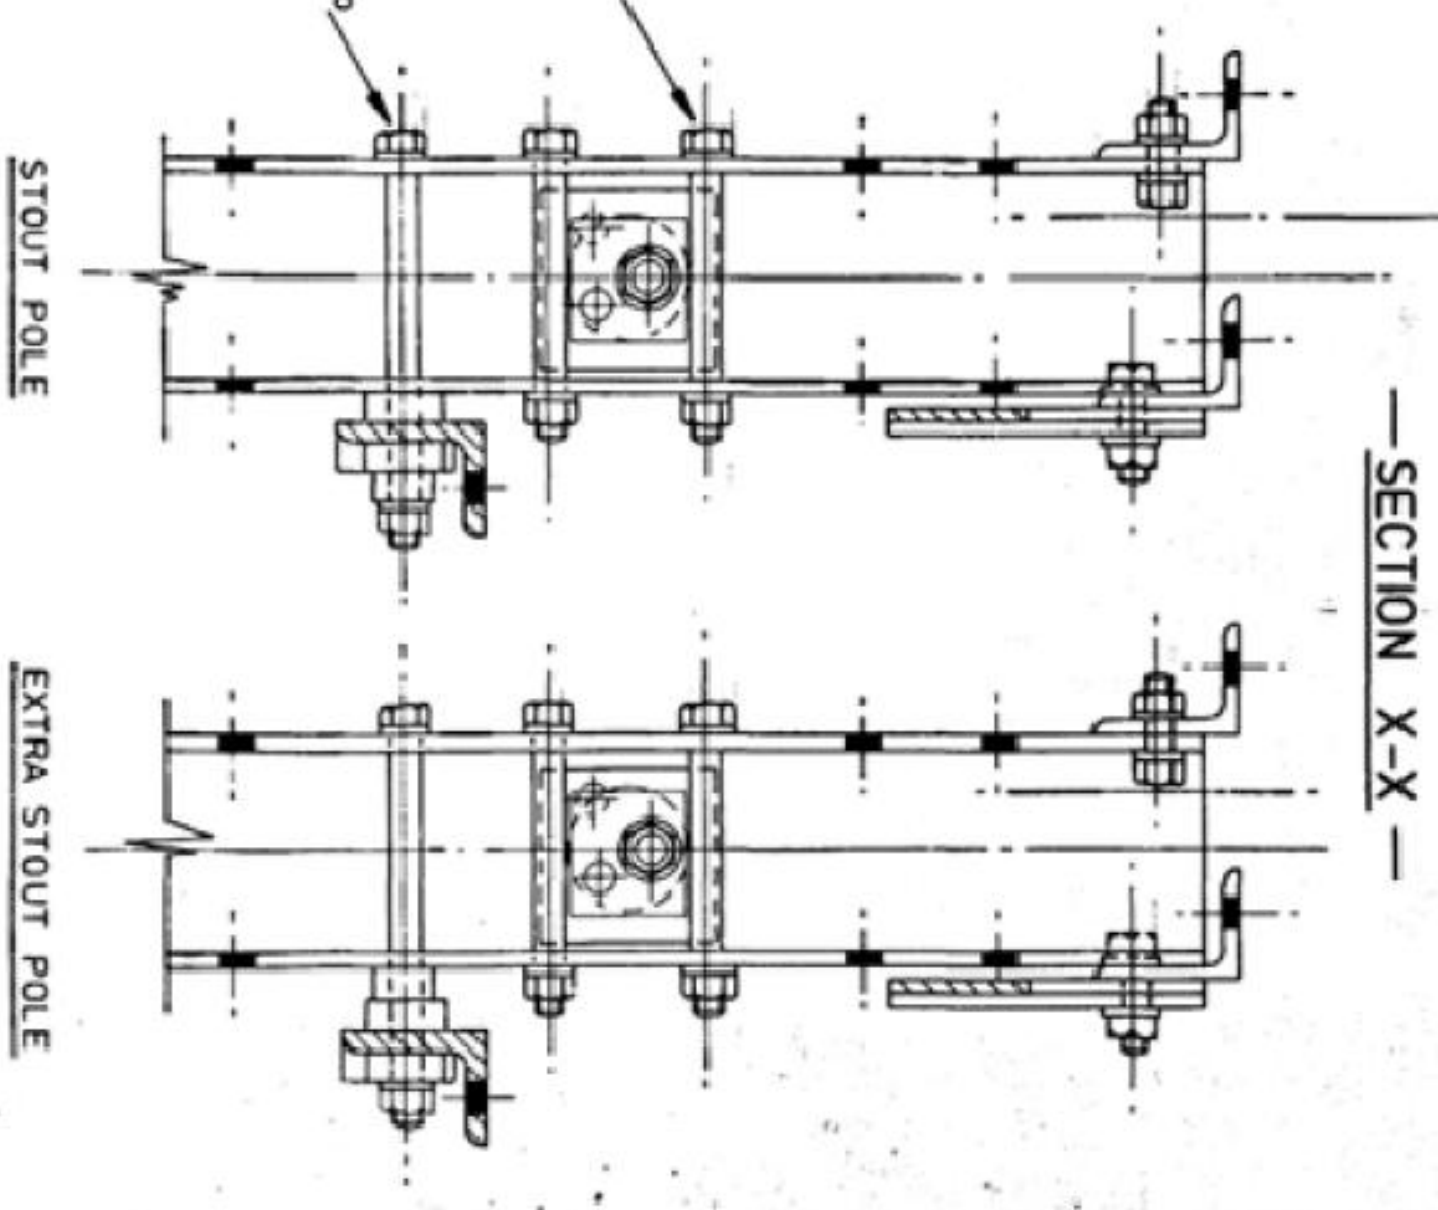

ALL DIMENSIONS ARE IN MILLIMETRES UNLESS OTHERWISE STATED

CE Electric UK				Lloyds Court, 78 Grey Street, Newcastle Upon Tyne, NE1 6AF			
Manufacture Details				66KV SINGLE CIRCUIT LINES			
ASSEMBLY OF COMPONENTS FOR 'A' POLE				LIGHT DUTY STRAIGHT LINE APPLICATION			
Sheet No.	4	Scale	1:5	Type	OVERHEAD	Historic Drg. No.	1091010652
Drawn By				Checked By			
Reviewed				Checked By			
Date Issued				Checked By			
Revision				Checked By			