


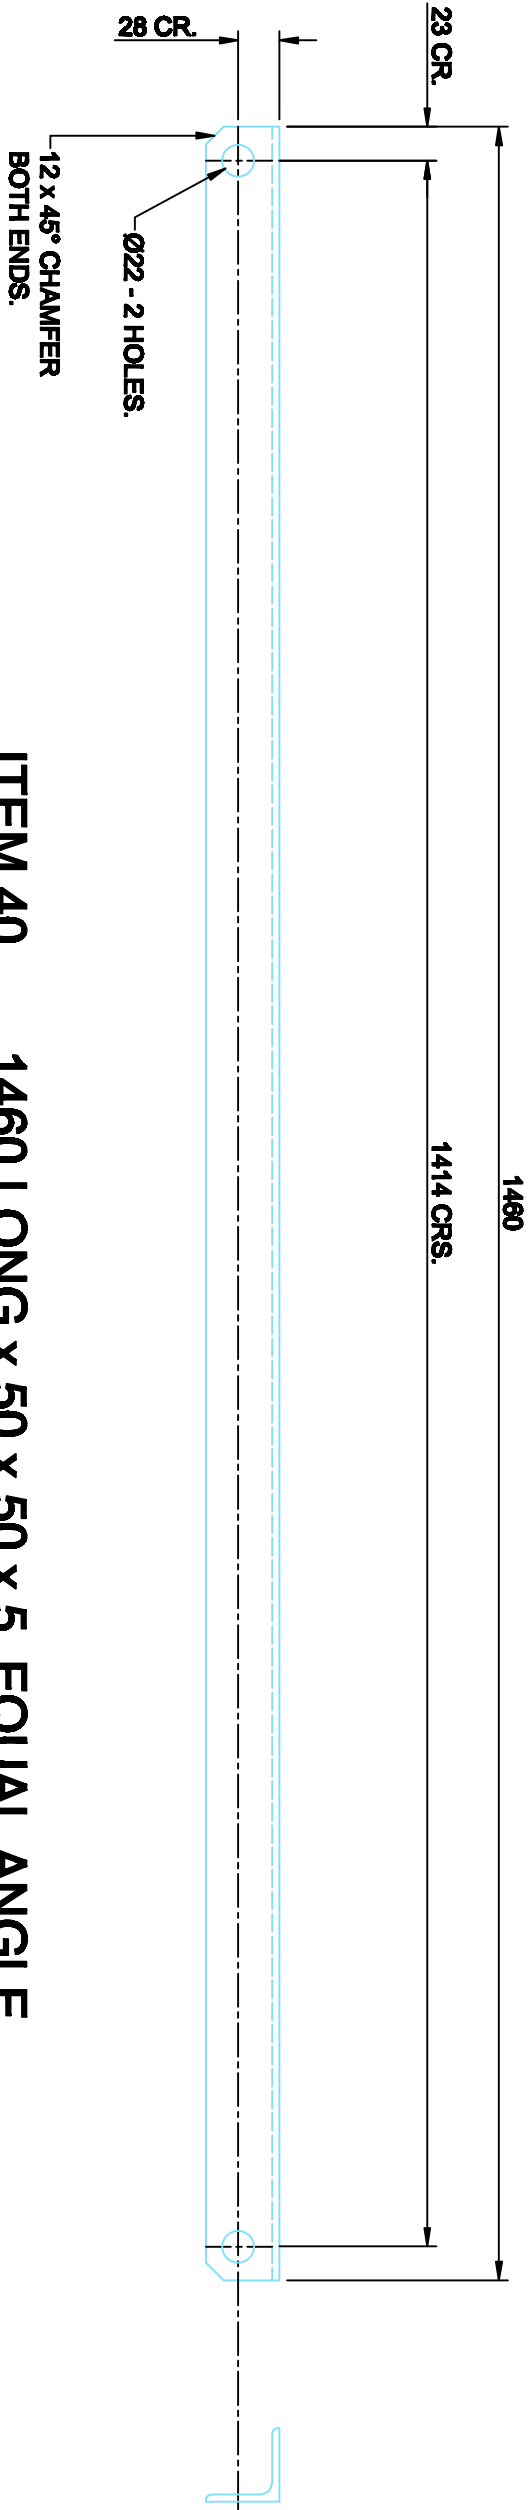

ITEM 40. 1460 LONG x 50 x 50 x 5 EQUAL ANGLE

- NOTES:-
- 1. STEELWORK TO B.S. 4360, GRADE 43A & B.S. 449
 - 2. SECTIONS TO B.S. 4, PART 1, FLATS TO B.S. 6722
 - 3. ALL BURRS TO BE REMOVED.
 - 4. GALVANIZING TO ISO 1461 AFTER FABRICATION.

CE Electric UK Lloyds Court, 78 Grey Street, Newcastle Upon Tyne, NE1 6AF			132KV OVERHEAD LINES CROSSARM STRUT ITEM NO.40		
Manufacturer Details					
Street No.	40	Scale	1:5		
Prepared By Barbara Simpson			Type OVERHEAD	DOCUMENT SUB CLASS	
Revised 19/06/07	Grid Reference		Ref No. C949350	Historic Dwg.No.	1091010675
Date Issued 19/06/07	Checked By G HAMMEL		Revision Notes		