
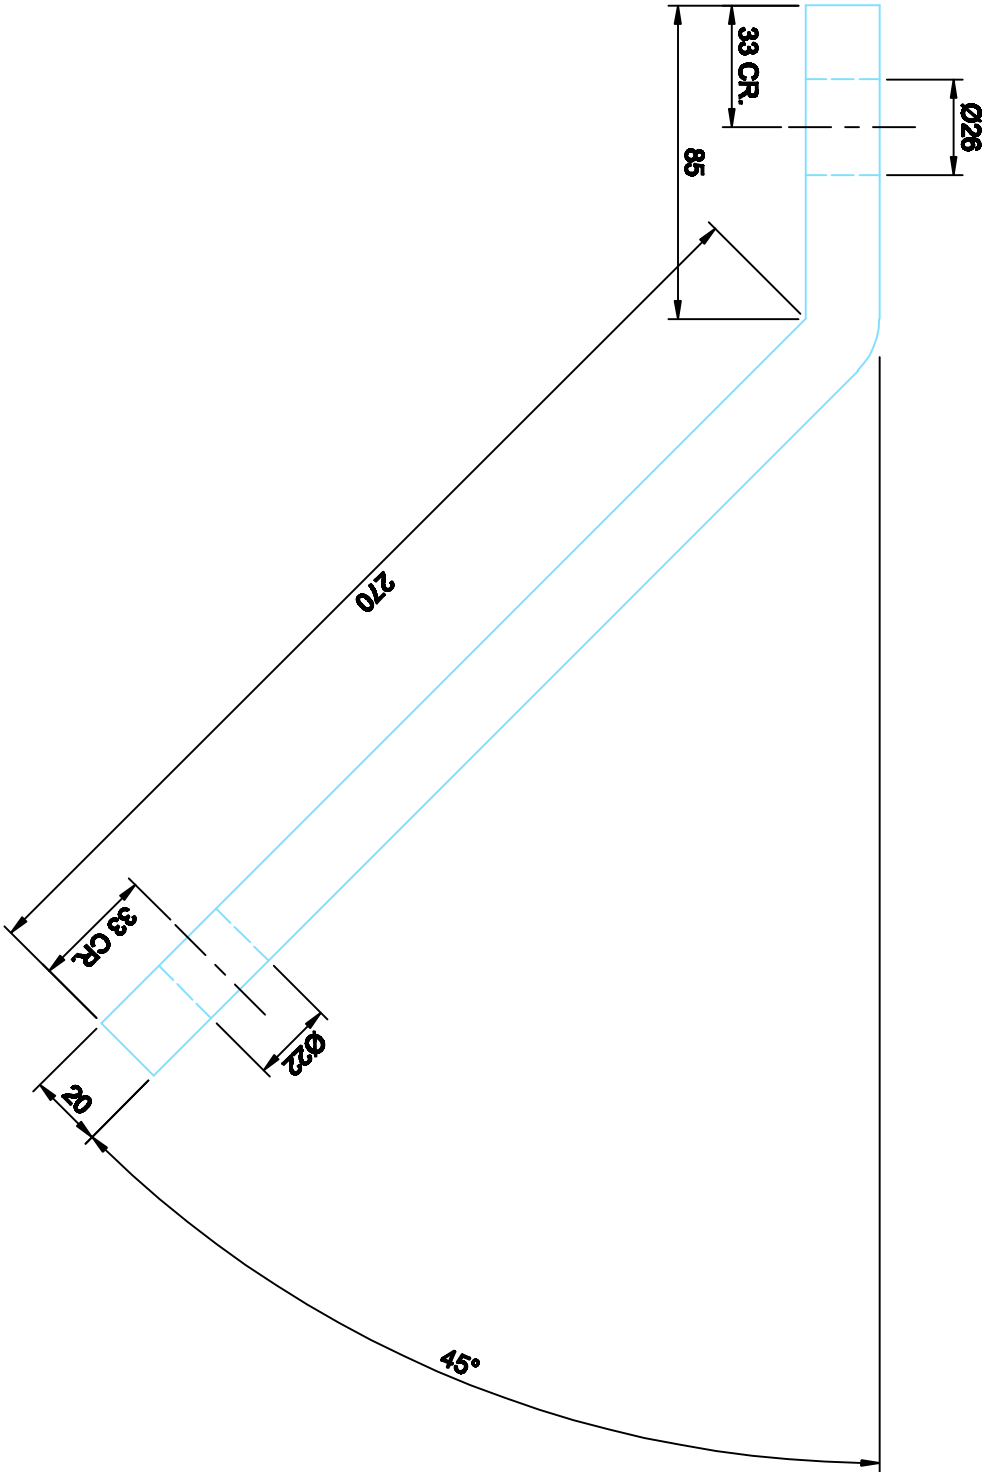


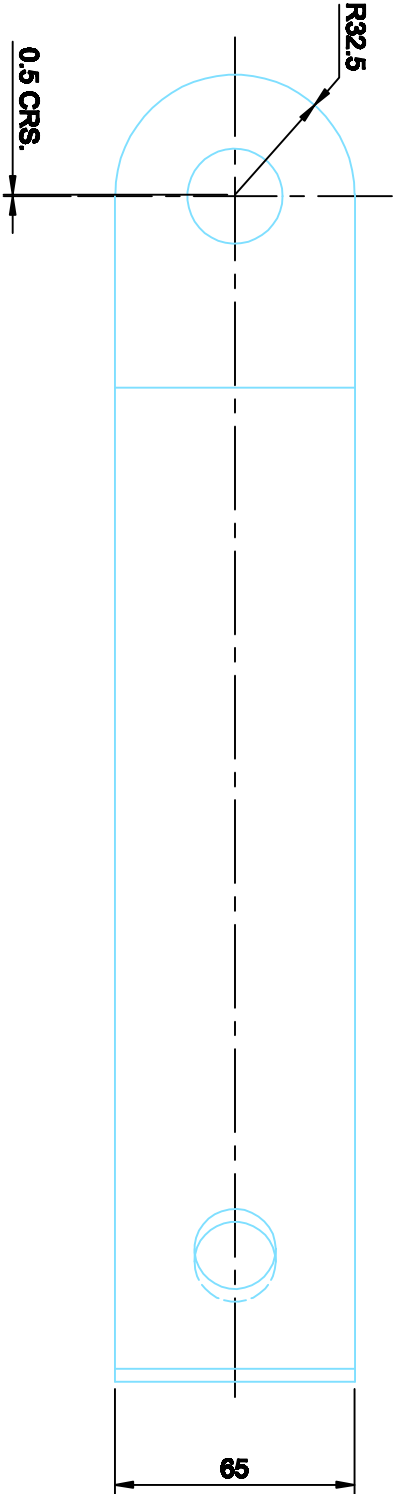

MATERIAL:- 355 APPROX. DEVELOPED LENGTH X 65 X 20THK. BAR M.S.

- NOTES:-
- 1. STEELWORK TO B.S. 4360, GRADE 43A & B.S. 449
 - 2. SECTIONS TO B.S. 4, PART 1, FLATS TO B.S. 6722
 - 3. ALL BURRS TO BE REMOVED.
 - 4. GALVANIZING TO ISO 1461 AFTER FABRICATION.

CE Electric UK Lloyds Court, 78 Grey Street, Newcastle Upon Tyne, NE1 6AF			132KV OVERHEAD LINES		
Manufacturer Details			45 DEGREES CRANKED STAY STRAP		
Sheet No.	47	Scale	1:2		
Prepared By Barbara Simpson			Type	OVERHEAD	
Reviewed 03/07/07	Grid Reference		Ref No.	C949708	Historic Dwg.No.
Date Issued 02/07/07	Checked By G HAMMEL		Revision	Notes	
				DOCUMENT SUB CLASS	
				1091010675	