
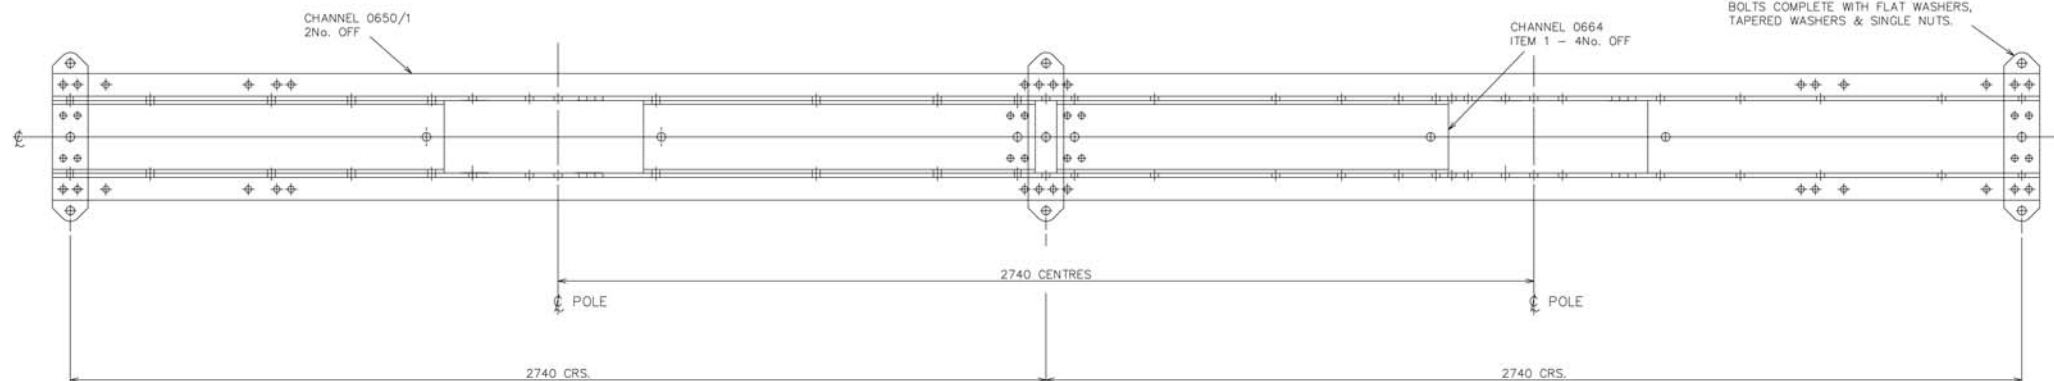


⊕ DENOTES 18 DIA. HOLES
 ⊕ DENOTES 22 DIA. HOLES
 ⊕ DENOTES 24 DIA. HOLES

ELEVATION

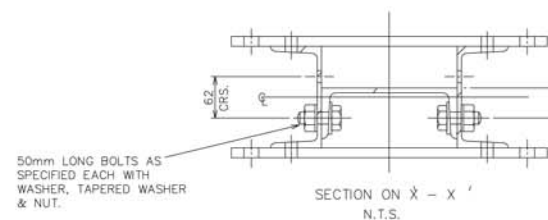

PLATES TOP & BOTTOM 0650/2
 6 No. OFF AFFIXED WITH M16x50.
 BOLTS COMPLETE WITH FLAT WASHERS,
 TAPERED WASHERS & SINGLE NUTS.

PLAN

NOTES :-

1. OUTER STIFFENER CHANNELS 0664/1 EACH AFFIXED WITH 8No. M20 x 50 LONG BOLTS & 2No. M16 x 50 LONG BOLTS.
2. INNER STIFFENER CHANNELS 0664/1 EACH AFFIXED WITH 6No. M20 x 50 LONG BOLTS & 2No. M16 x 50 LONG BOLTS.

TO BE READ IN CONJUNCTION WITH SHEET 1
 OF THIS DRAWING.

ALL DIMENSIONS SHOWN ARE IN MILLIMETRES UNLESS OTHERWISE STATED

		Northern Electric Distribution Limited, Coriol House, Newcastle Upon Tyne, NE1 6NE.	
66kV OVERHEAD LINES STRAIGHT LINE SECTION 'H' SUPPORT CROSSARM ASSEMBLY			
Prepared by S.B. Checked M.W. Date Issued FEB'97	Drg No. 1 09 123 1163 Mods. 1/1	Sheet No. 4 Revised SEP'99(RC) Scale 1:7.5	