



THE ASSEMBLED PLAN

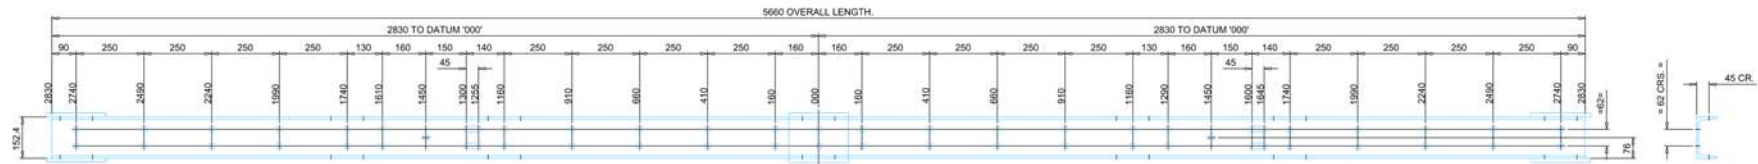

ELEVATION VIEW

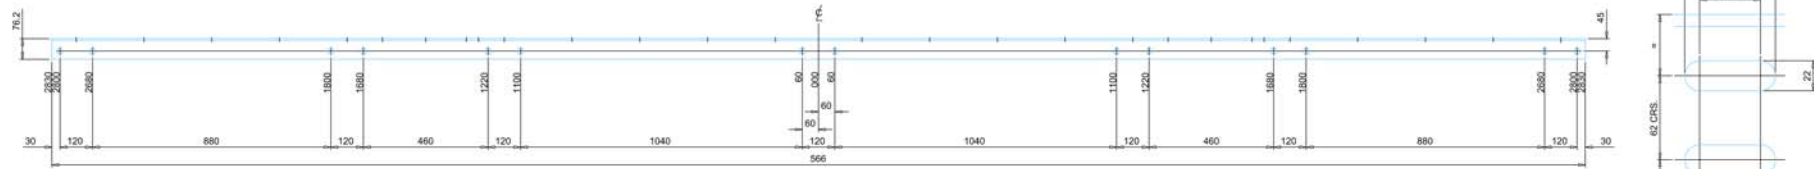

PLAN

SLOT DETAILS
SCALE 1:2

NOTE 1
INNER AND OUTER STIFFENER CHANNELS 0675 SHT50 ITEM 6
EACH FIXED WITH 10 OFF M20x50 LONG BOLTS.
TO BE READ IN CONJUNCTION WITH SHT4.

		Lloyds Court, 78 Grey Street, Newcastle Upon Tyne, NE1 6AF	
Sheet No: 7		Scale: 1:10	
Prepared By: Joan Oakley		Type: OVERHEAD	
Revised: 04/06/10		Gnd Reference:	
Date Issued: 04/06/10		Checked By: G HAMMILL	
Ref No: C987619		Historic Drg No: 1091231163	
Revision:		Notes:	