



- ⊕ DENOTES 18 DIA. HOLES.
- ⊕ DENOTES 24 DIA. HOLES.
- ⊕ DENOTES 22 DIA. HOLES.

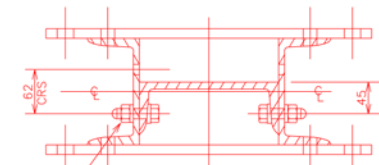

50mm LONG BOLTS AS
SPECIFIED EACH WITH
WASHER, TAPERED
WASHER & NUT.

SECTION X - X

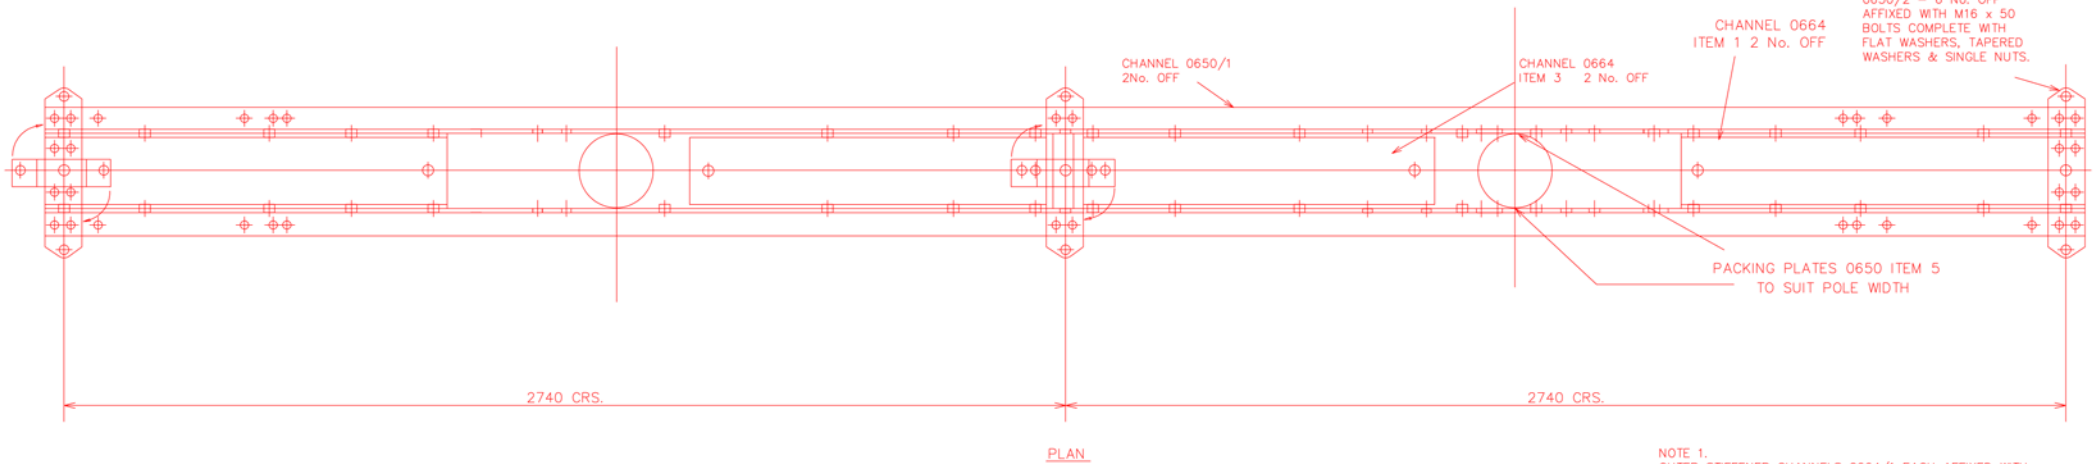

NOTE 1.
OUTER STIFFENER CHANNELS 0664/1 EACH AFFIXED WITH
8 No. M20 x 50 LONG BOLTS & 2 No. M16 x 50 LONG BOLTS.

NOTE 2.
INNER STIFFNER CHANNELS 0664/3 EACH AFFIXED WITH
6 No. M20 X 50 LONG BOLTS & 2 No. M16 X 50 LONG BOLTS.

TO BE READ IN CONJUNCTION WITH SHEETS
1 & 2 OF THIS DRAWING AS REQUIRED.

NORTHERN ELECTRIC		Northern Electric, Coriol House, Newcastle upon Tyne NE1 6NE			
Drawn C.M.		66KV OVERHEAD LINES - LARGE SECTION H POLES CROSSARM ASSEMBLY FOR 8' - 0" 2440 CENTRES			
Checked M.W.		Orig.No.	1 09 123 1164	Sheet No.	3
Date Issued 7.6.96		Revised		Scale	1:7.5
Mod.					