



⊙ DENOTES 22 DIA. HOLES

ELEVATION

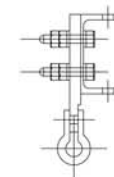

SECTION X-X  
SCALE 1:5

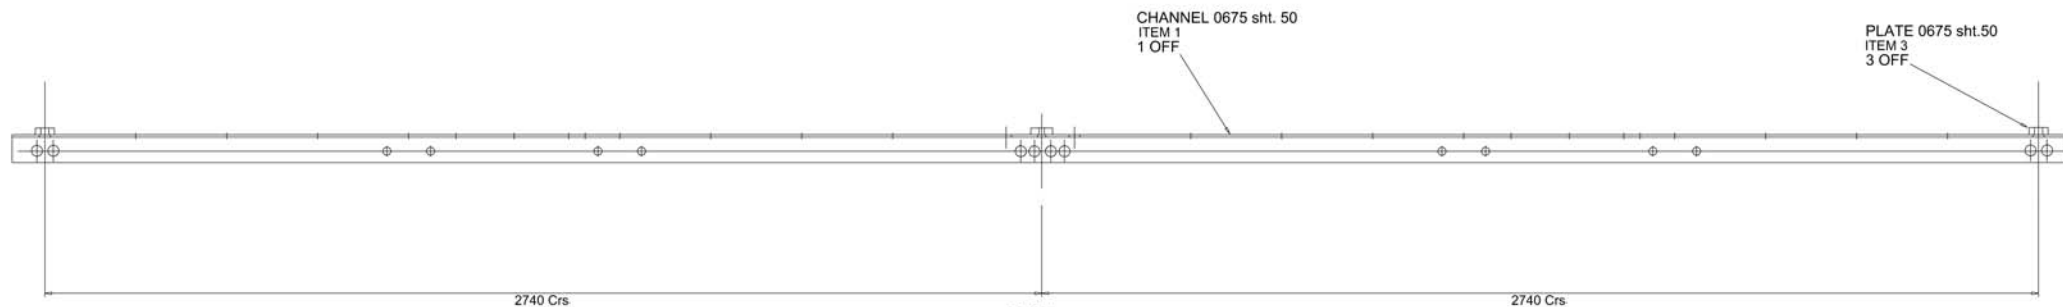

CHANNEL 0675 sht. 50  
ITEM 1  
1 OFF

PLATE 0675 sht.50  
ITEM 3  
3 OFF

PLAN

ALL DIMENSIONS SHOWN ARE IN MILLIMETRES UNLESS OTHERWISE STATED

|                               |                        |                                                                         |                     |
|-------------------------------|------------------------|-------------------------------------------------------------------------|---------------------|
|                               |                        | Lloyds Court, 78 Grey Street, Newcastle Upon Tyne, NE1 6AF              |                     |
| Manufacturer Details          |                        | 66KV SINGLE CIRCUIT OVERHEAD LINES<br>CROSSARM ASSEMBLY FOR PORTAL POLE |                     |
| Sheet No.<br>3                | Scale                  | Type<br>OVERHEAD                                                        | POLES               |
| Prepared By<br>Barbara Gordon | Grid Reference         | Ref No.<br>C987010                                                      | Historic<br>Dwg.No. |
| Revised<br>12/05/10           | Checked By<br>G HAMMEL | Revision                                                                | Notes               |
|                               |                        |                                                                         | 1091231165          |