


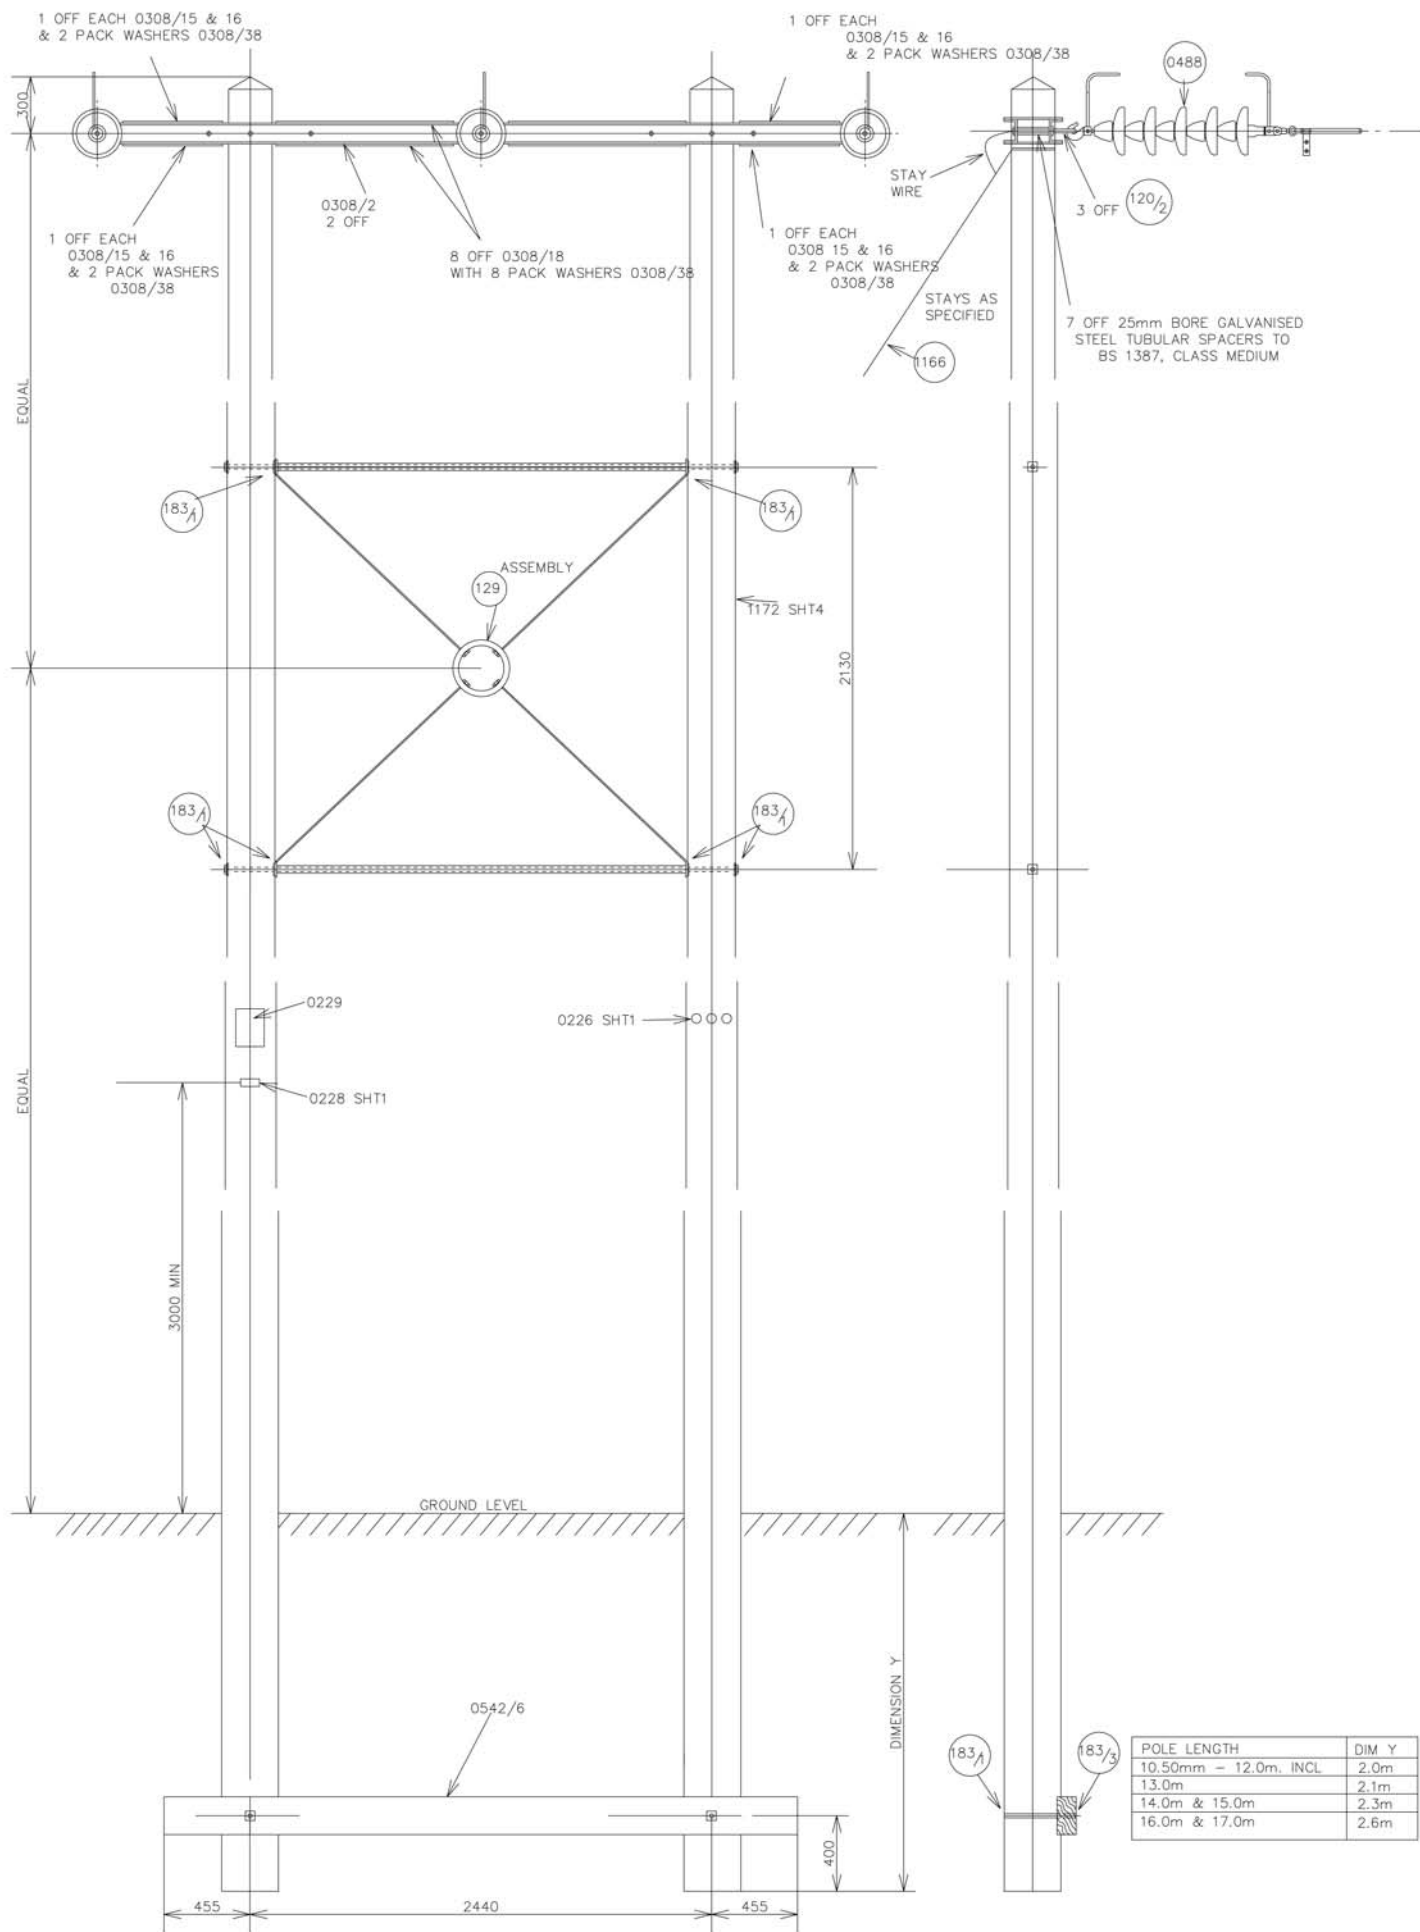

THIS DRAWING ALSO REFERRED TO IN WORK SPEC. REF. No 04/221M

NOTES

- ALL POLE BOLTS TO BE M20 DIA
- DETAIL DRAWINGS INDICATED THUS: - REFER TO DRG No 66.5/10
SERIES : ALL OTHER DETAILS REFER TO 1:09:101 SERIES

ALL DIMENSIONS SHOWN ARE IN MILLIMETRES UNLESS OTHERWISE STATED



Prepared by C.T.
Checked H.A.J. Date Issued FEB'76

Northern Electric Distribution Limited, Carliol House, Newcastle Upon Tyne, NE1 6NE.

66kV SINGLE CIRCUIT OVERHEAD LINES TERMINAL 'H' SUPPORT WITHOUT CABLE TERMINATION

Drq.No. 1 09 123 1172
Mod. A B C

Sheet No. 3
Revised SEP'99(RC)
Scale 1:20