

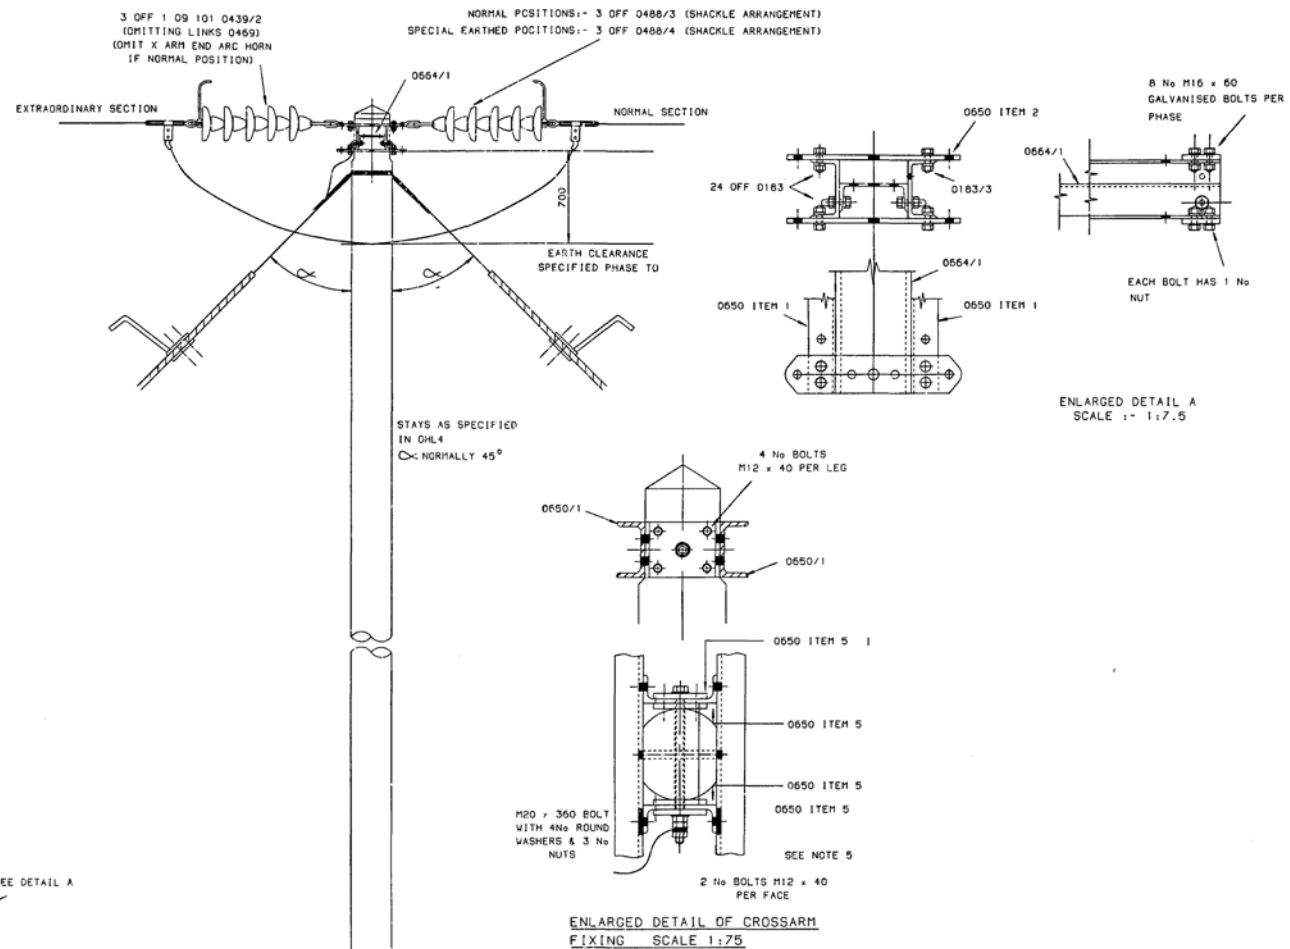


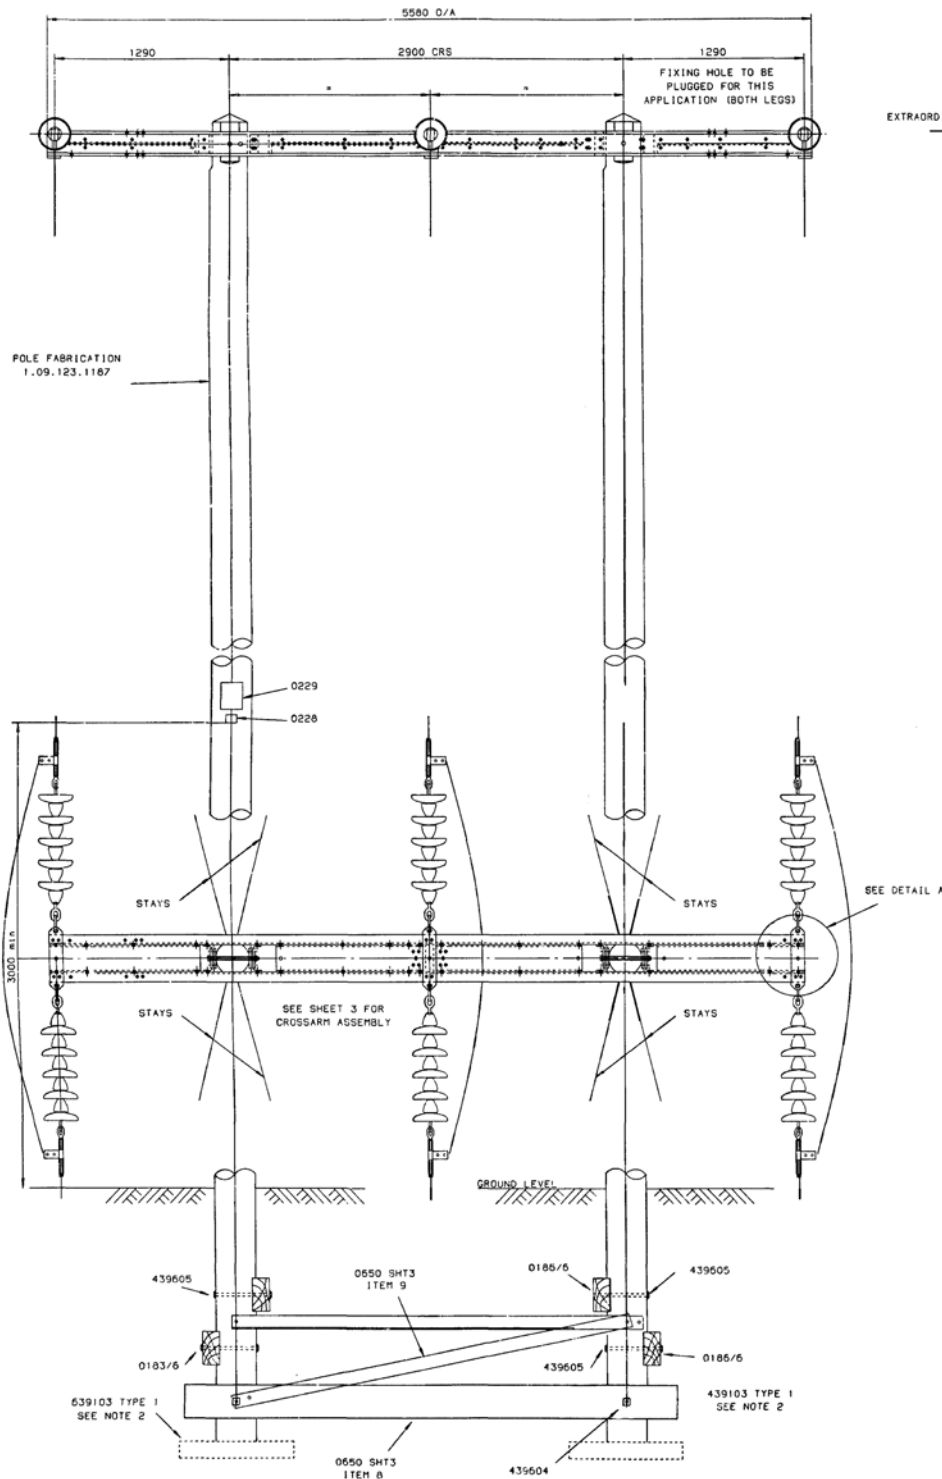

- NOTES
1. ALL POLE BOLTS TO BE M20 UNLESS OTHERWISE STATED
 2. FOOTING USED WHEN REQUIRED TO CONSIST OF 2 No WOOD BAULKS LAID TOGETHER TO FORM 500 x 850 BASE AND INSTALLED AT EACH POLE LEG.
 3. DETAILED DRGS PREFIXED 43... REFER TO ES1 BASED DRAWINGS AND OTHER DETAILED DRGS REFER TO 1.09.101 SERIES.
 4. CLEARANCE BETWEEN PHASE AND STEELWORK OR TIMBER TO BE 700 MIN. CLEARANCE BETWEEN DISSIMILAR PHASES TO BE 1500 MIN.
 5. ALL STEELWORK FIXING BOLTS TO BE COMPLETE WITH 1 No ROUND WASHER UNDER NUT AND 1 No ROUND WASHER UNDER BOLT HEAD UNLESS SPECIFIED OTHERWISE.
 6. REFERENCE CROSSARM FIXING DETAIL INDICATES PLATES DEPLOYED UNDER NORMAL CONDITIONS.
 7. ARRANGEMENTS NOT NORMALLY USED FOR POLES OF GREATER THAN 17.0M LENGTH.

POLE LENGTH	DIM X
UP TO AND INCLUDING 12.0M	2.0M
13.0M TO 15.0M INCLUSIVE	2.2M
16.0M TO 18.0M INCLUSIVE	2.4M

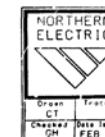

WORK SPEC No 04/22

Northern Electric - Central House - Newcastle upon Tyne NE1 0NE

66kV SINGLE CIRCUIT OVERHEAD LINES.
OUT OF BALANCE SECTION ARRANGEMENT TO
EXTRAORDINARY SECTION - NEW CONSTRUCTION

Drawn: CT
Checked: CH
Date Issued: FEB 87

Rev'd: 2
Revised: JAN 86 CT

Scale: 1:20