



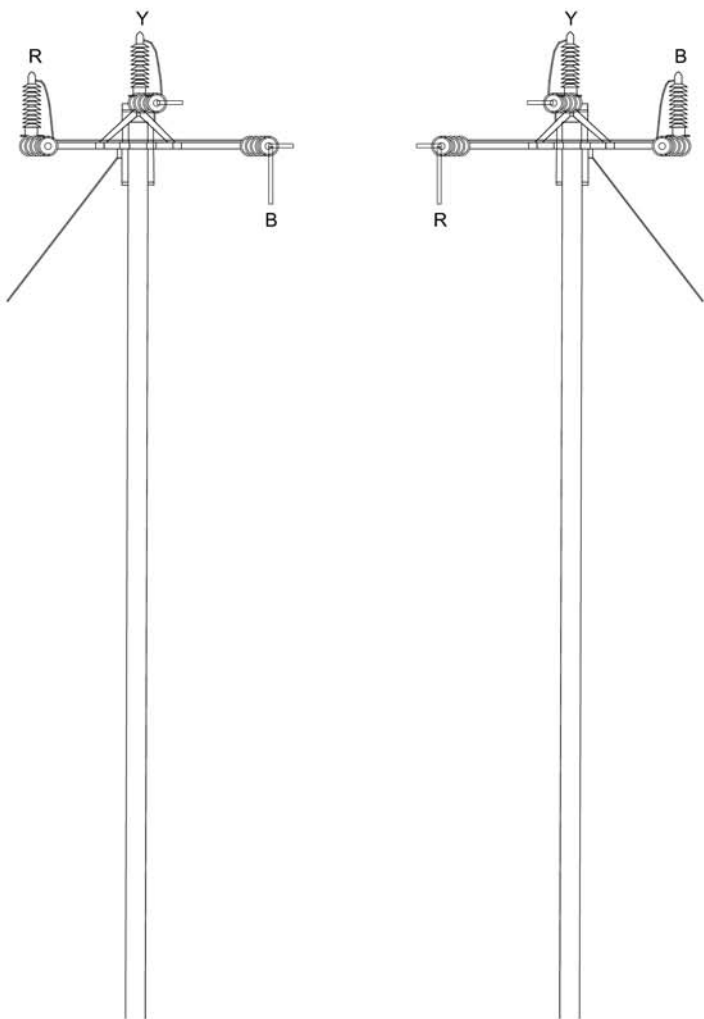

SINGLE POLE ARRANGEMENT

1.09.123.1192

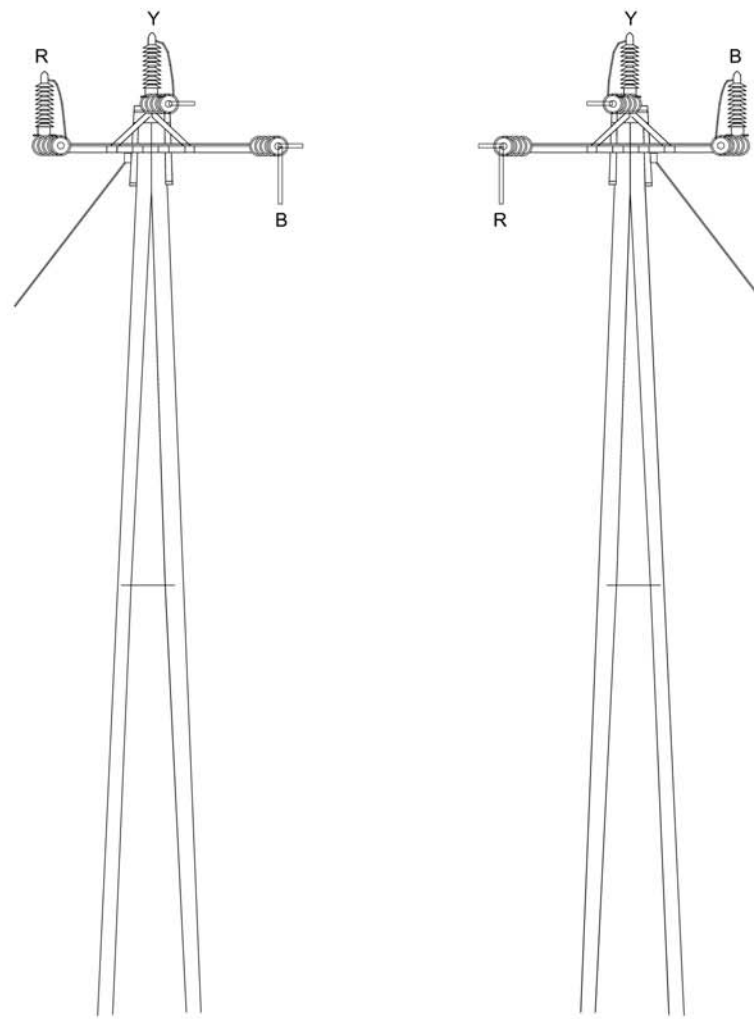

SECTION 'A' POLE ARRANGEMENT

		Lloyds Court, 78 Grey Street, Newcastle Upon Tyne, NE1 6AF	
Manufacturer Details		OUTLINE OF SECTION ANGLE 'A' POLE ARRANGEMENT. NORMAL SPAN - SMALL ANGLE SINGLE POLE ARRANGEMENT NORMAL SPAN - MEDIUM ANGLE	
Sheet No. X	Scale 1:100	Type OVERHEAD	POLES
Prepared By Barbara Simpson		Ref No. C948830	Historic Drg.No. 1091231192
Revised 30/05/07	Grid Reference	Revision Notes	
Date Issued 30/05/07	Checked By M WILSON		