

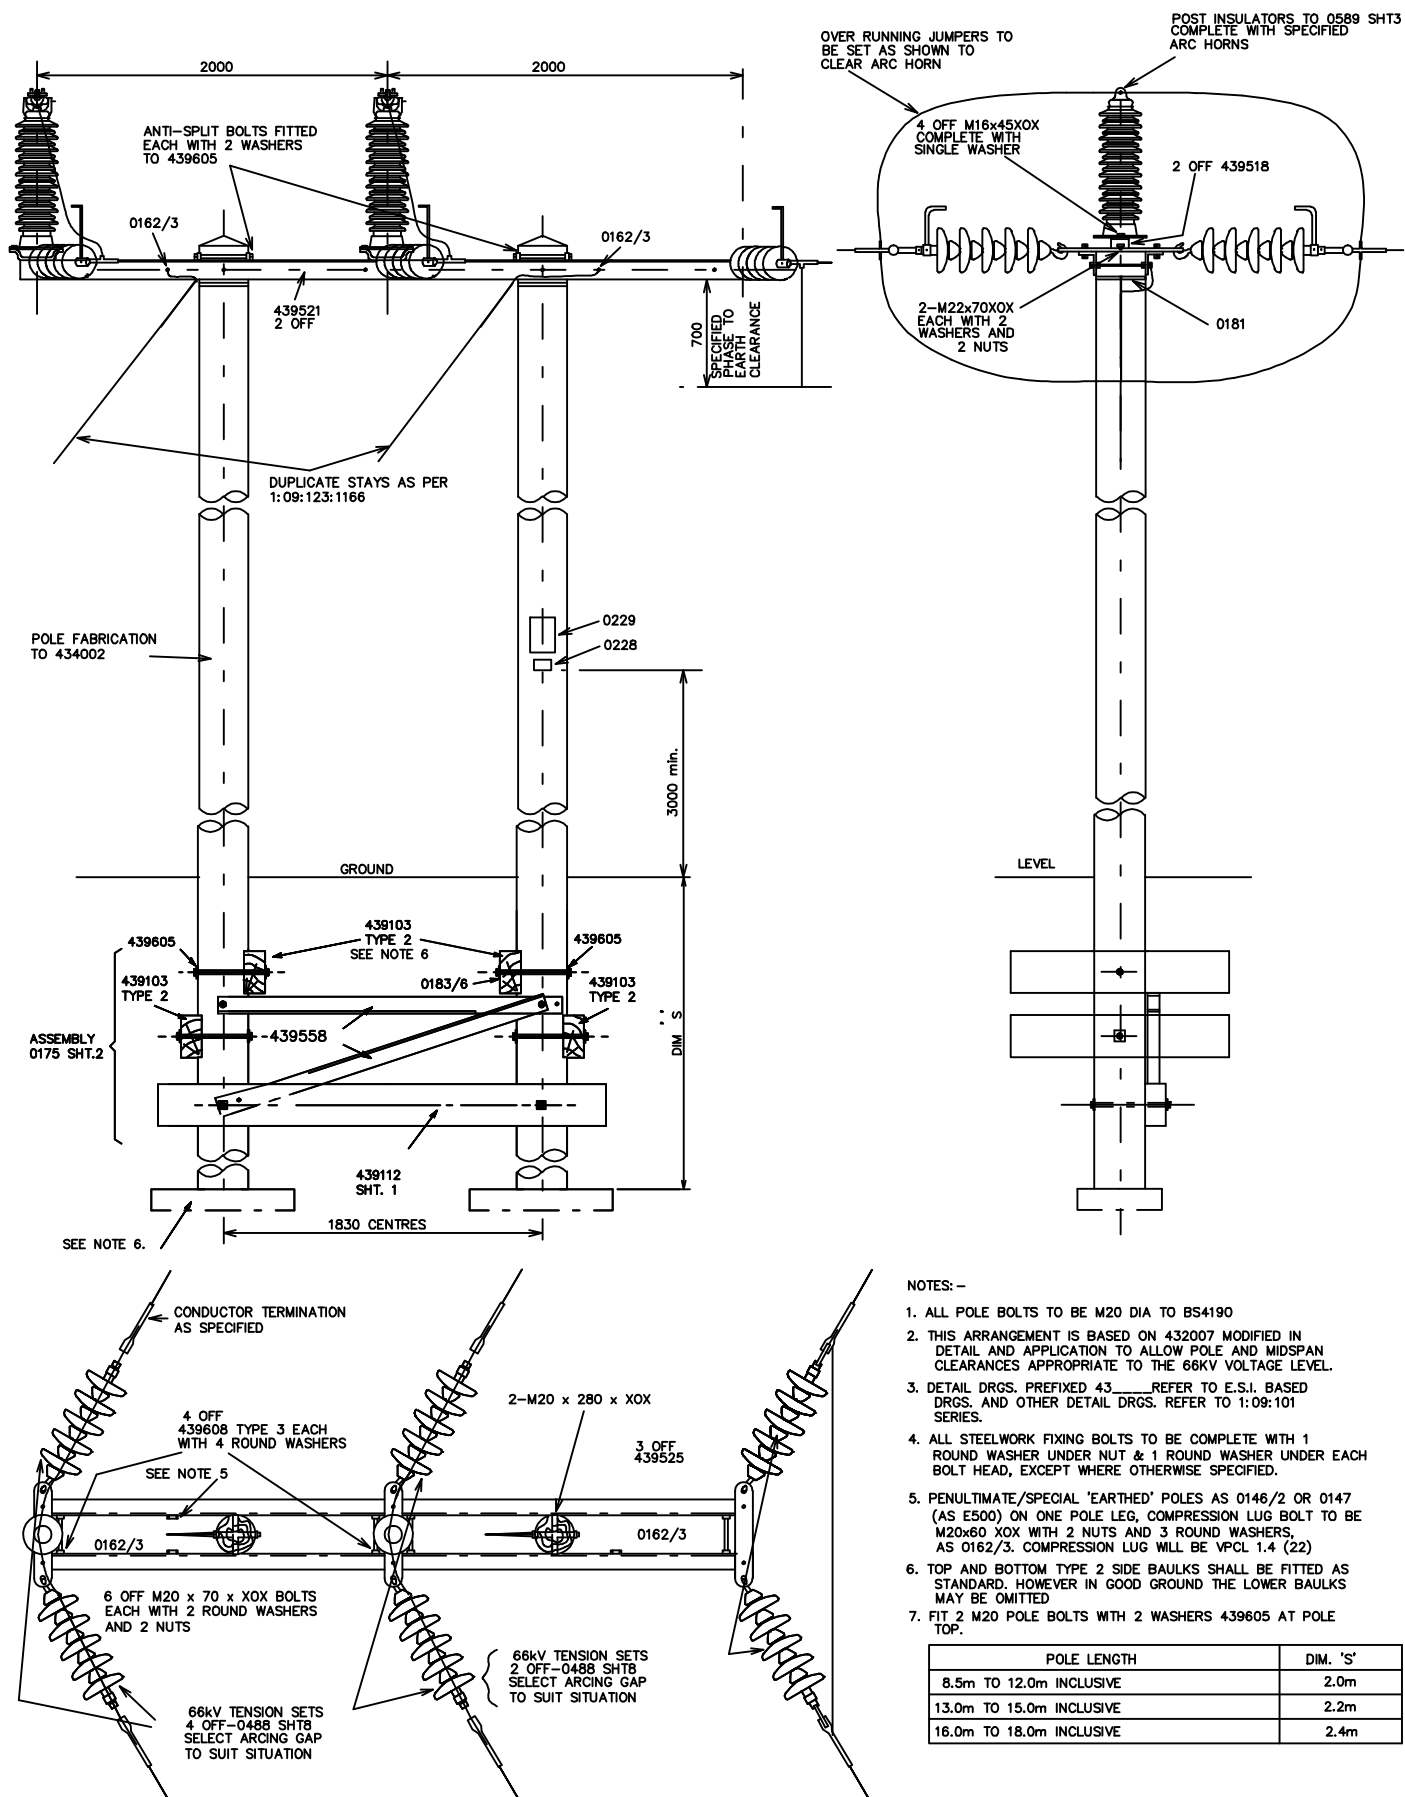


FIG 1

WORK SPEC. 04/243

ALL DIMENSIONS SHOWN ARE IN MILLIMETRES UNLESS OTHERWISE STATED

		Northern Electric Distribution Limited, Carlisle House, Newcastle Upon Tyne, NE1 6NE.	
66kV SINGLE CIRCUIT LINES NARROW CENTRED 'H' POLE FOR NORMAL SPANS HEAVY ANGLE APPLICATION			
Prepared by B.F.R.	Drg.No. 1 09 123 1193	Sheet No. 1	
Checked (date issued) 6/08/11 NOV '81	Mod. K.L.M.	Revised SEP '99 (RC)	
		Scale 1:20	