


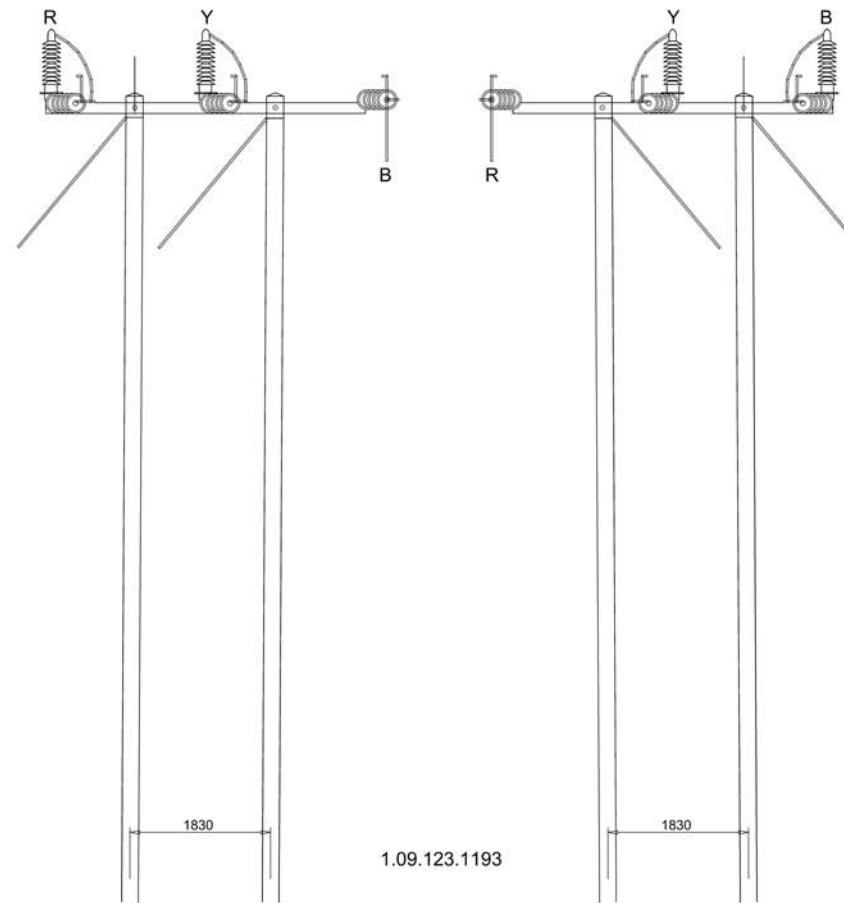

		Lloyds Court, 78 Grey Street, Newcastle Upon Tyne, NE1 6AF	
Manufacturer Details		OUTLINE OF SECTION ANGLE NARROW CENTRED 'H' POLE NORMAL SPANS - HEAVY ANGLE	
Sheet No. X	Scale 1:100	Type OVERHEAD	POLES
Prepared By Barbara Simpson	Grid Reference	Ref No. C948843	Historic Drg.No.
Revised 30/05/07	Checked By M WILSON	Revision	Notes
Date Issued 30/05/07			1091231193