


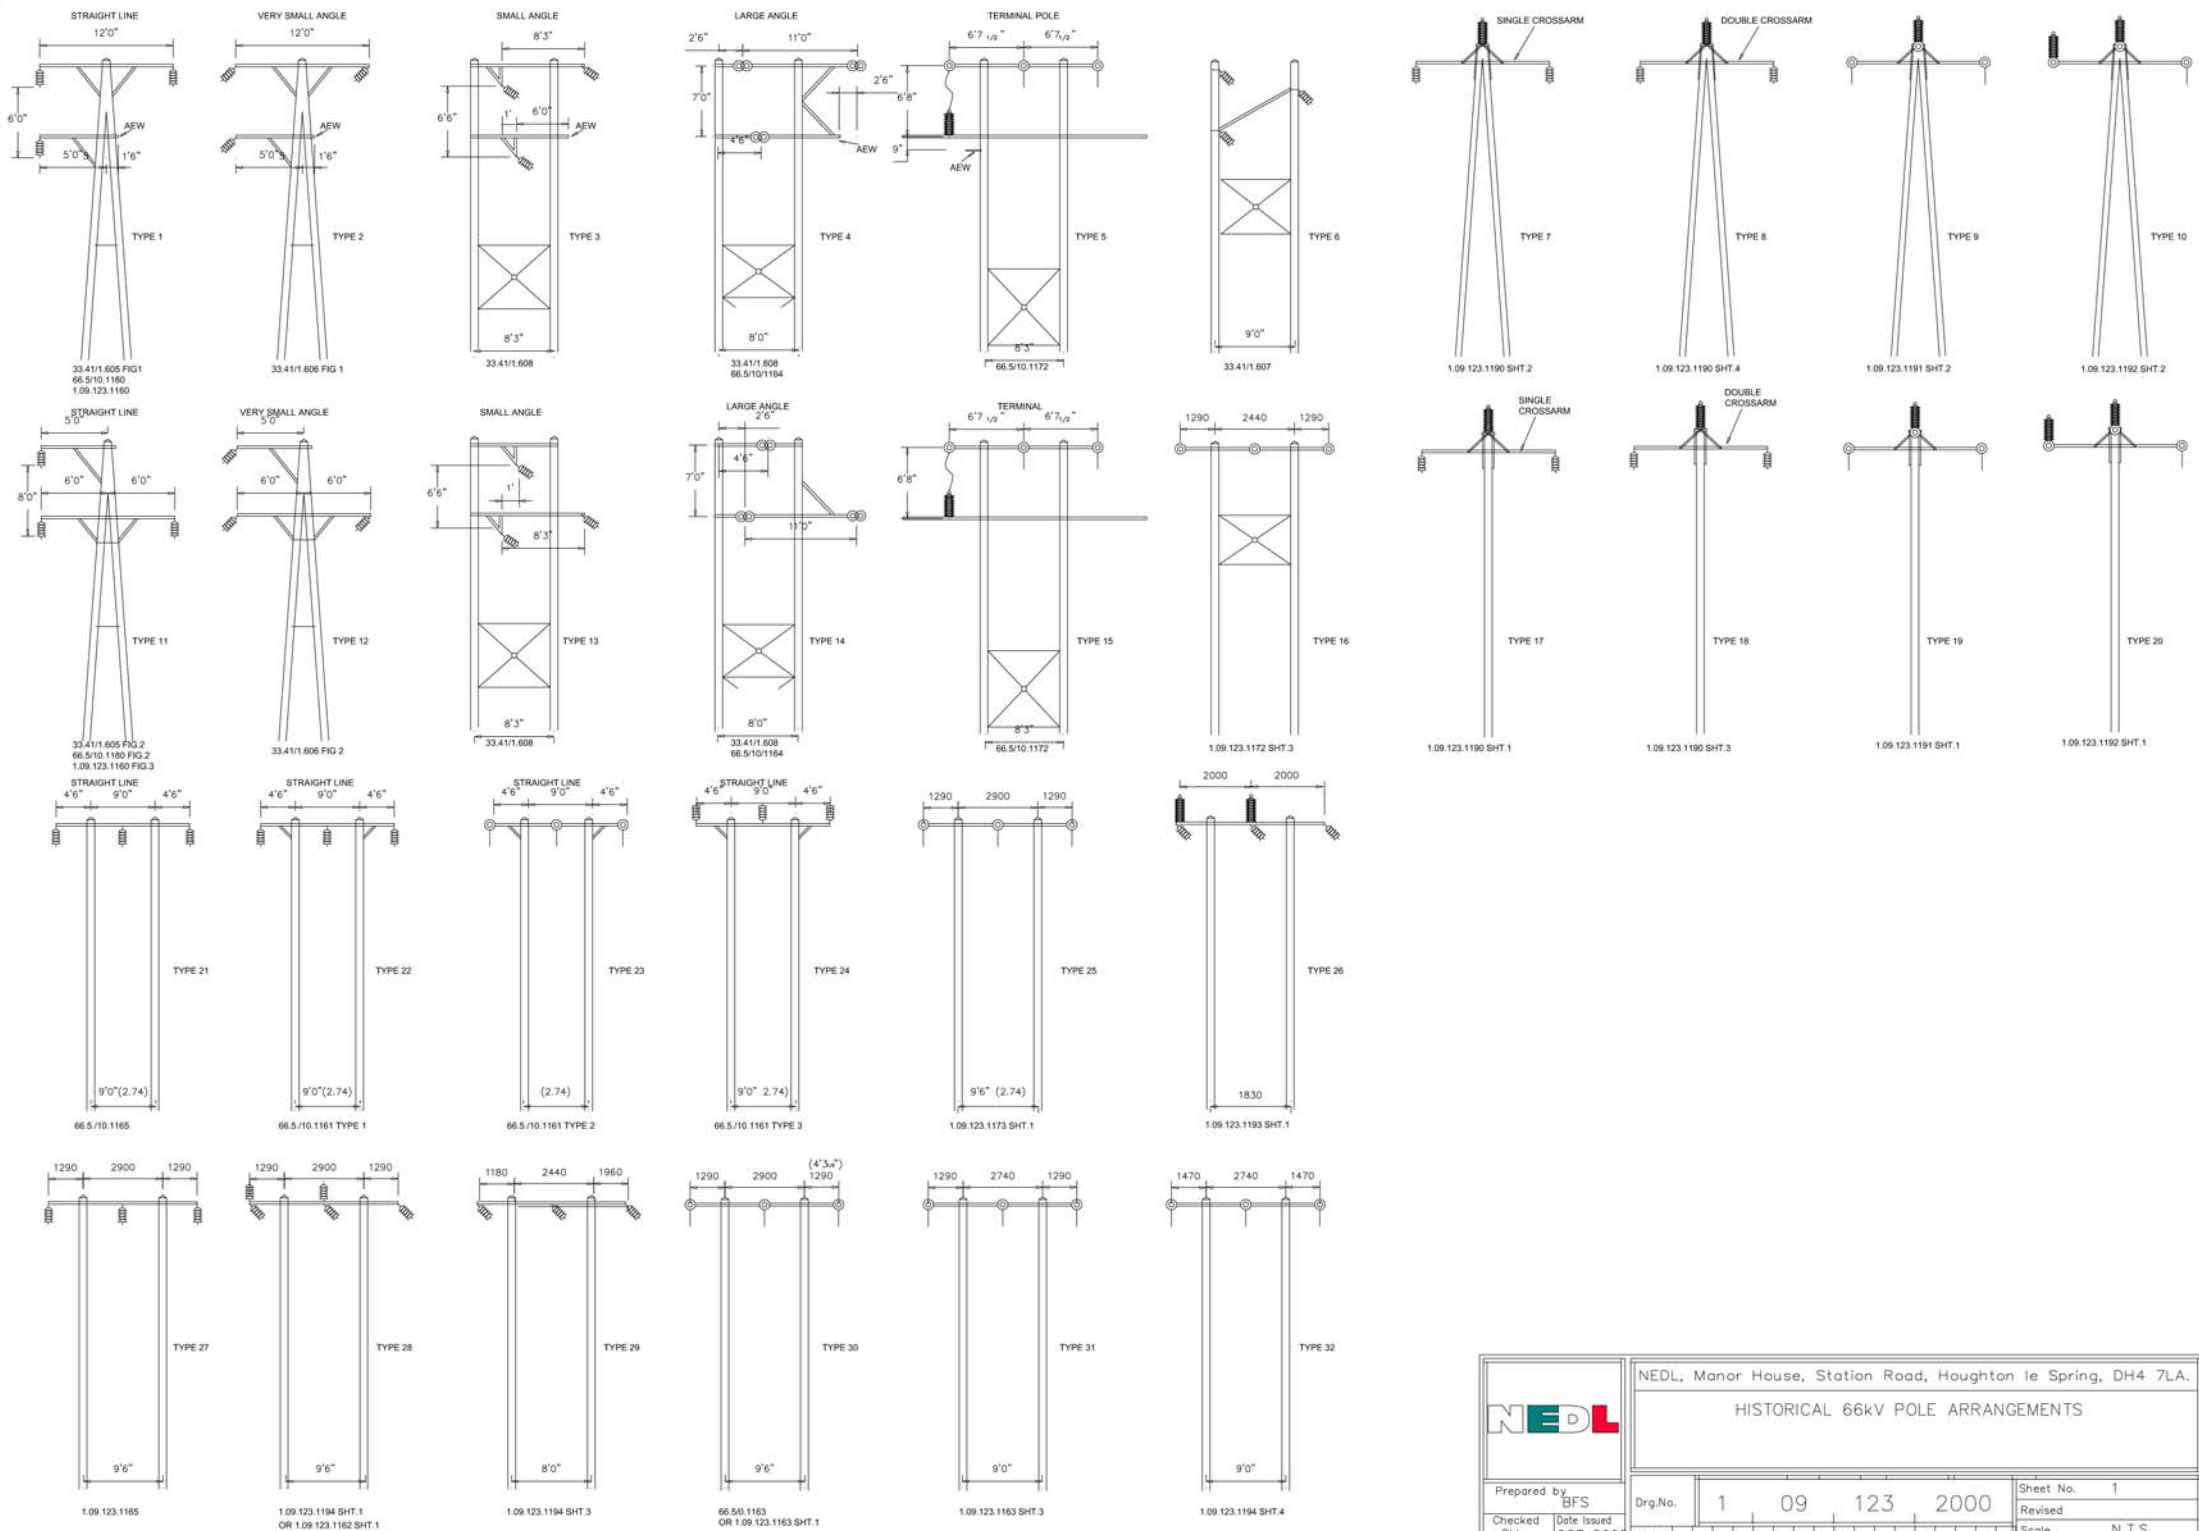

		NEDL, Manor House, Station Road, Houghton le Spring, DH4 7LA.			
		HISTORICAL 66kV POLE ARRANGEMENTS			
Prepared by BFS	Drg.No.	1	09	123	2000
Checked GH	Date Issued OCT 2000	Sheet No. 1			Revised
Mod.			Scale N.T.S.		