



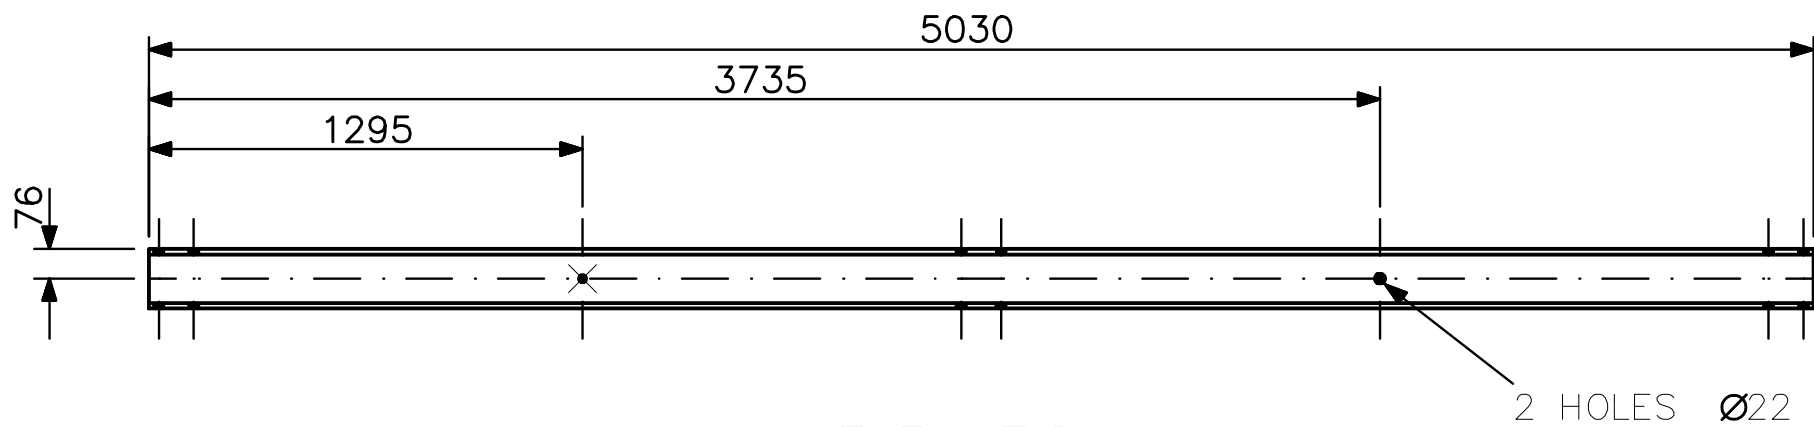

ELEVATION

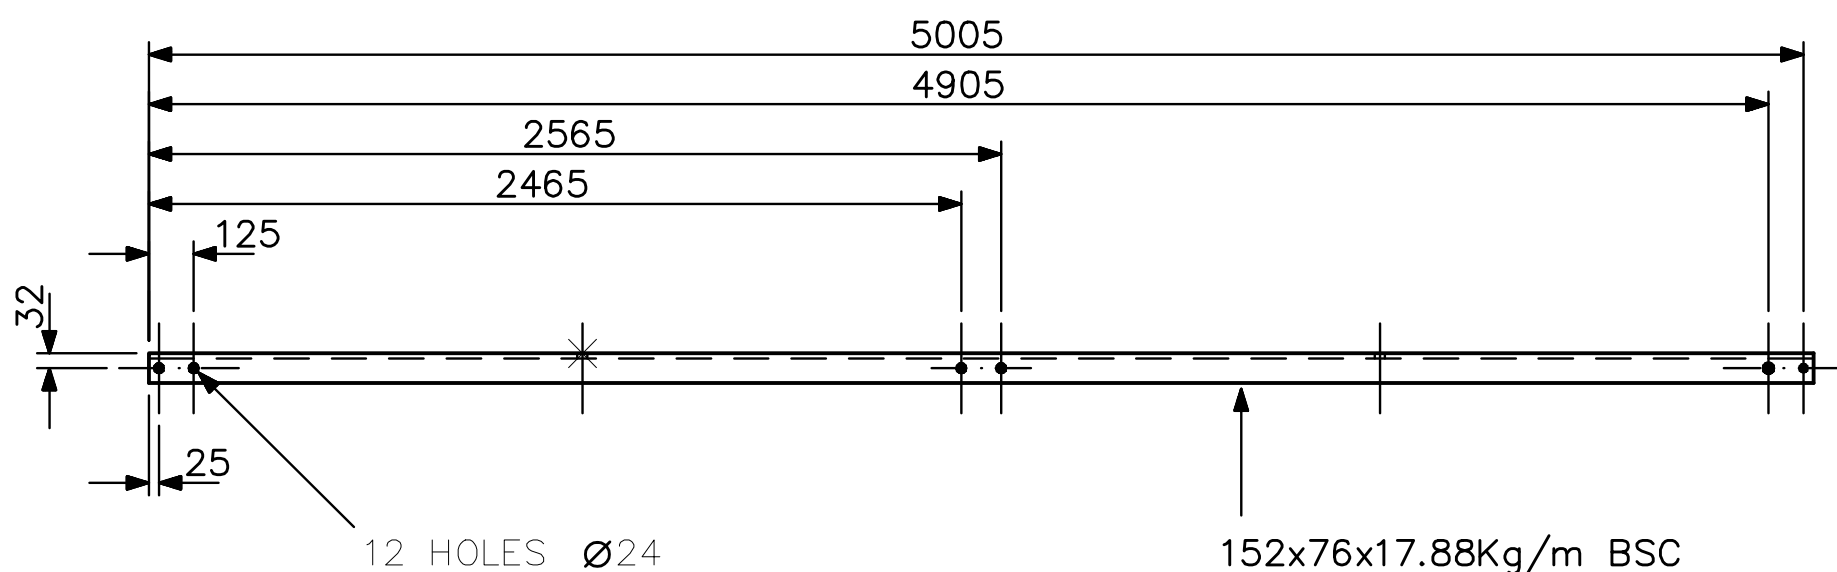

PLAN

ALL STEELWORK TO BE IN
ACCORDANCE WITH BS4360
GRADE 43A AND BS4 PART 1
GALVANISED IN ACCORDANCE
WITH BS729

DIMENSIONS IN MILLIMETRES

 CE Electric UK		Lloyds Court, 78 Grey Street, Newcastle Upon Tyne, NE1 6AF			
		OVERHEAD LINES CE / C / 37 CROSSARM STEELWORK INTERMEDIATE SUPPORT			
Manufacturer Details					
Sheet No. 1	Scale N.T.S.				
Prepared By Janis.Webb		Type OVERHEAD		LINES	
Revised 29/05/07	Grid Reference	Ref No.	C948771	Historic Drg.No.	Y204L0901
Date Issued 25/05/07	Checked By	Revision A Notes			