



ELEVATION

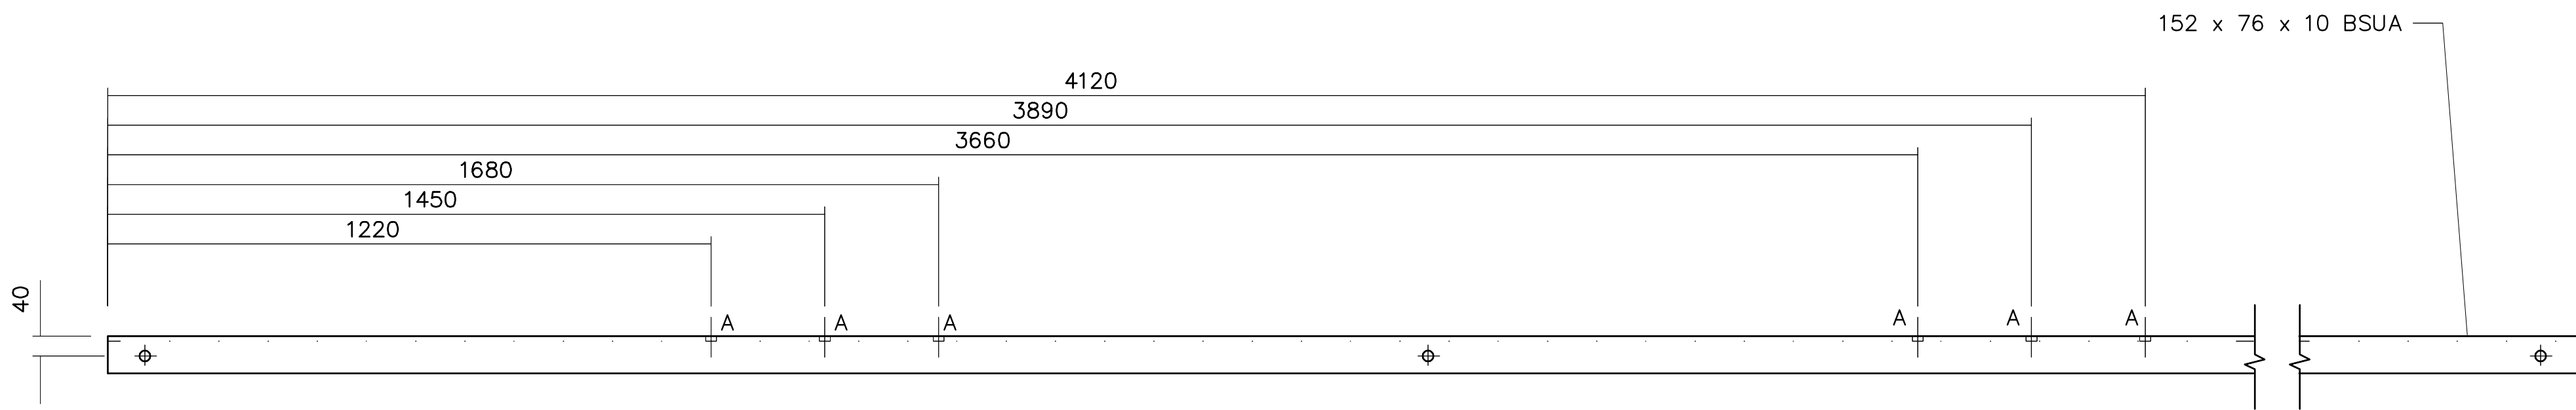


PLAN

ITEM No. 1


2 No. REQUIRED

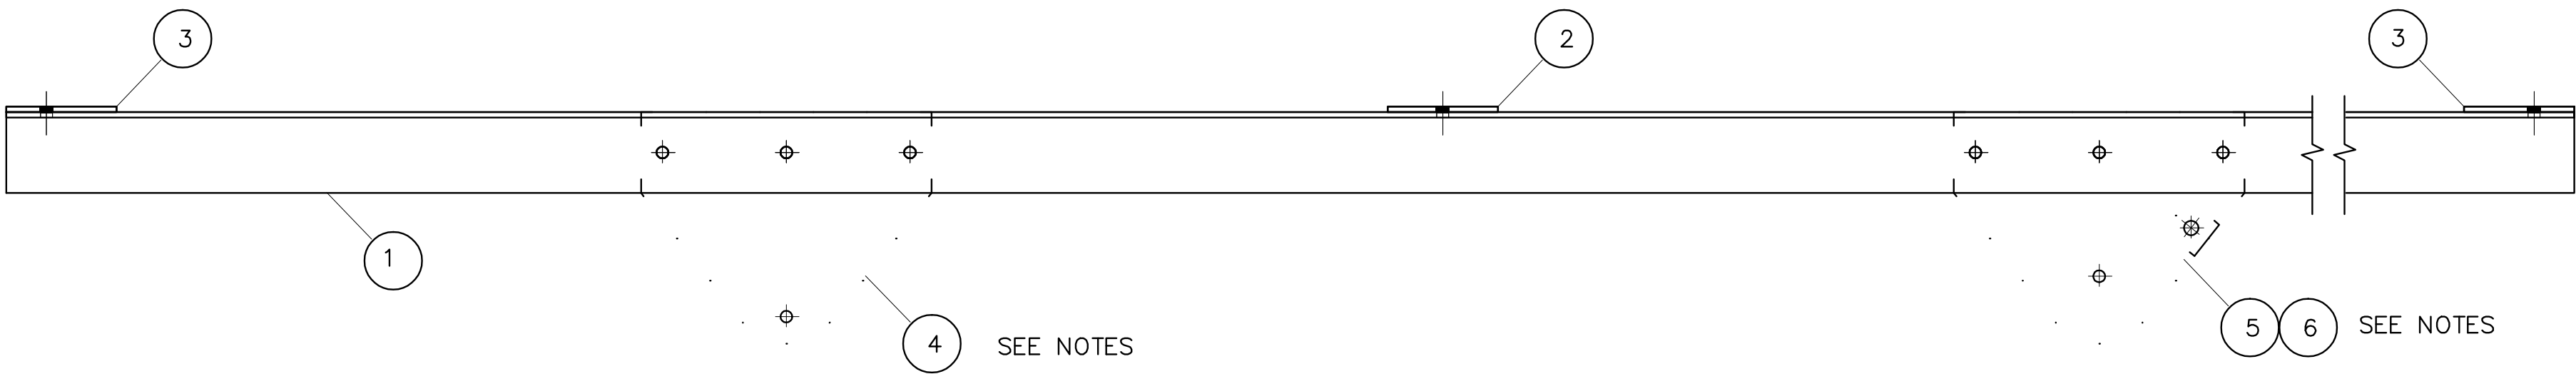

ELEVATION

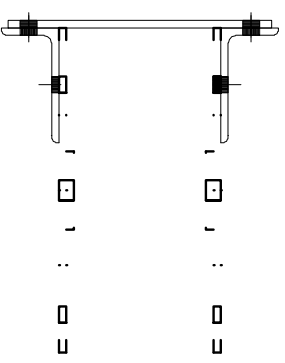


END ELEVATION

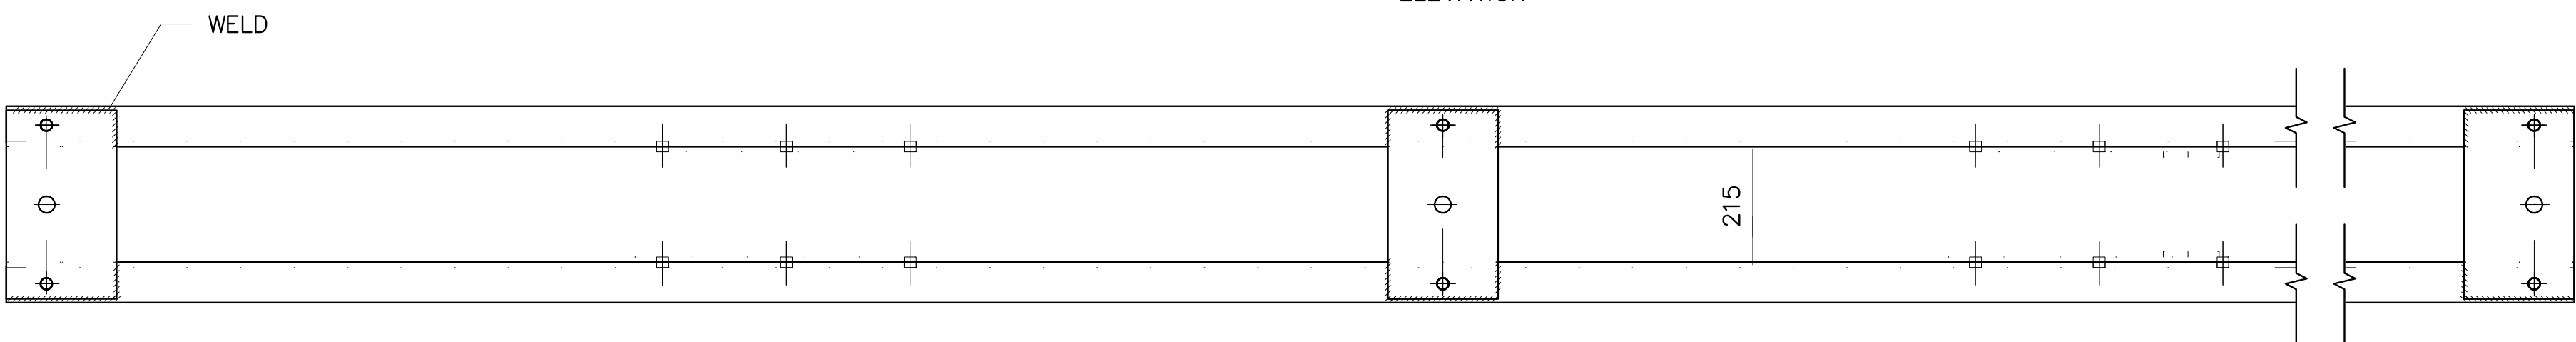


PLAN

TOP CROSSARM
WELDED ASSEMBLY OF ITEMS 1 , 2 & 3
1 No. REQUIRED

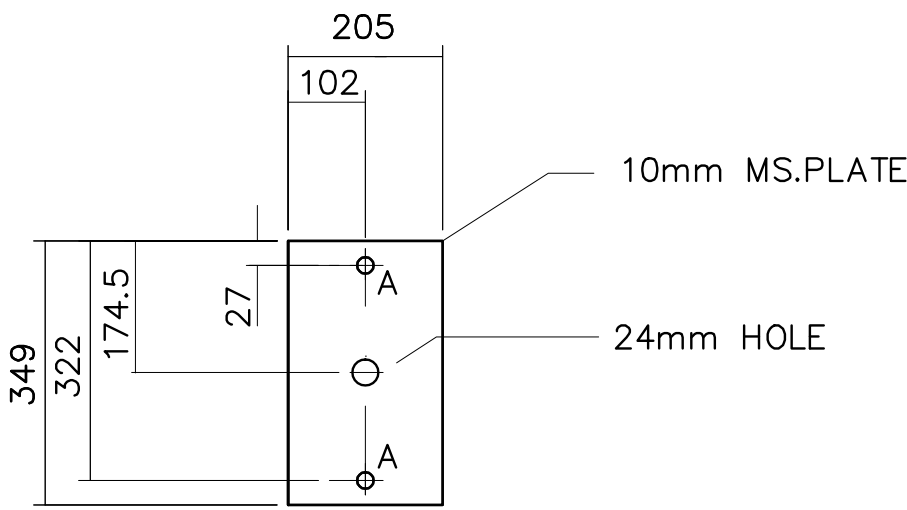

ITEM No. 2


1 No. REQUIRED

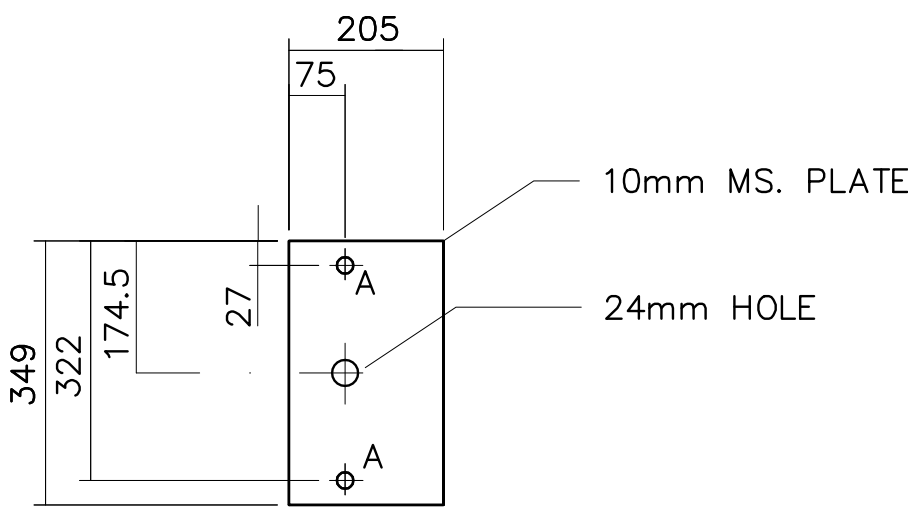

ITEM No. 3


2 No. REQUIRED

ITEMS 4,5 & 6 REQUIRED FOR ANGLE POSITIONS ONLY

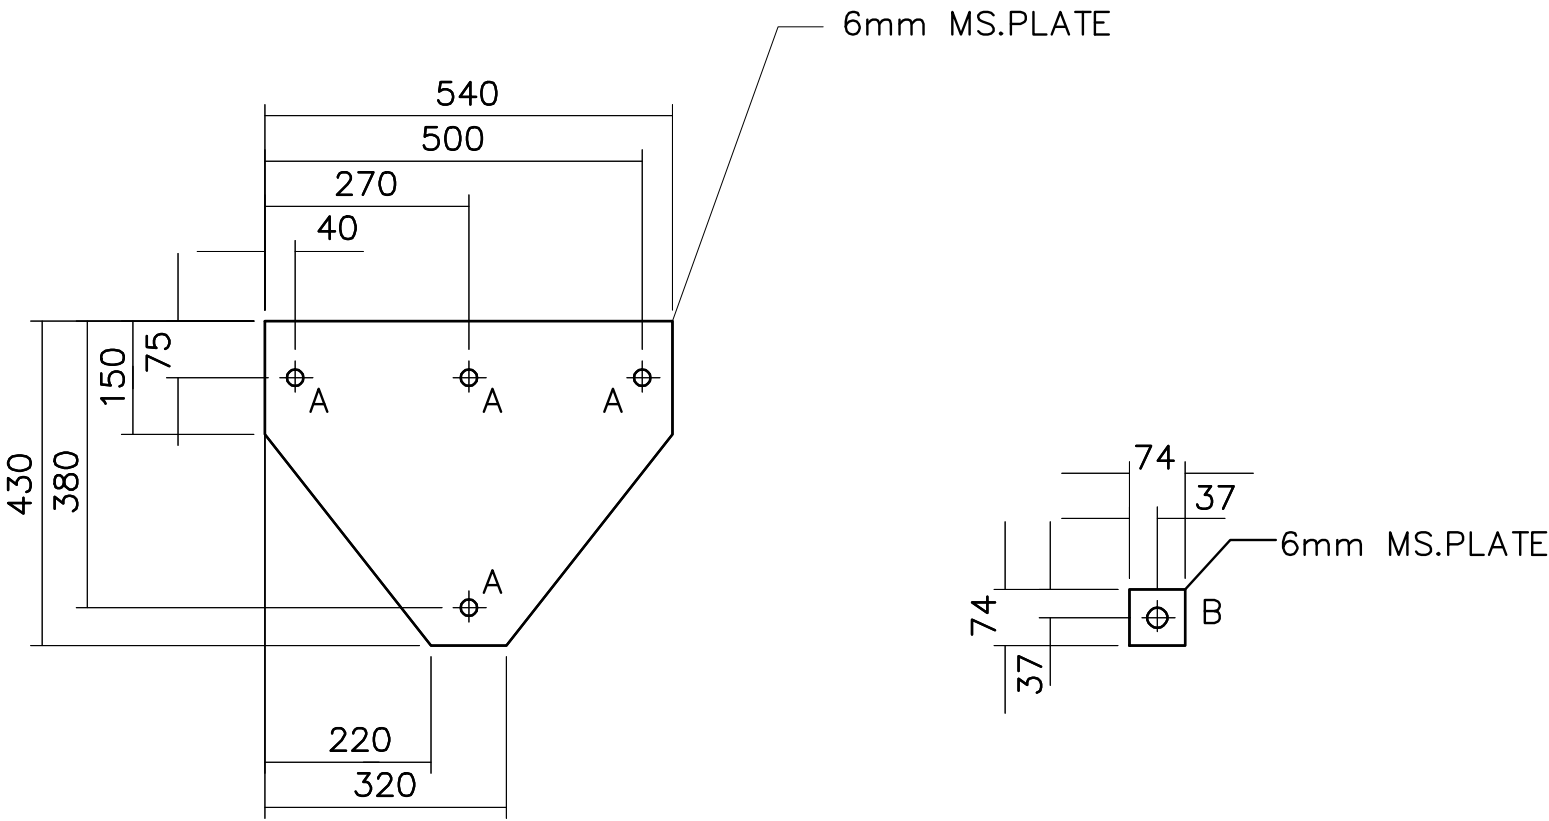


ITEM No. 4

2 No. REQUIRED

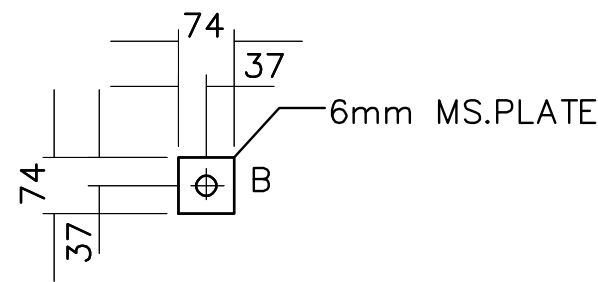


ITEM No. 5

2 No. REQUIRED

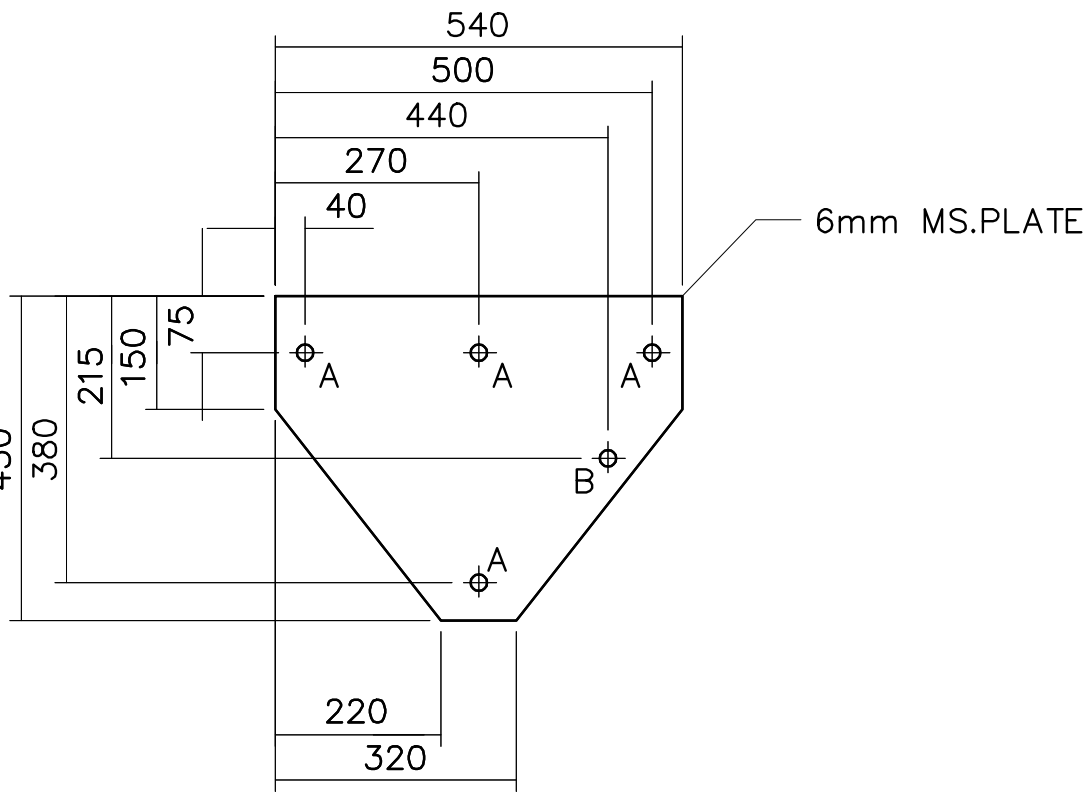


ITEM No. 6

2 No. REQUIRED

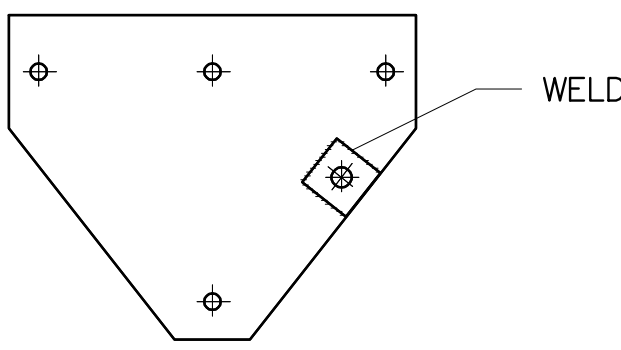

ELEVATION

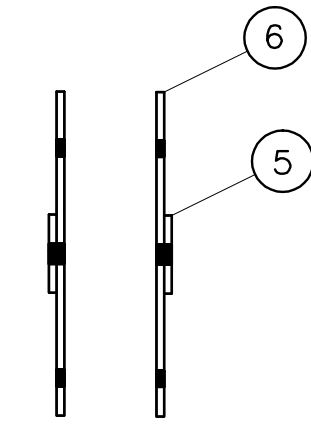

SIDE ELEVATION

GUSSET PLATE
WELDED ASSEMBLY OF ITEMS 5 & 6
1 SET REQUIRED

NOTES

HOLES MARKED "A" Ø22
HOLES MARKED "B" Ø27
ITEMS 4 & ASSEMBLY 5 & 6 SHOWN DOTTED
ARE ASSEMBLED ON SITE WITH THE TOP CROSSARM

ALL STEELWORK TO BS4848 PART 4 & BS4360 GRADE 43A
GALVANISED TO BS729
ALL WELDS TO BE 6mm FILLET AND SHOWN THUS 

		Lloyds Court, 78 Grey Street, Newcastle Upon Tyne, NE1 6AF	
Manufacturer Details		OVERHEAD LINES CROSSARM STEELWORK SECTION SUPPORT (& ANGLES UP TO 10 DEGREES) CE / C / 37 (M)	
Sheet No. 1	Scale 1:10	Type OVERHEAD	LINES
Prepared By Janis Webb	Grid Reference	Ref No. C948772	Historic Drg.No. Y204L0902
Revised 23/05/07	Checked By	Revision B	Notes
Date Issued 25/05/07			