



ELEVATION

SIDE ELEVATION

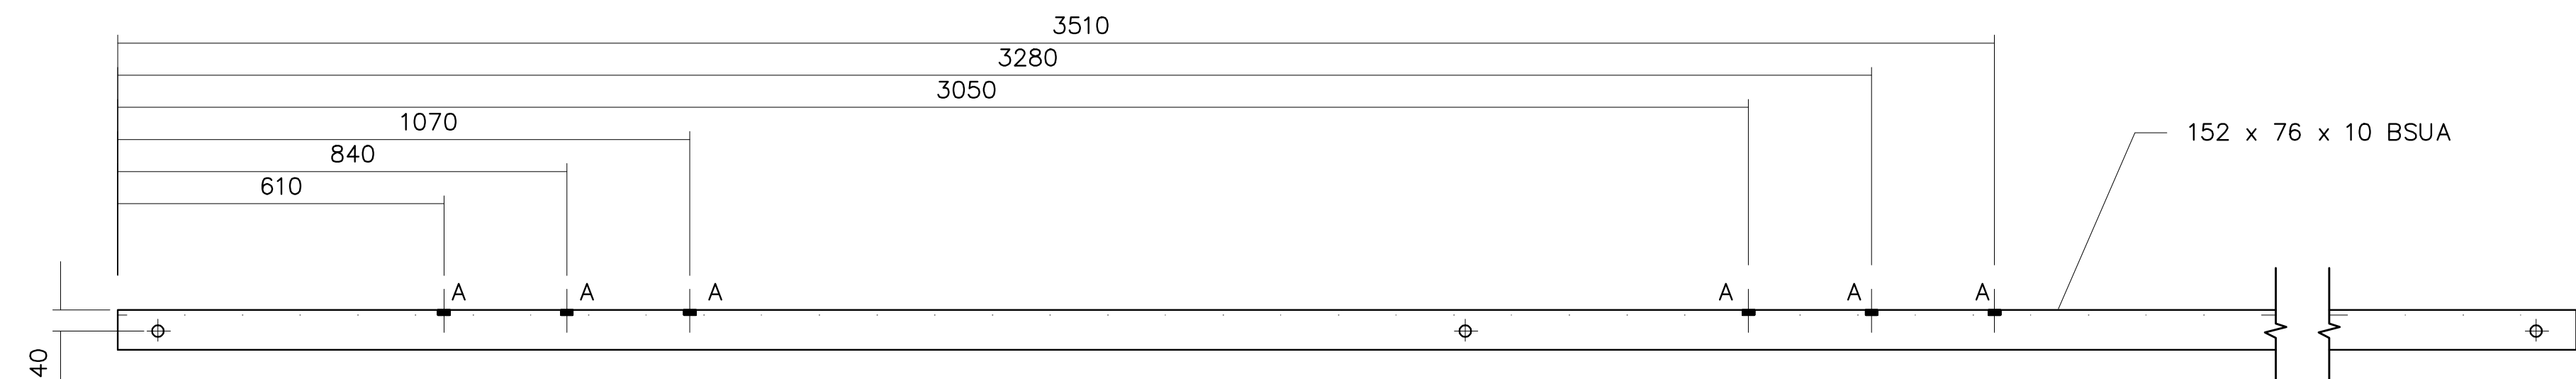


PLAN

ITEM No. 1
1 PAIR REQUIRED

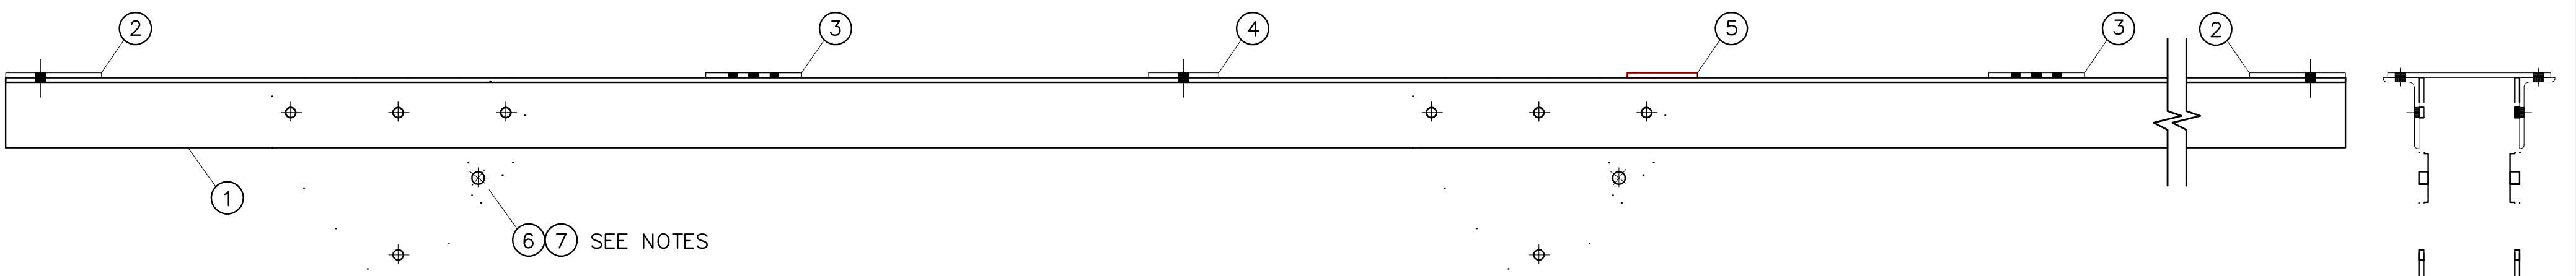


ELEVATION

END ELEVATION

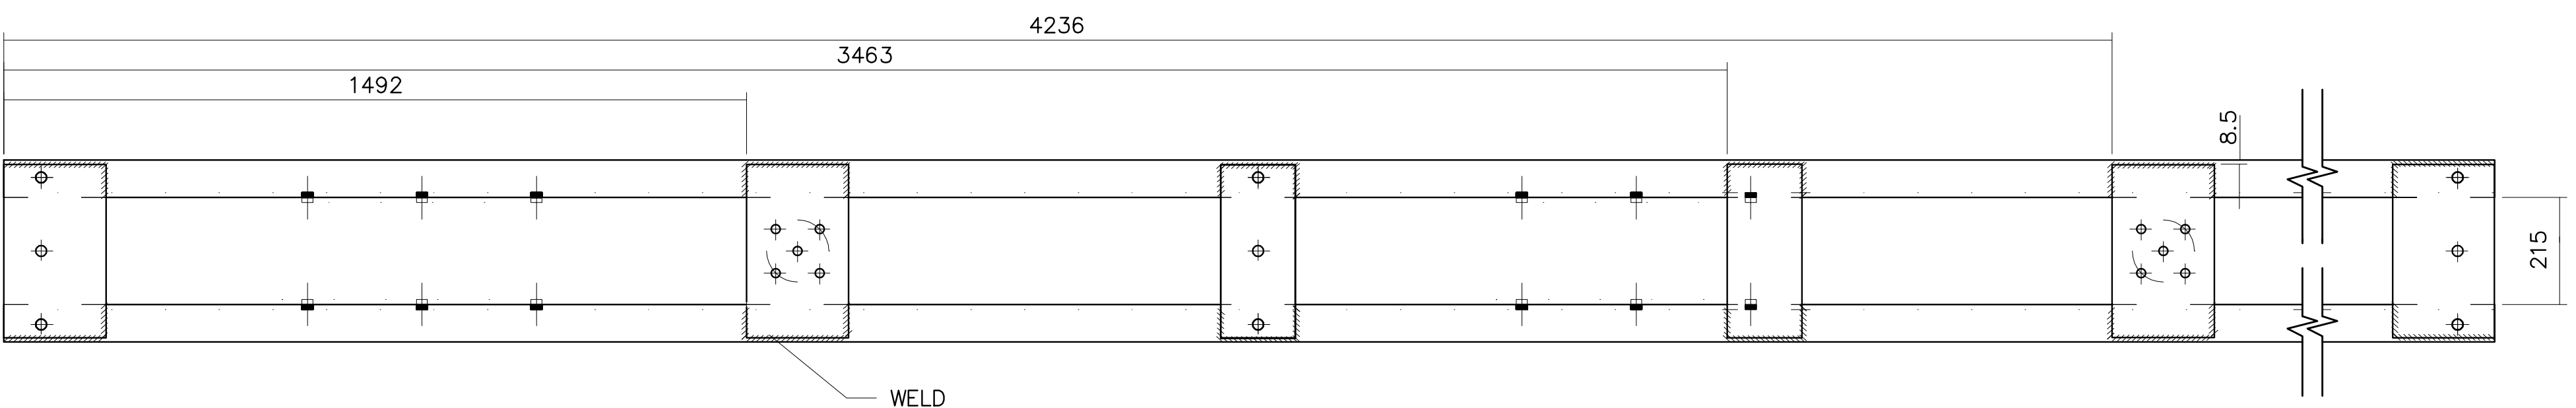


PLAN


TOP CROSSARM
WELDED ASSEMBLY OF ITEMS 1 , 2 , 3 , 4 & 5
1 No. REQUIRED

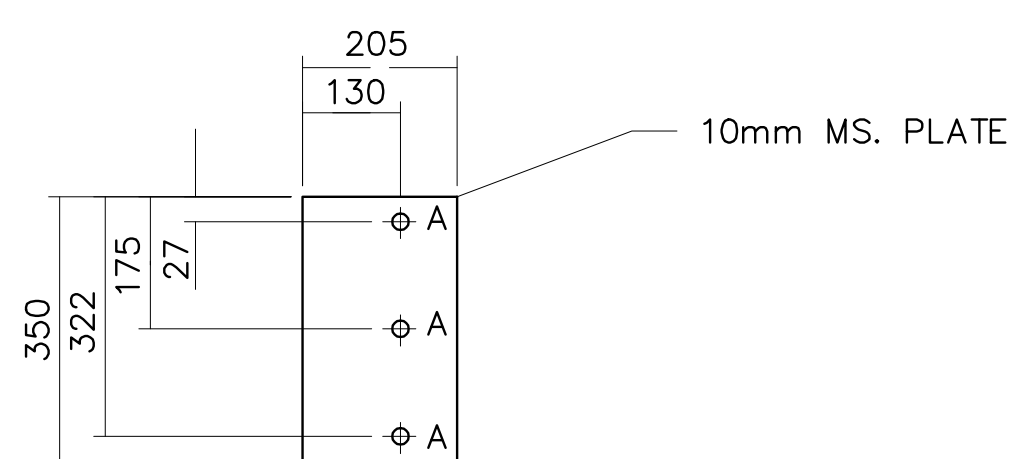


ITEM No. 2
2 No. REQUIRED

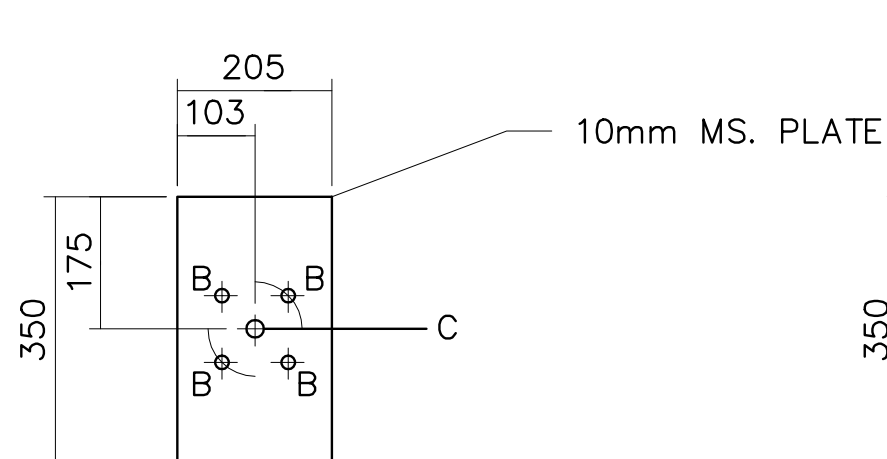


ITEM No. 3
2 No. REQUIRED

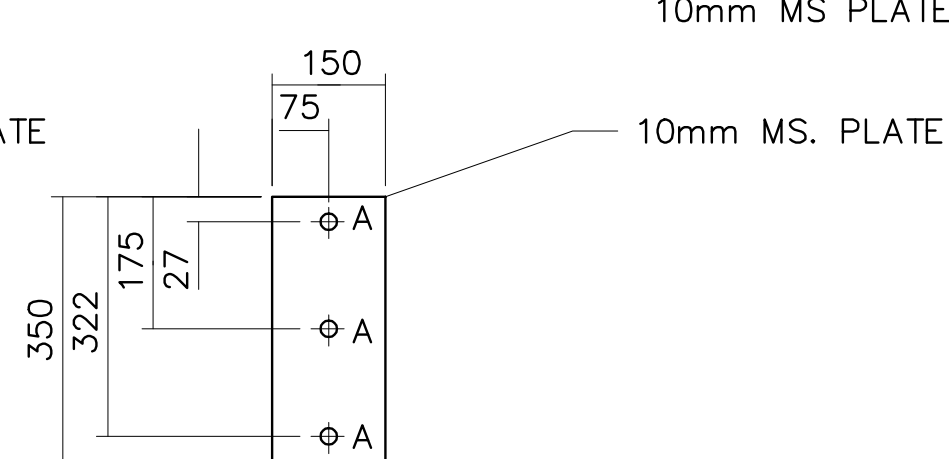


ITEM No. 4
1 No. REQUIRED

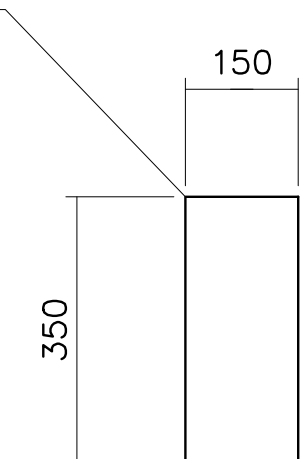


ITEM No. 5
1 No. REQUIRED

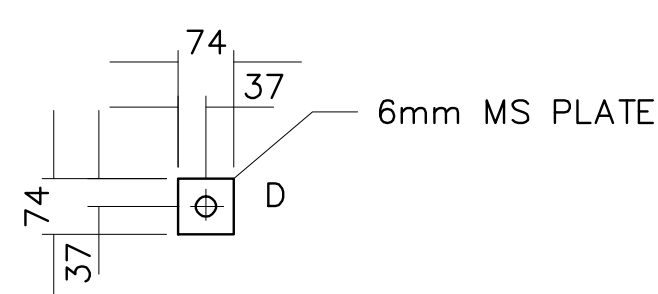


ITEM No. 6
4 No. REQUIRED

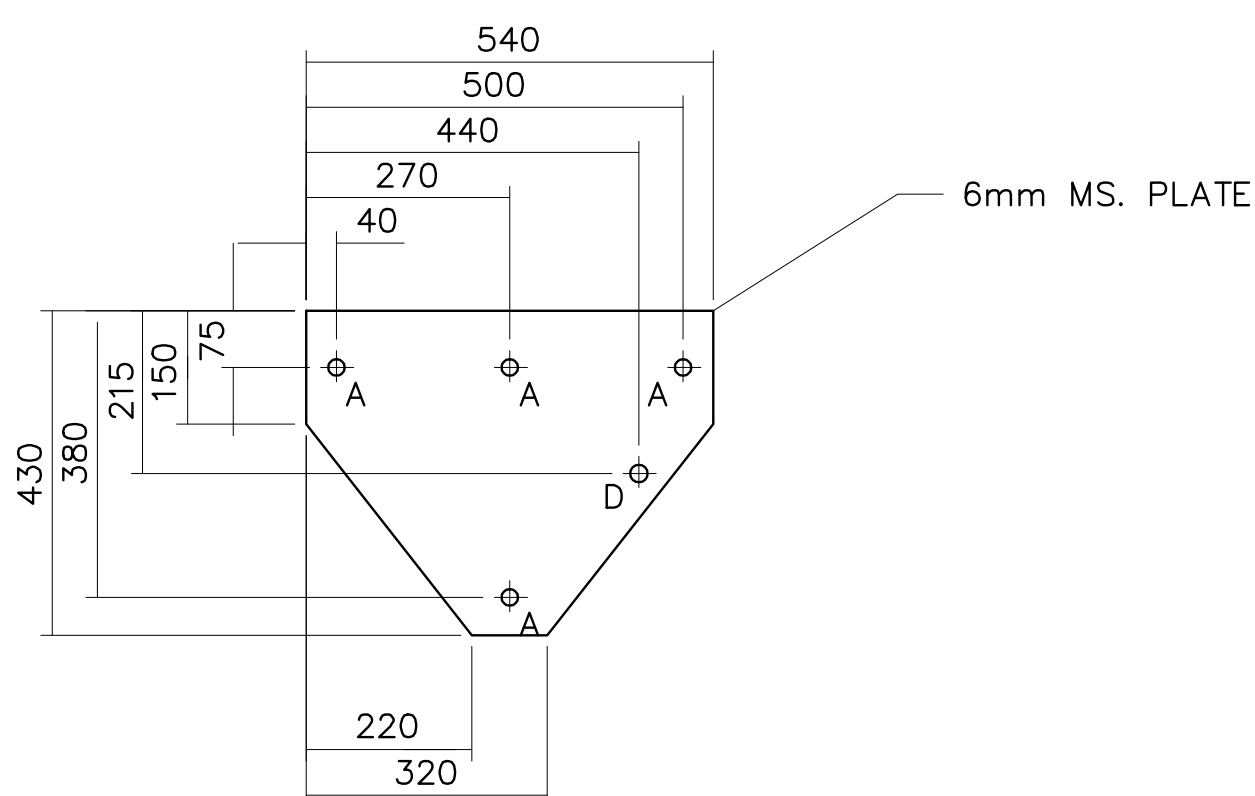

ITEM No. 7
4 No. REQUIRED

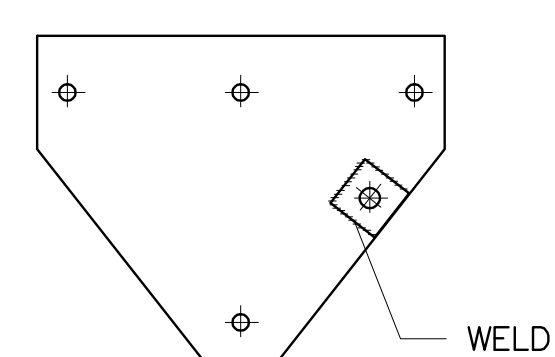

ELEVATION

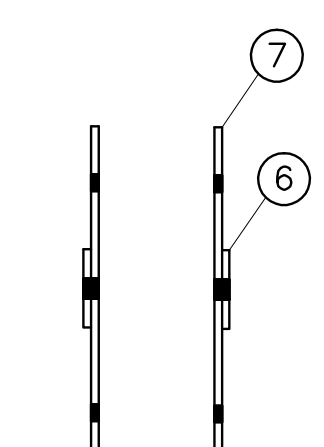

SIDE ELEVATION

GUSSET PLATE
WELDED ASSEMBLY OF ITEMS 6 & 7
2 SETS REQUIRED

NOTES
HOLES MARKED "A" ϕ 22
HOLES MARKED "B" ϕ 18 ON 127 PCD
HOLES MARKED "C" ϕ 24
HOLES MARKED "D" ϕ 27
ASSEMBLY 6 & 7 SHOWN DOTTED ARE ASSEMBLED
ON SITE WITH THE TOP CROSSARM

ALL STEELWORK TO BS4848 PART 4
& BS4360 GRADE 43A
GALVANISED TO BS729
ALL WELDS TO BE 6mm FILLET ARE
SHOWN THUS

		Lloyds Court, 78 Grey Street, Newcastle Upon Tyne, NE1 6AF	
Manufacturer Details		OVERHEAD LINES CROSSARM STEELWORK ANGLE SUPPORT (ANGLES 10 - 60 DEGREES) CE / C / 37 (M)	
Sheet No. 1	Scale 1:10	Type OVERHEAD	LINES
Prepared By Jania Webb	Grid Reference	Ref No. C948773	Historic Drg.No. Y204L0903
Revised 23/05/07	Checked By	Revision	Notes
Date Issued 25/05/07			