

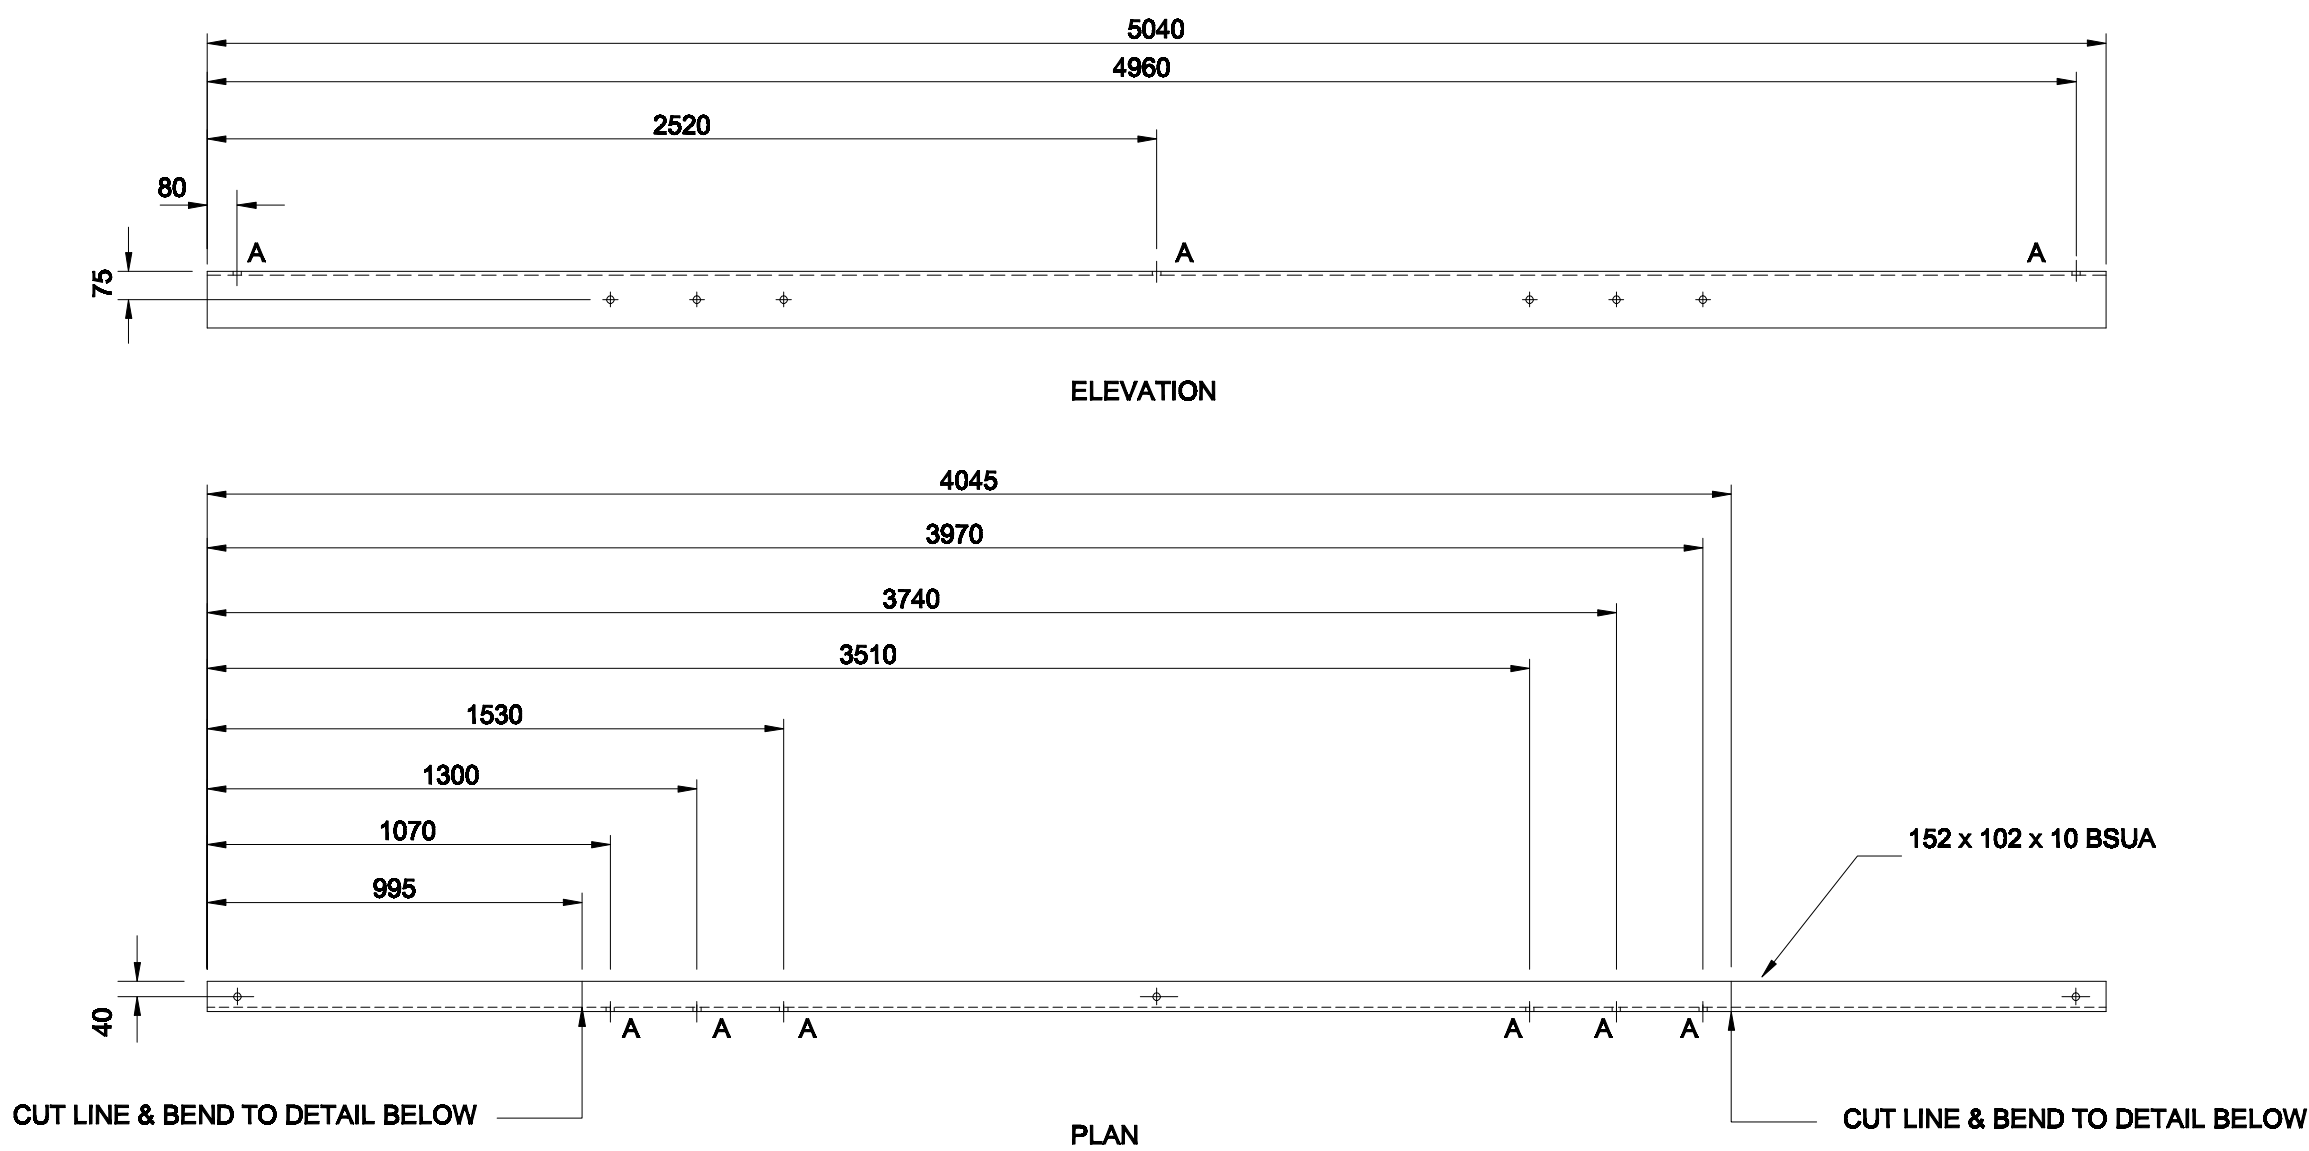
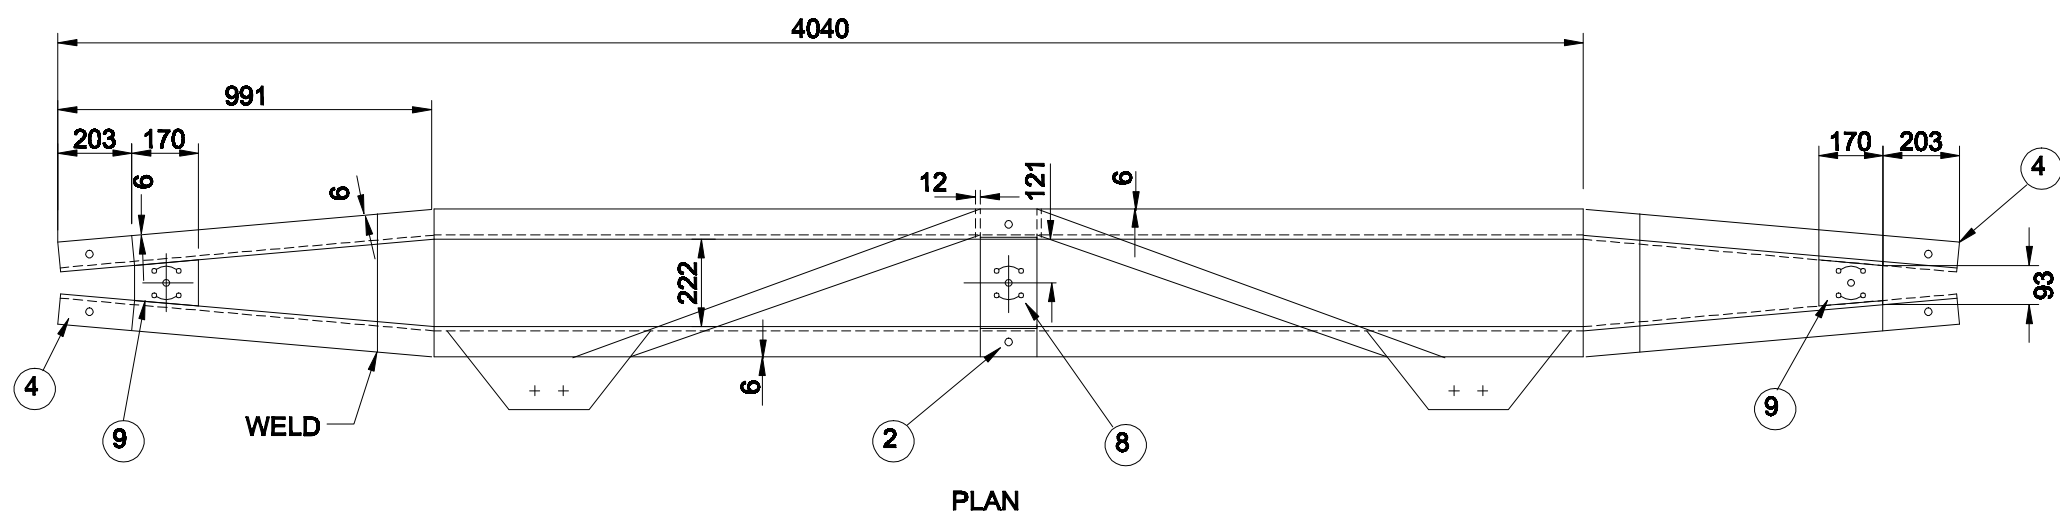
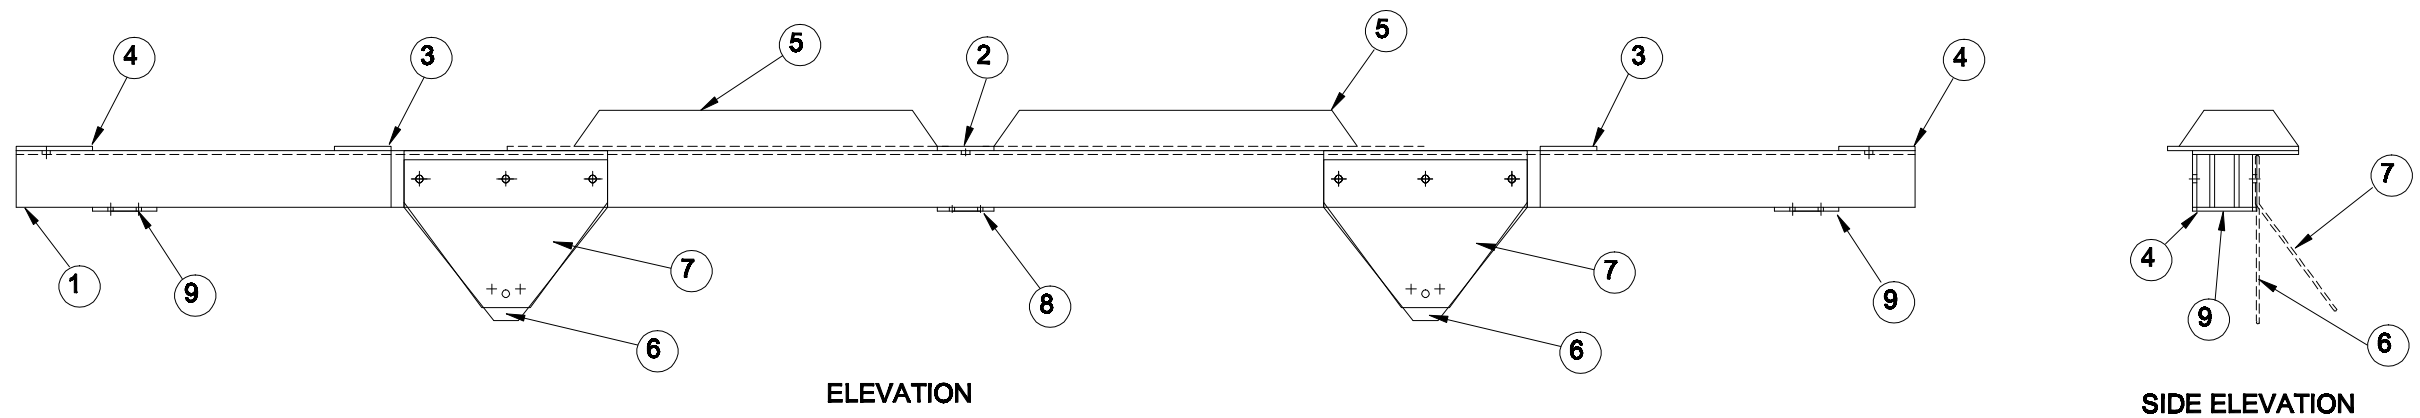
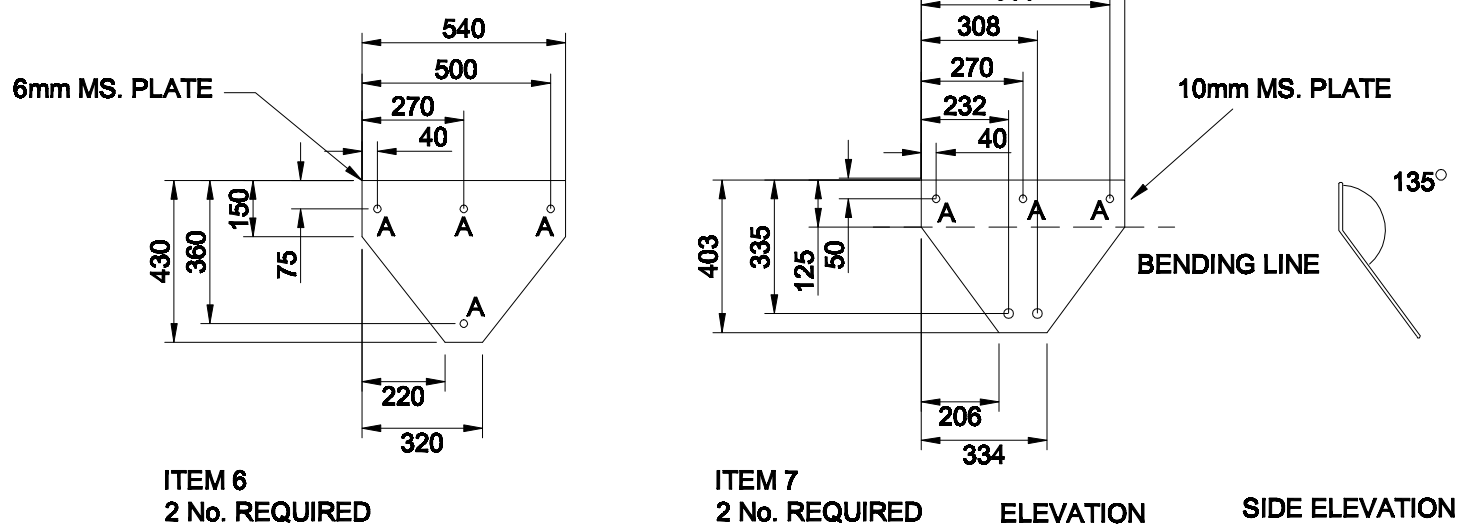
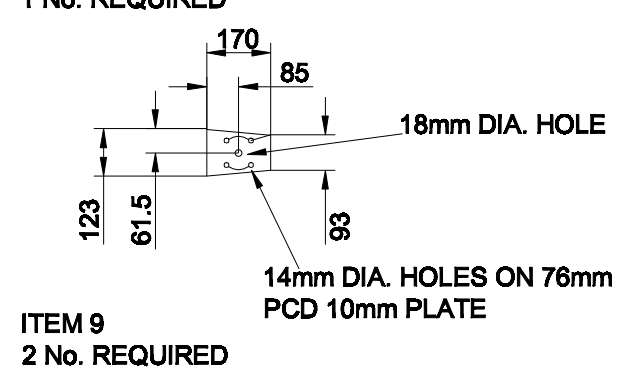
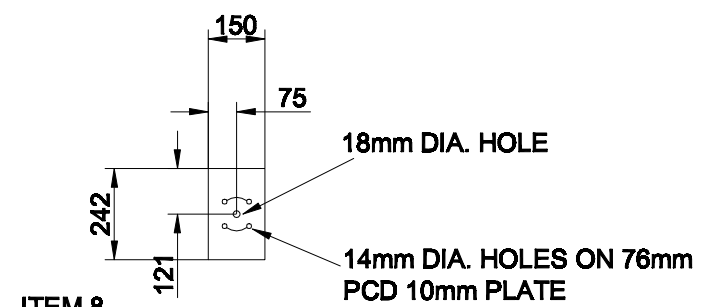
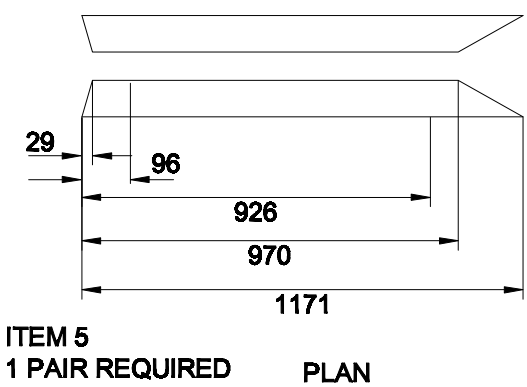


ITEM 1
2 No. REQUIRED

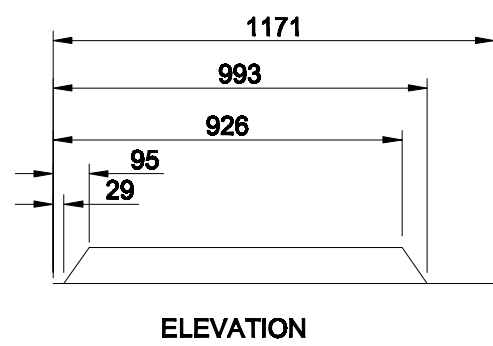

TOP CROSSARM
WELDED ASSEMBLY OF ITEMS 1,2,3,4,& 5
1 No. REQUIRED

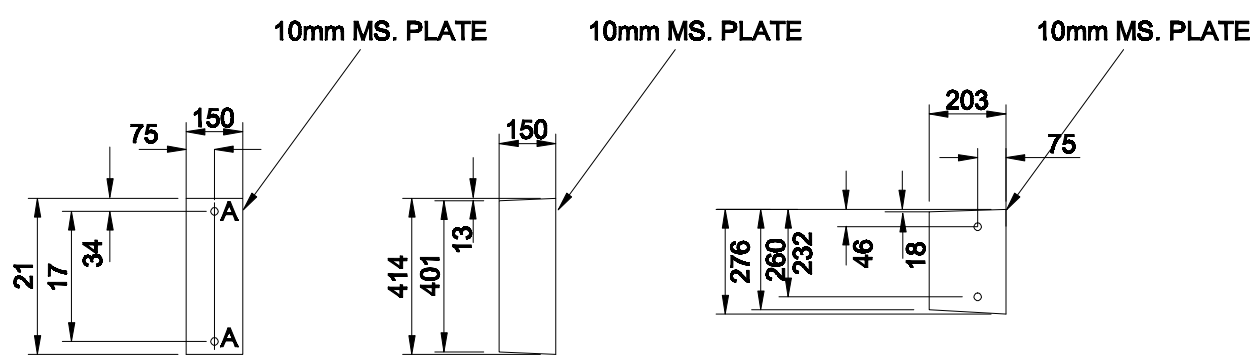

NOTES
HOLES MARKED A 22 DIA
HOLES MARKED B 27 DIA
ITEMS 6 & 7 ARE ASSEMBLED ON SITE WITH THE TOP CROSSARM
ALL STEELWORK TO BS4848 PART 4 & BS4360 GRADE 43A
GALVANISED TO BS729
ALL WELDS TO BE 6mm FILLET ARE SHOWN THUS

 CE Electric UK		Lloyds Court, 78 Grey Street, Newcastle Upon Tyne, NE1 6AF			
Manufacturer Details		CROSSARM STEELWORK FOR PORTAL TERMINAL SUPPORT CE/C/37 (MI)			
Sheet No. 1	Scale 1:20				
Prepared By Janis.Webb		Type OVERHEAD			
		STANDARDS			
Revised 17/05/07	Grid Reference	Ref No.	C948366	Historic Drg.No.	Y204L0904
Date Issued 17/05/07	Checked By	Revision	B	Notes	