



ITEM 1

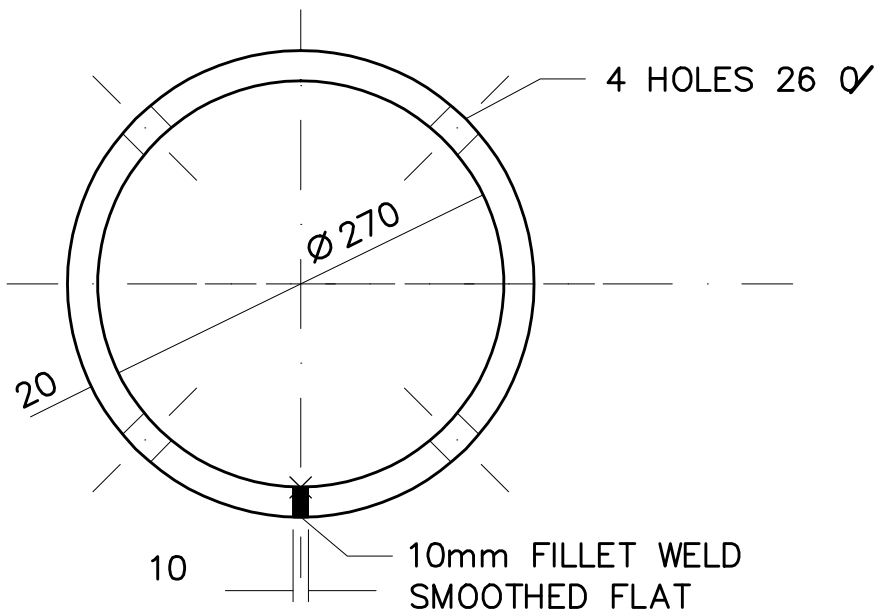


ELEVATION

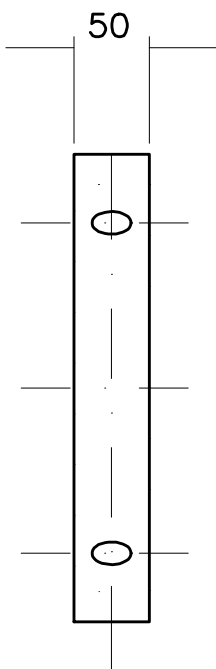


SIDE ELEVATION

ITEM 2

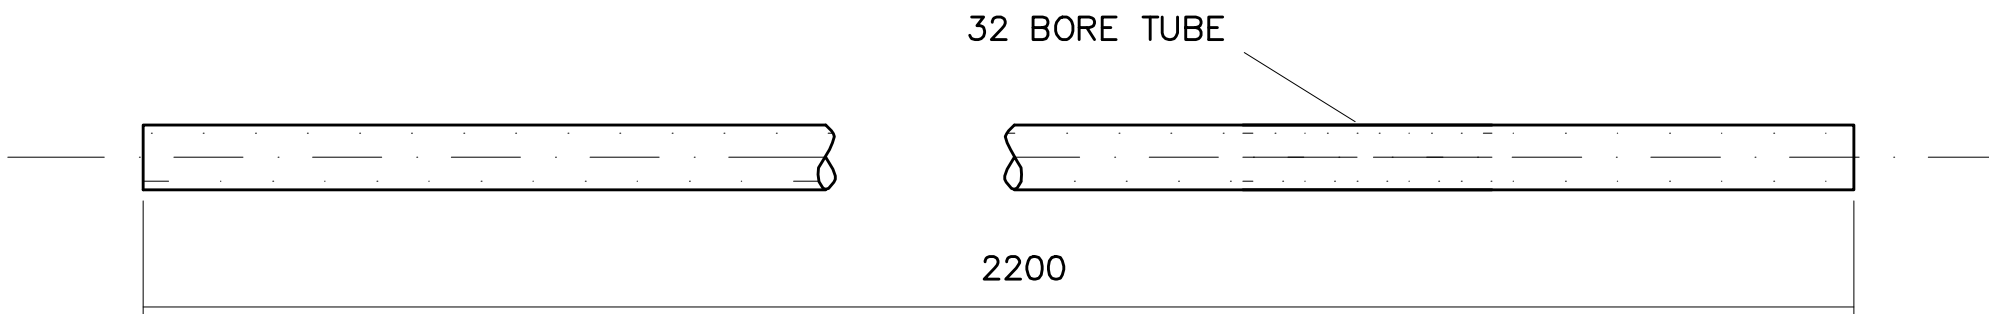


PLAN


ITEM 3

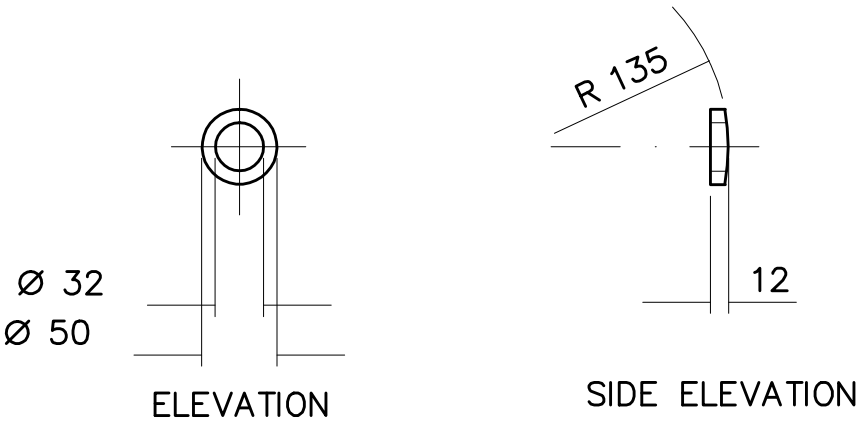

ITEM 4
25 mm MS ROD COMPLETE
WITH TWO NUTS AND TWO
WASHERS

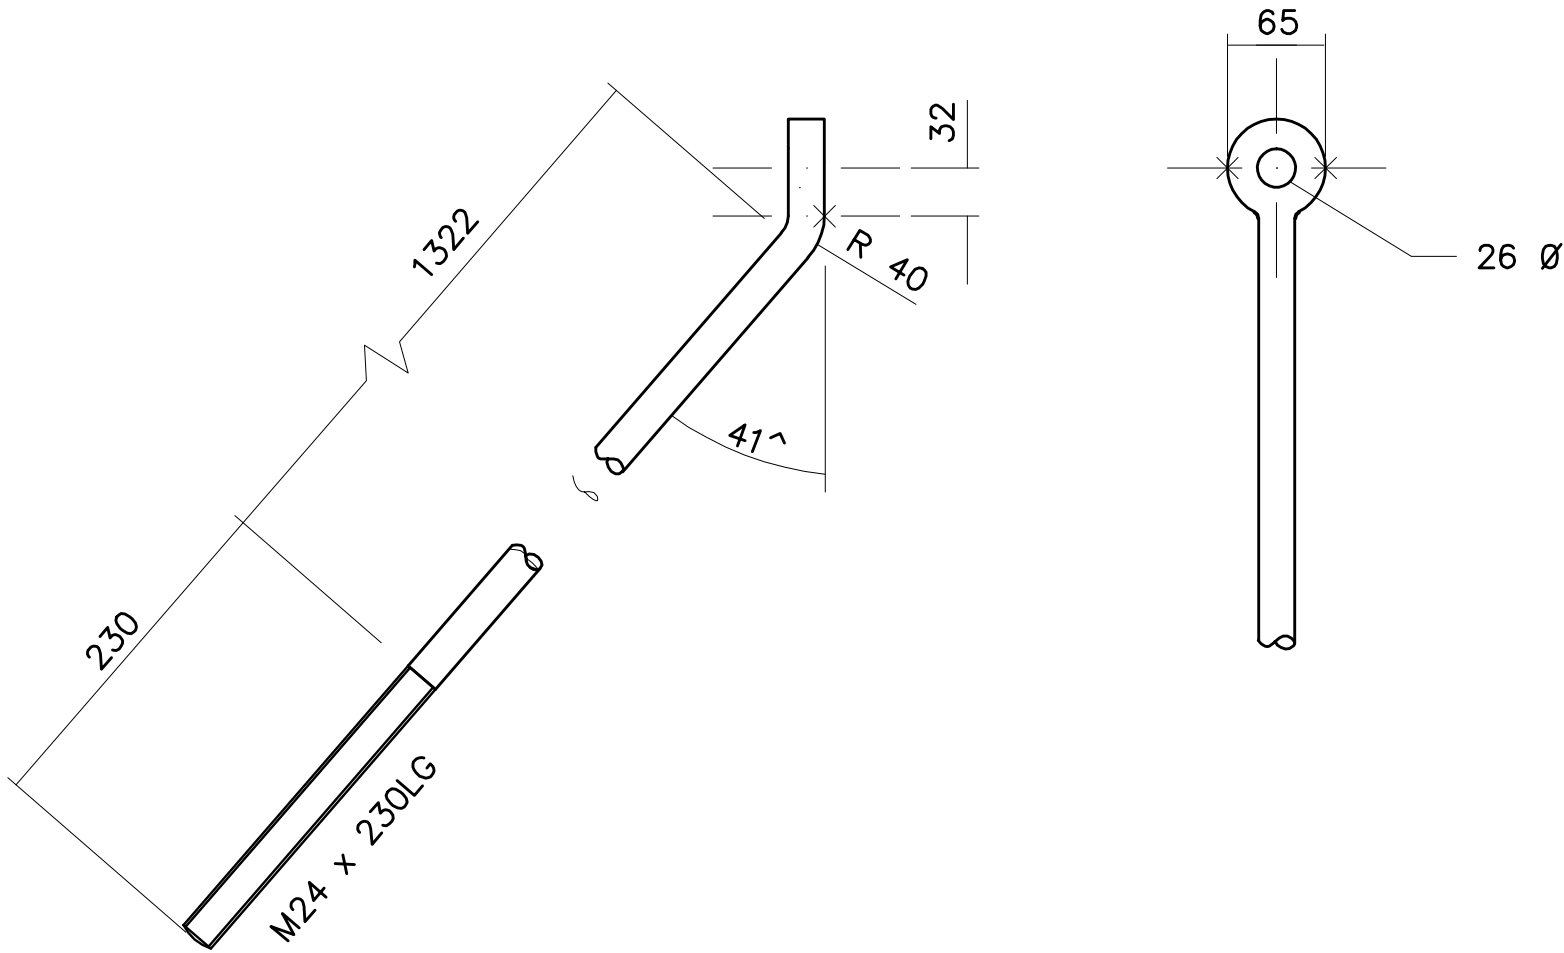

ITEM 5
25mm MS ROD COMPLETE
WITH TWO NUTS AND FOUR
(75x75x6) WASHERS

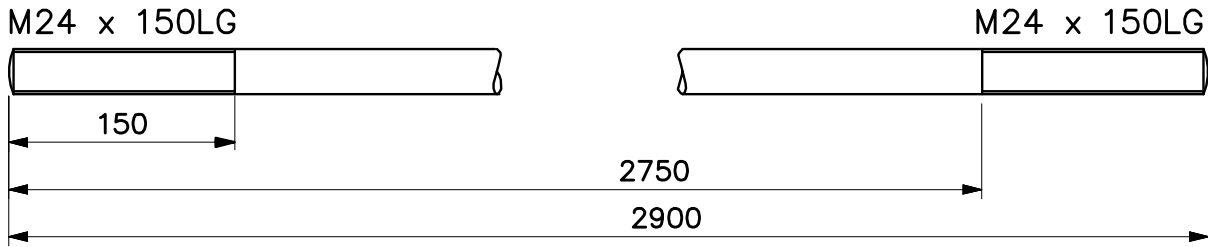

MATERIALS
TUBE – SEAMLESS STEEL ,
HEAVY CLASS , TO BS 1387
OTHER COMPONENTS – MILD
STEEL ,TO BS 4360 GRADE 43A
ALL MATERIALS TO BE
GALVANISED TO BS 729
ALL NUT AND ROD THREADS
TO BS 3643

PARTS LIST

	ITEM	1	2	3	4	5
NUMBER	SINGLE BRACING	1	2	4	4	2
REQUIRED	DOUBLE BRACING	2	3	8	8	3

		Lloyds Court, 78 Grey Street, Newcastle Upon Tyne, NE1 6AF				
Manufacturer Details		OVERHEAD LINES POLE BRACINGS CE / C / 37M				
Sheet No.	Scale					
1	N.T.S.	Type OVERHEAD LINES				
Prepared By Janis.Webb	Grid Reference	Ref No.	C948774	Historic Drg.No.	Y204L0905	
Revised 29/05/07	Checked By	Revision	B	Notes		
Date Issued 25/05/07						