


PART No 90a  
2 No REQUIRED

ELEVATION


SIDE ELEVATION

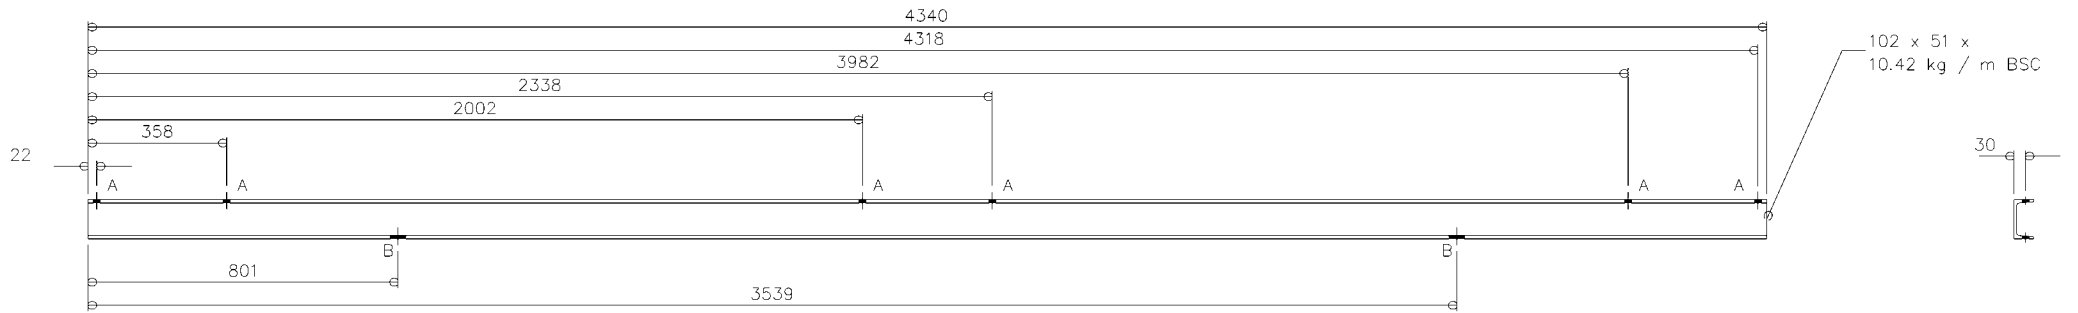

PART No 90b  
2 No REQUIRED

ELEVATION


SIDE ELEVATION

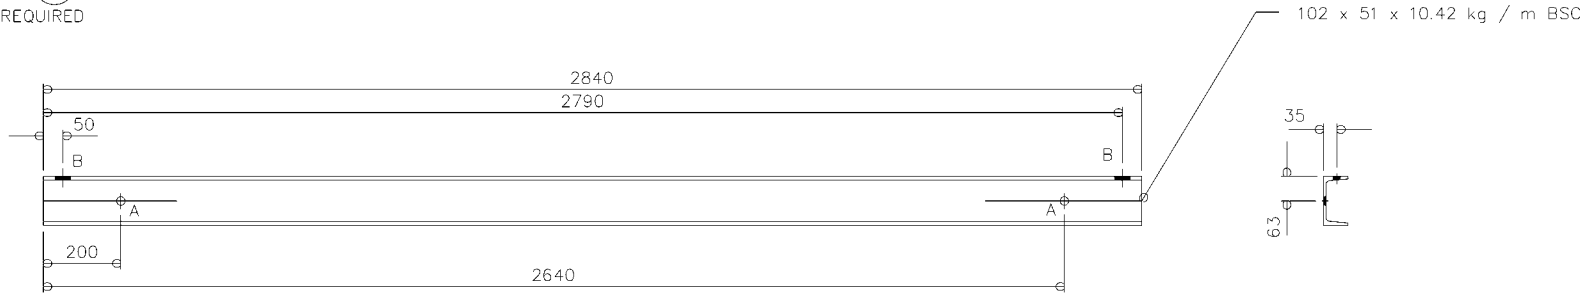

PART No 90c  
1 No REQUIRED

ELEVATION



SIDE ELEVATION

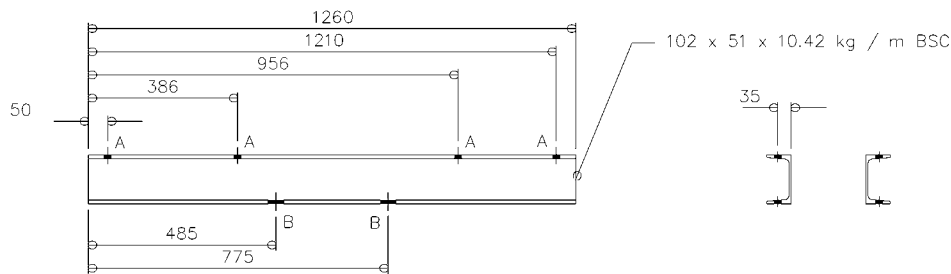


PART No 90d  
1 PAIR REQUIRED

ELEVATION


SIDE ELEVATION

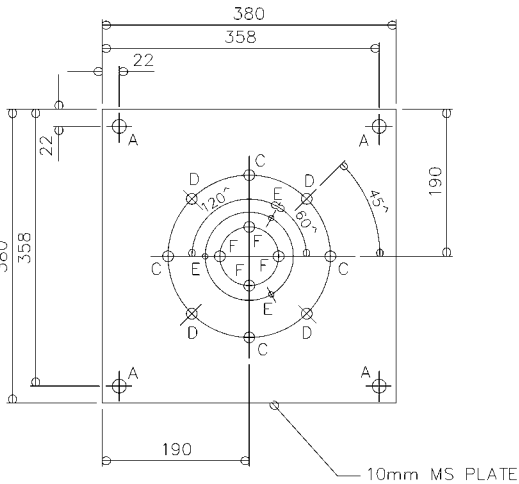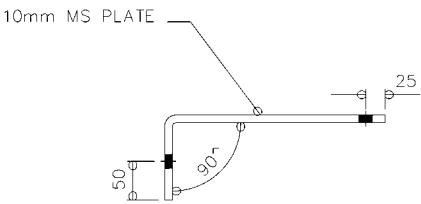

PART No 90e  
3 No REQUIRED  
SCALE 1:5

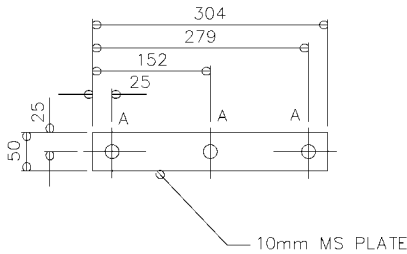

PART No 90f  
3 No REQUIRED  
SCALE 1:5

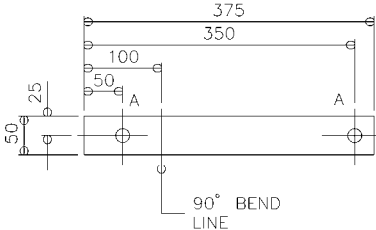

PART No 90g  
6 No REQUIRED  
SCALE 1:5

ELEVATION

PLAN

NOTES  
HOLES MARKED "A" Ø 22  
SLOTS MARKED "B" 40 x 22  
HOLES MARKED "C" Ø 18 ON 210 PCD  
HOLES MARKED "D" Ø 18 ON 210 PCD  
HOLES MARKED "E" Ø 7 ON 114PCD  
HOLES MARKED "F" Ø 14 ON 76 PCD

ALL STEELWORK TO BE IN ACCORDANCE WITH BS4360  
GRADE 43A AND BS4 PART 1  
GALVANISED IN ACCORDANCE WITH BS729

|                           |                |                                                                                                  |                     |
|---------------------------|----------------|--------------------------------------------------------------------------------------------------|---------------------|
| CE Electric UK            |                | Lloyds Court, 78 Grey Street, Newcastle Upon Tyne, NE1 6AF                                       |                     |
| Manufacturer Details      |                | OVERHEAD LINES                                                                                   |                     |
| Sheet No. 1               | Scale AS SHOWN | STEELWORK DETAIL FOR 33KV SEALING<br>END PLATFORM WITH SURGE DIVERSERS<br>CE / C / 37M STRUCTURE |                     |
| Prepared By<br>Janis Webb | Grid Reference | Type<br>OVERHEAD                                                                                 | LINES               |
| Revised<br>29/05/07       | Checked By     | Ref No.<br>C948777                                                                               | Historic<br>Drg.No. |
| Date Issued<br>25/05/07   |                | Revision                                                                                         | Notes               |
|                           |                |                                                                                                  | Y204L0907           |