




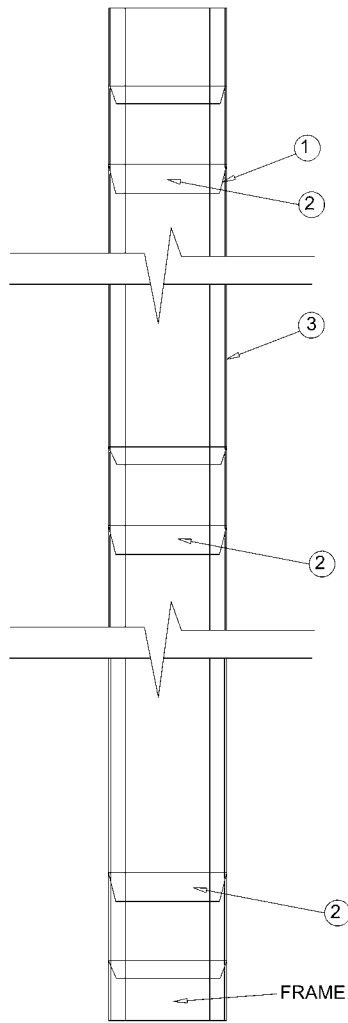


ELEVATION

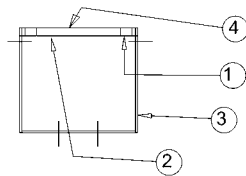

PLAN

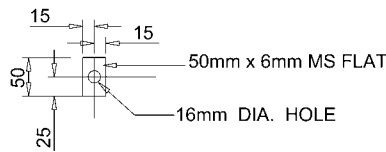


DETAIL ①
6 No REQUIRED
1:5

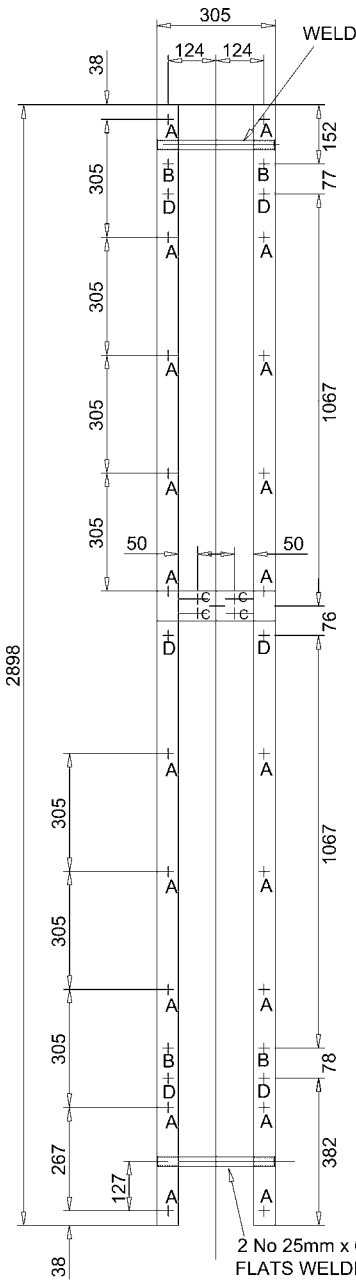


ELEVATION

FRAME

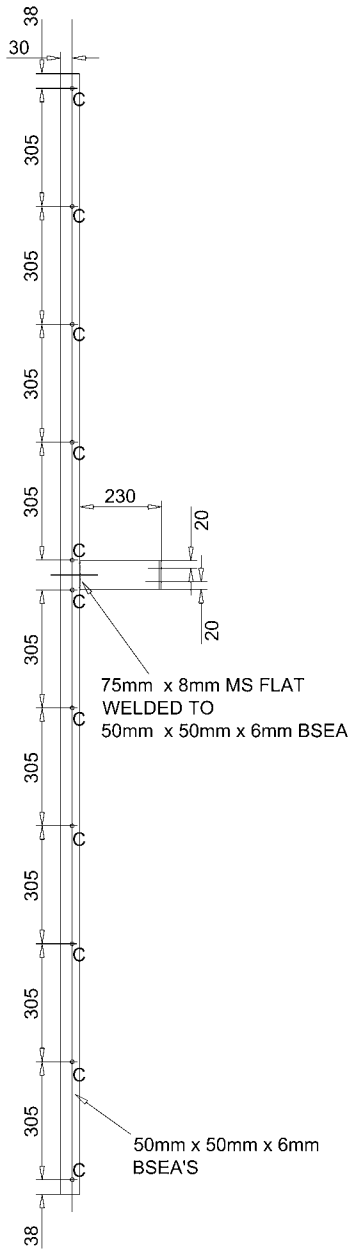


SIDE ELEVATION

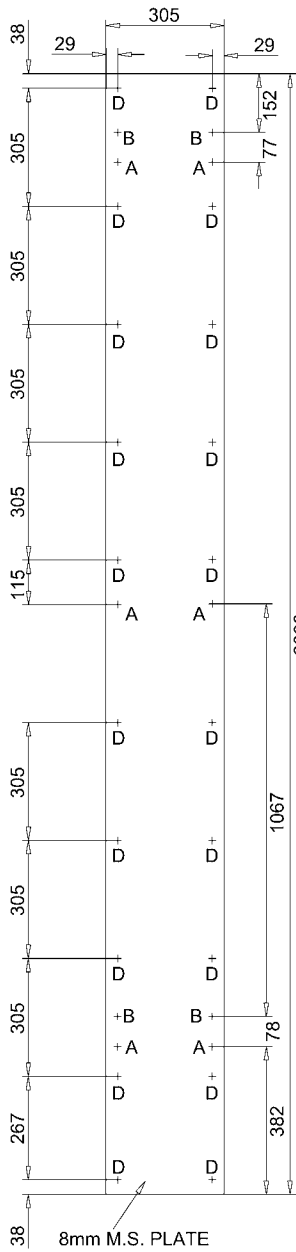


BACK PLATE
DETAIL ④


MATERIAL - 6mm MS PLATE

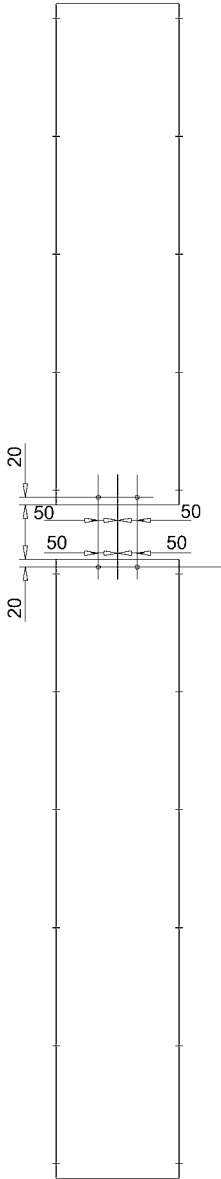

ELEVATION

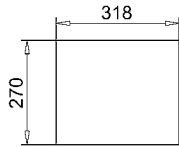


PLAN
DETAIL ③

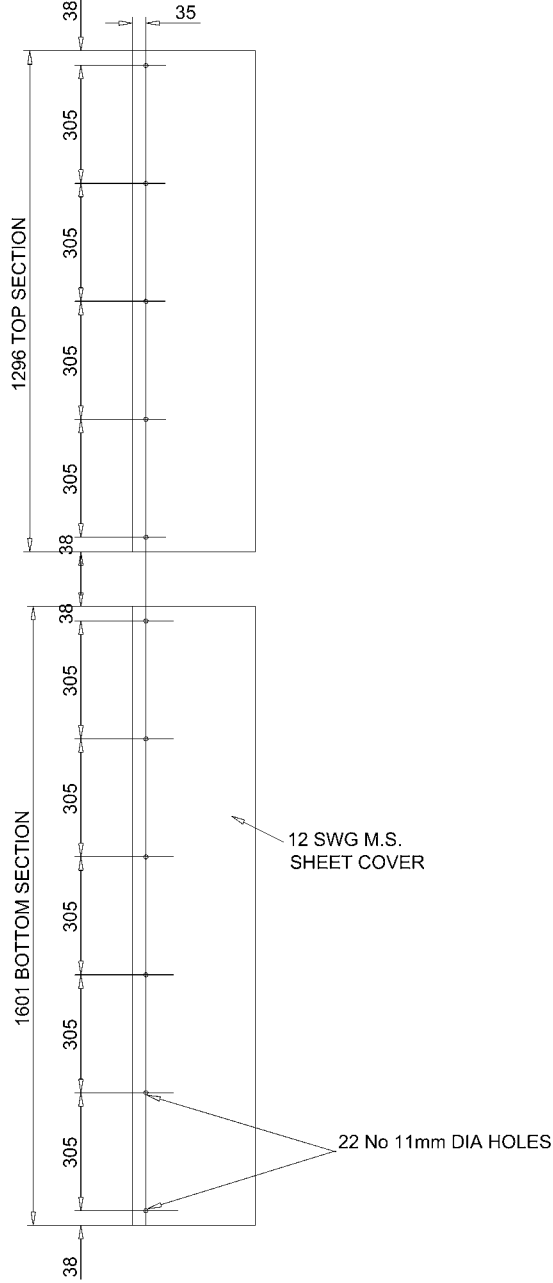

SIDE ELEVATION

MATERIALS

ALL STEELWORK TO BS4848 PART 4 AND BS 4360 GRADE 43A
BOLTS TO BS4190 GRADE 4.6 THREADED ISO COARSE
ALL GALVANISED TO BS729

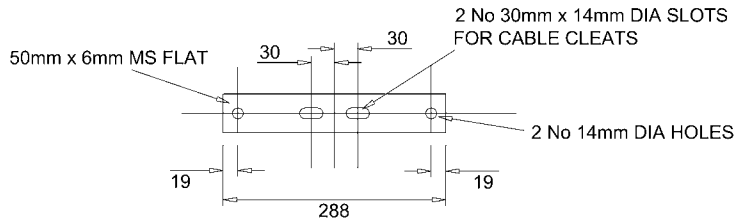

DETAIL ②
3 No REQUIRED
1:5

HOLES MARKED 'A' 26 No DRILLED 14mm DIA
HOLES MARKED 'B' 4 No DRILLED 16mm DIA
HOLES MARKED 'C' 26 No DRILLED AND TAPPED FOR 10mm DIA SET SCREWS
HOLES MARKED 'D' 26 No DRILLED AND TAPPED FOR 12mm DIA SET SCREWS

BOLT LIST			
No REQUIRED	DIA	DESCRIPTION	REMARKS
26	M10	SET SCREW 10mm LONG	COVER / FRAME
20	M12	SET SCREW 12mm LONG	BACK PLATE / FRAME
4	M16	25mm LONG THREADED 13mm WITH NUT AND WASHER	CABLE GUARD / TOP AND BOTTOM BSC
6	M12	25mm LONG THREADED 19mm	CABLE CLEAT SUPPORT / FRAME

CE Electric UK		Lloyds Court, 78 Grey Street, Newcastle Upon Tyne, NE1 6AF	
Manufacturer Details		66KV AND 33KV CABLE GUARD	
Sheet No. 1	Scale 1:10		
Prepared By Janis Webb	Type OVERHEAD	LINES	
Revised 15/05/07	Grid Reference	Ref No. C948290	Historic Drg. No. Y204L0911
Date Issued 10/05/07	Checked By	Revision B	Notes