




ARRANGEMENT OF ABSD ON SECTION POLE TO Y003X1308

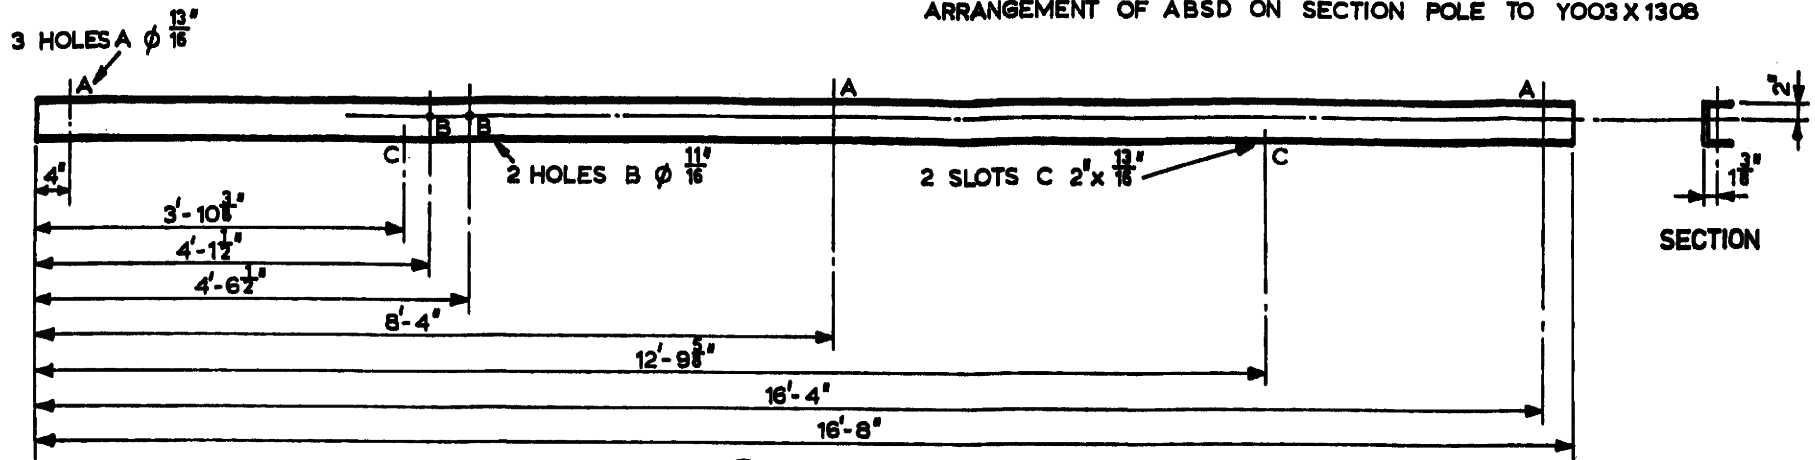

ITEM ① - ELEVATION

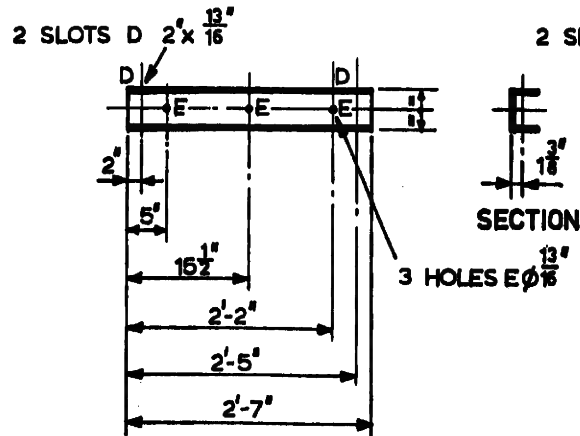

ELEVATION
ITEM ②

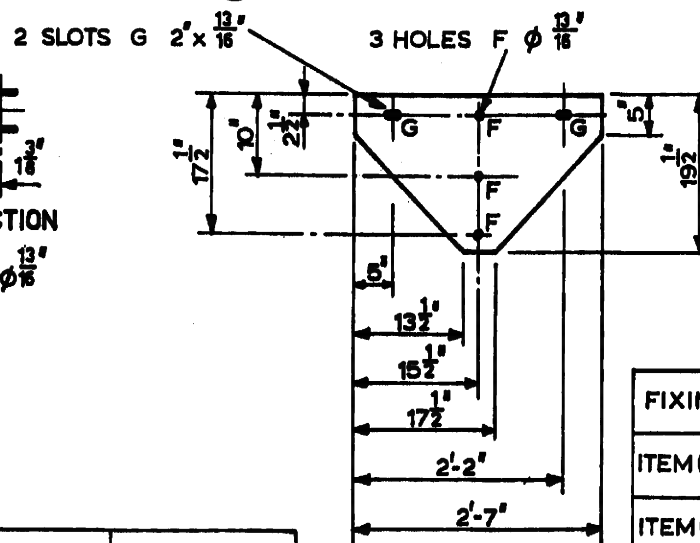

ELEVATION
ITEM ③

ALL STEELWORK TO BE IN ACCORDANCE WITH
BS 4360 GRADE 43A AND BS 4 PART 1
GALVANISED IN ACCORDANCE WITH BS 729
ALL BOLTS TO BS 916 SCREWED BSW AND
GALVANISED IN ACCORDANCE WITH BS 729

BOLT LIST

FIXING BETWEEN	WASHERS	SIZE	No REQUIRED
ITEM ① AND ITEM ②	8 TAPER	2 1/2' x 3/4' DIA	4
ITEM ② AND ITEM ③	8 ROUND	2' x 1/2' DIA	4
ITEM ③ AND WOOD POLES	6 CURVED 6 ROUND	12' x 3/4' DIA	6

ITEM	DESCRIPTION	MATERIAL	No REQUIRED
①	CROSS CHANNEL	127 x 64 x 14.9 kg/m BS CHANNEL	1-AS SHOWN 1-LESS HOLES 'B'
②	SUPPORT	127 x 64 x 14.9 kg/m BS CHANNEL	2
③	GUSSET PLATE	1/2" THK. MS PLATE	2

DRAWING WAS FORMERLY Y003X3421

drawn M.W. 17.7.97	OVERHEAD LINES CE/C/37	
traced J.E.F. 17.7.97	33/66kV ROTATING TYPE AIR BREAK SWITCH DISCONNECTOR SUPPORT STEELWORK DETAILS	
checked -	date -	original scale 1/4" TO 1'
approved -	date -	Y204L0913

YE
DL
RELENTLESSLY
AT YOUR SERVICE