



ITEM No 1
1 No REQUIRED

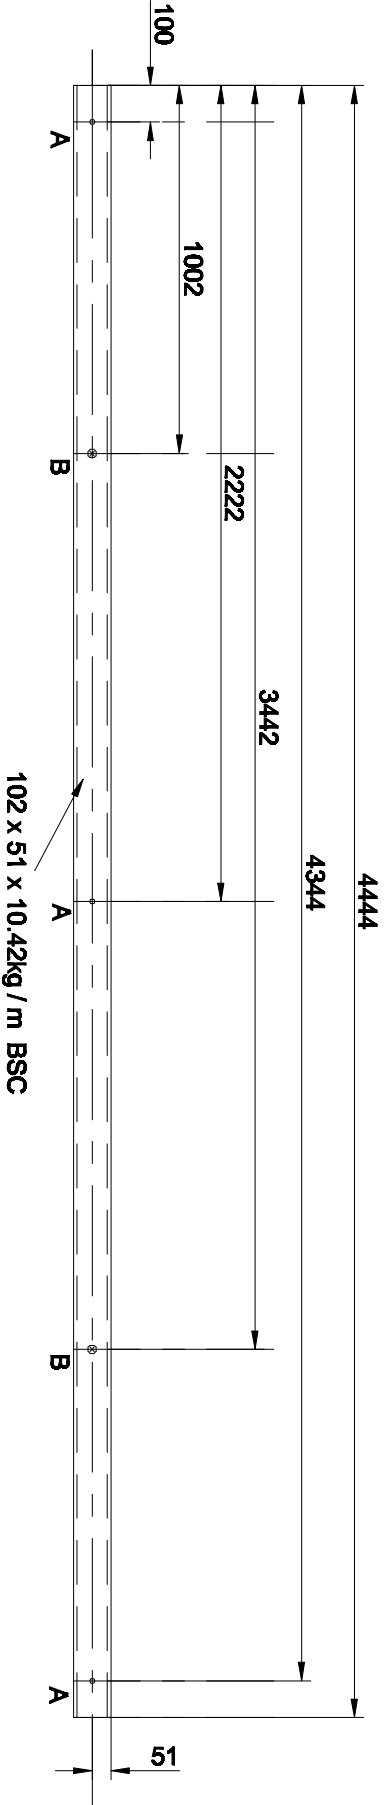

ITEM No 2
1 No REQUIRED

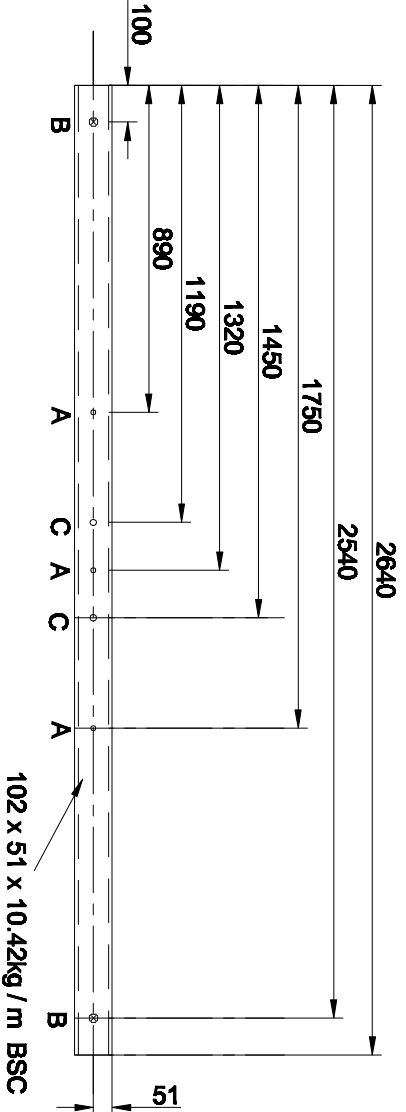

ITEM No 3
3 OFF REQUIRED

NOTES

1. HOLES MARKED 'A' 14 mm DIA
2. SLOTS MARKED 'B' 22 x 23mm CENTRES
3. HOLES MARKED 'C' 18mm DIA
4. ALL STEELWORK TO BS 4848 PART 4 & BS 4360 GRADE 43A
5. ALL GALVANISED IN ACCORDANCE WITH BS729

CE Electric UK Manufacturer Details			Lloyds Court, 78 Grey Street, Newcastle Upon Tyne, NE1 6AF		
CABLE SUPPORT STEELWORK FOR 33 AND 66KV POLYMERIC CABLE TERMINATION CE / C / 37 - CE / OM / DC1					
Sheet No. 1		Scale 1:20		Type OVERHEAD	
Prepared By Jantis Webb				LINES	
Revised 15/05/07	Grid Reference		Ref No. C948286	Historic Drg.No.	Y204L0917
Date Issued 10/05/07	Checked By		Revision D	Notes	

ALL DIMENSIONS SHOWN ARE IN MILLIMETRES UNLESS OTHERWISE STATED