



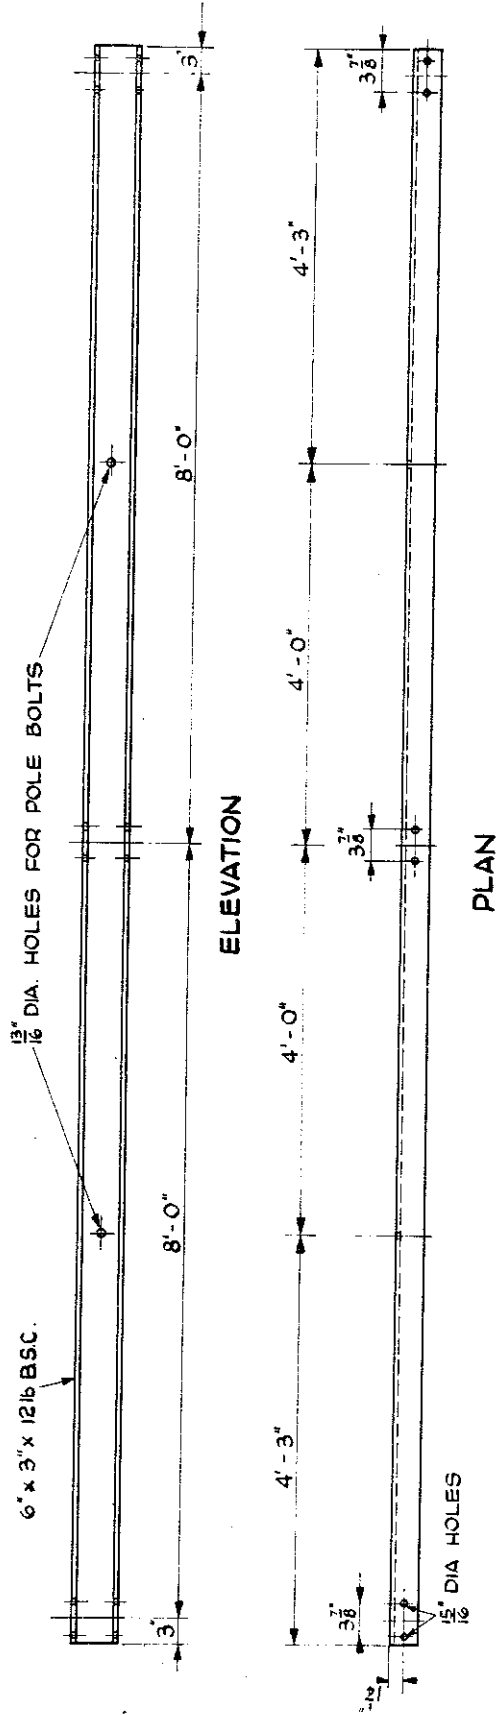


MATERIALS
ALL MATERIALS TO BS 4 PART 1 & BS 4360 GRADE 43A
GALVANISED TO BS 729
BOLTS TO BS 916 THREADED B.S. WHITWORTH
WASHERS - GALVANISED MALLEABLE IRON TO
BS 1320 (FIG. 38).

BOLTS	
2 N° 2	2" DIA X 10" LONG SCREWED COMPLETE WITH NUT
2 N° 2	2 1/2" x 2 1/2" x 1/4" CURVED WASHERS

CROSSARM POLE	
2 N° 2	2" DIA X 10" LONG SCREWED COMPLETE WITH NUT
2 N° 2	2 1/2" x 2 1/2" x 1/4" CURVED WASHERS

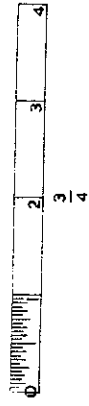

drawn	M.G.B.	OVERHEAD LINES SPEC C/C/37			
traced	checked				
date 21 3 69		CROSSARM STEELWORK			
scale 3/4" = 1'		INTERMEDIATE SUPPORT			
A	B	C	D	Yorkshire Electricity Board	Y003 X 3310

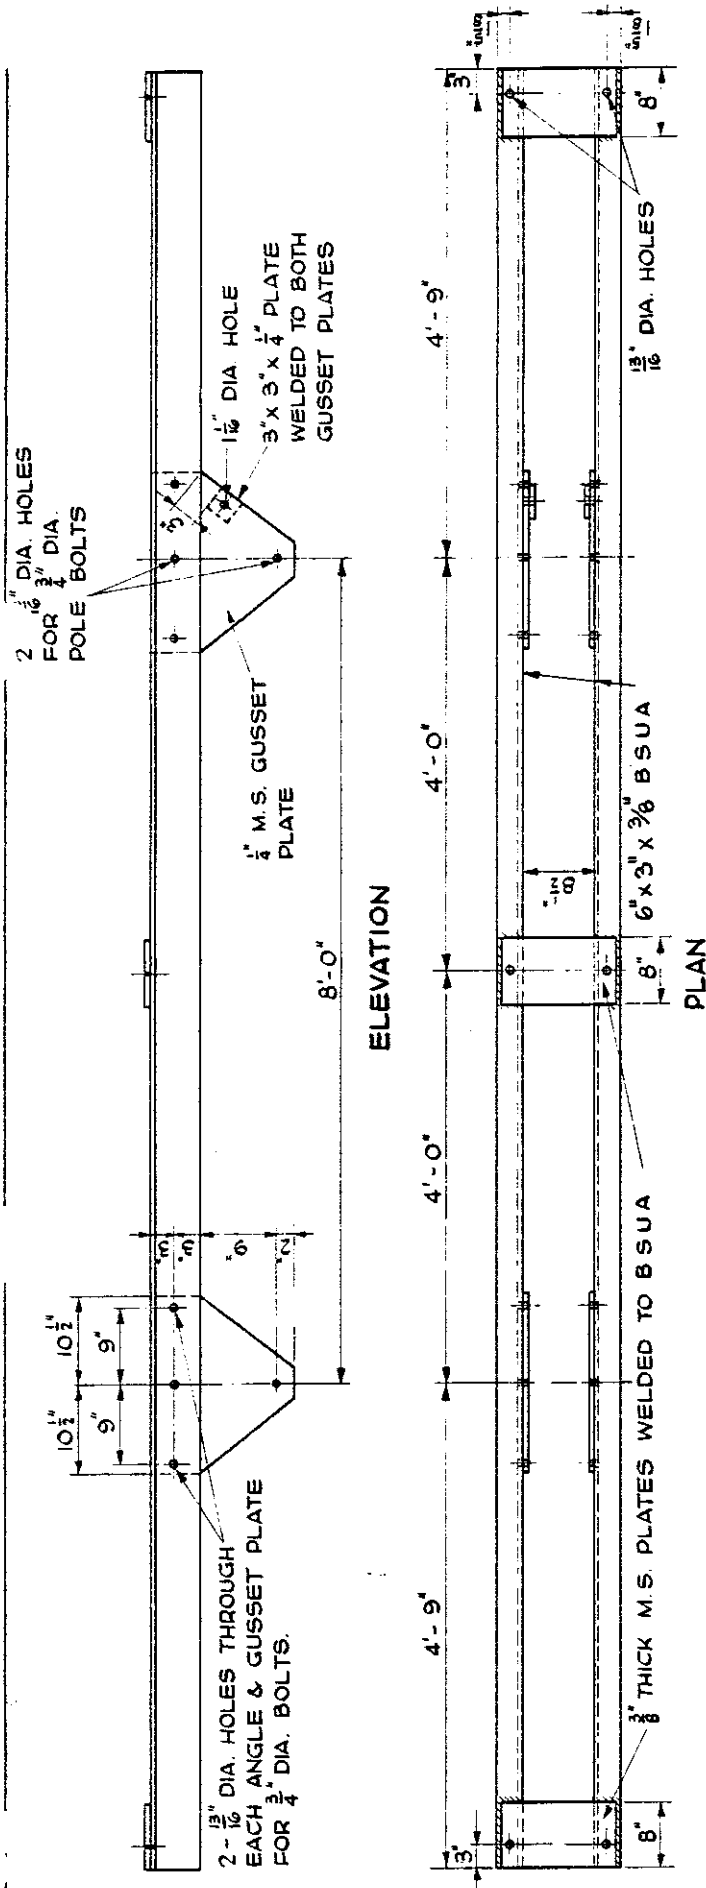

BOLTS

ANGLE SUPPORT (UP TO 10°)

	CROSSARM/ GUSSET
8 NO 3/4" DIA. X 1 1/2" LONG SCREWED 1" COMPLETE WITH NUT	
4 NO 3/4" DIA. 11" LONG SCREWED 3" COMPLETE WITH NUT	CROSSARM / POLE

SECTION SUPPORT (UP TO 10°)

	CROSSARM / POLE
2 NO 3/4" DIA. X 11" LONG SCREWED 3" COMPLETE WITH NUT	

MATERIALS

ALL STEELWORK TO BS4848 PART 4 & BS4360 GRADE 43A GALVANISED TO BS.729.

BOLTS TO B.S. 916 THREADED B.S. WHITWORTH

NOTES:-

FOR ANGLES 10° - 60° SEE Y003 X 3312

GUSSET PLATES TO BE SUPPLIED FOR ANGLE POSITIONS ONLY

drawn	M G B
checked	6
date	19. 3. 69
scale	1/4" = 1'

OVERHEAD LINES SPEC CE/C/37

CROSSARM STEELWORK

SECTION SUPPORT (& ANGLES UP TO 10°)

A GUSSET REINFORCING R


C

D


Yorkshire Electricity Board Y003 X 3311

13/16" DIA HOLES THROUGH EACH
ANGLE & GUSSET PLATE FOR
3/4" DIA. BOLTS.

2-13/16" DIA. HOLES FOR
3/4" DIA. POLE BOLTS

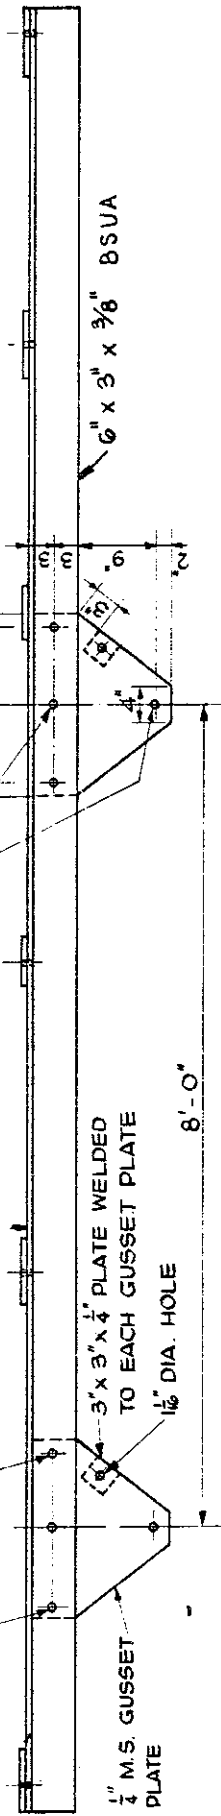

ELEVATION

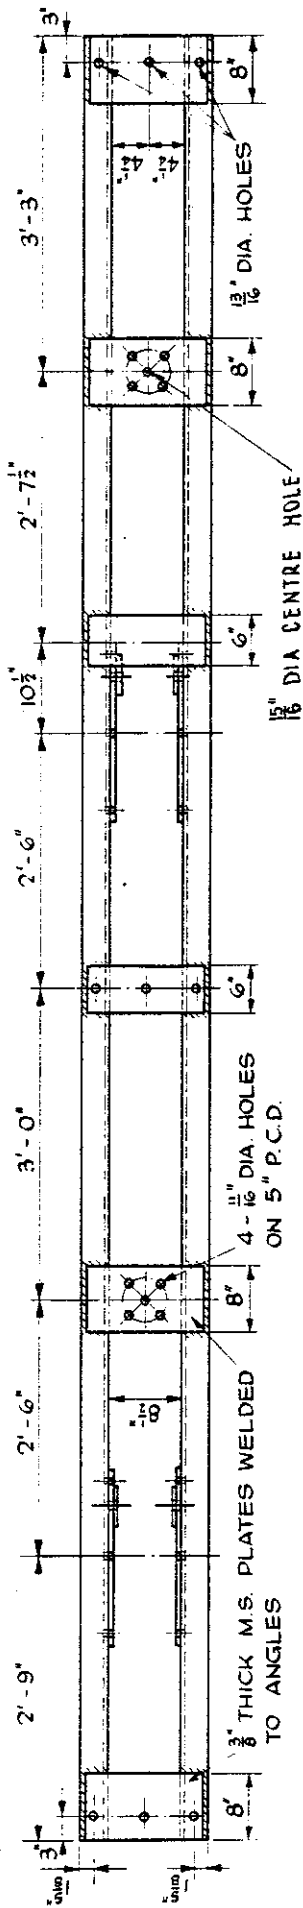

PLAN

BOLTS

8 N°	3/4" DIA. x 12" LONG SCREWED 1" COMPLETE WITH NUT	CROSSARM/ GUSSET
4 N°	3/4" DIA. x 11" LONG SCREWED 3" COMPLETE WITH NUT	CROSSARM/POLE

MATERIALS

ALL STEELWORK TO BS4848 PART4 & BS 4360 GRADE 43A
GALVANISED TO B.S.729.

BOLTS TO B.S.916 THREADED B.S. WHITWORTH

NOTE

FOR ANGLES UP TO 10° SEE Y003 X 3311

drawn	M.G.B.
checked	10
date	20.3.69
scale	3/4" = 1'

OVERHEAD LINES SPEC CE/C/37

CROSSARM STEELWORK

ANGLE SUPPORT (ANGLES 10°- 60°)

DRG N° FOR ANGLES
A11P TO 10° AMENDED

GUSSET REINFORCING
B PLATES SHOWN

D

Yorkshire Electricity Board

Y003 X 3312