


INTERMEDIATE POLE

SECTION POLE
& ANGLE 0° TO 10°

ANGLE POLE
(ANGLES 10° TO 60°)

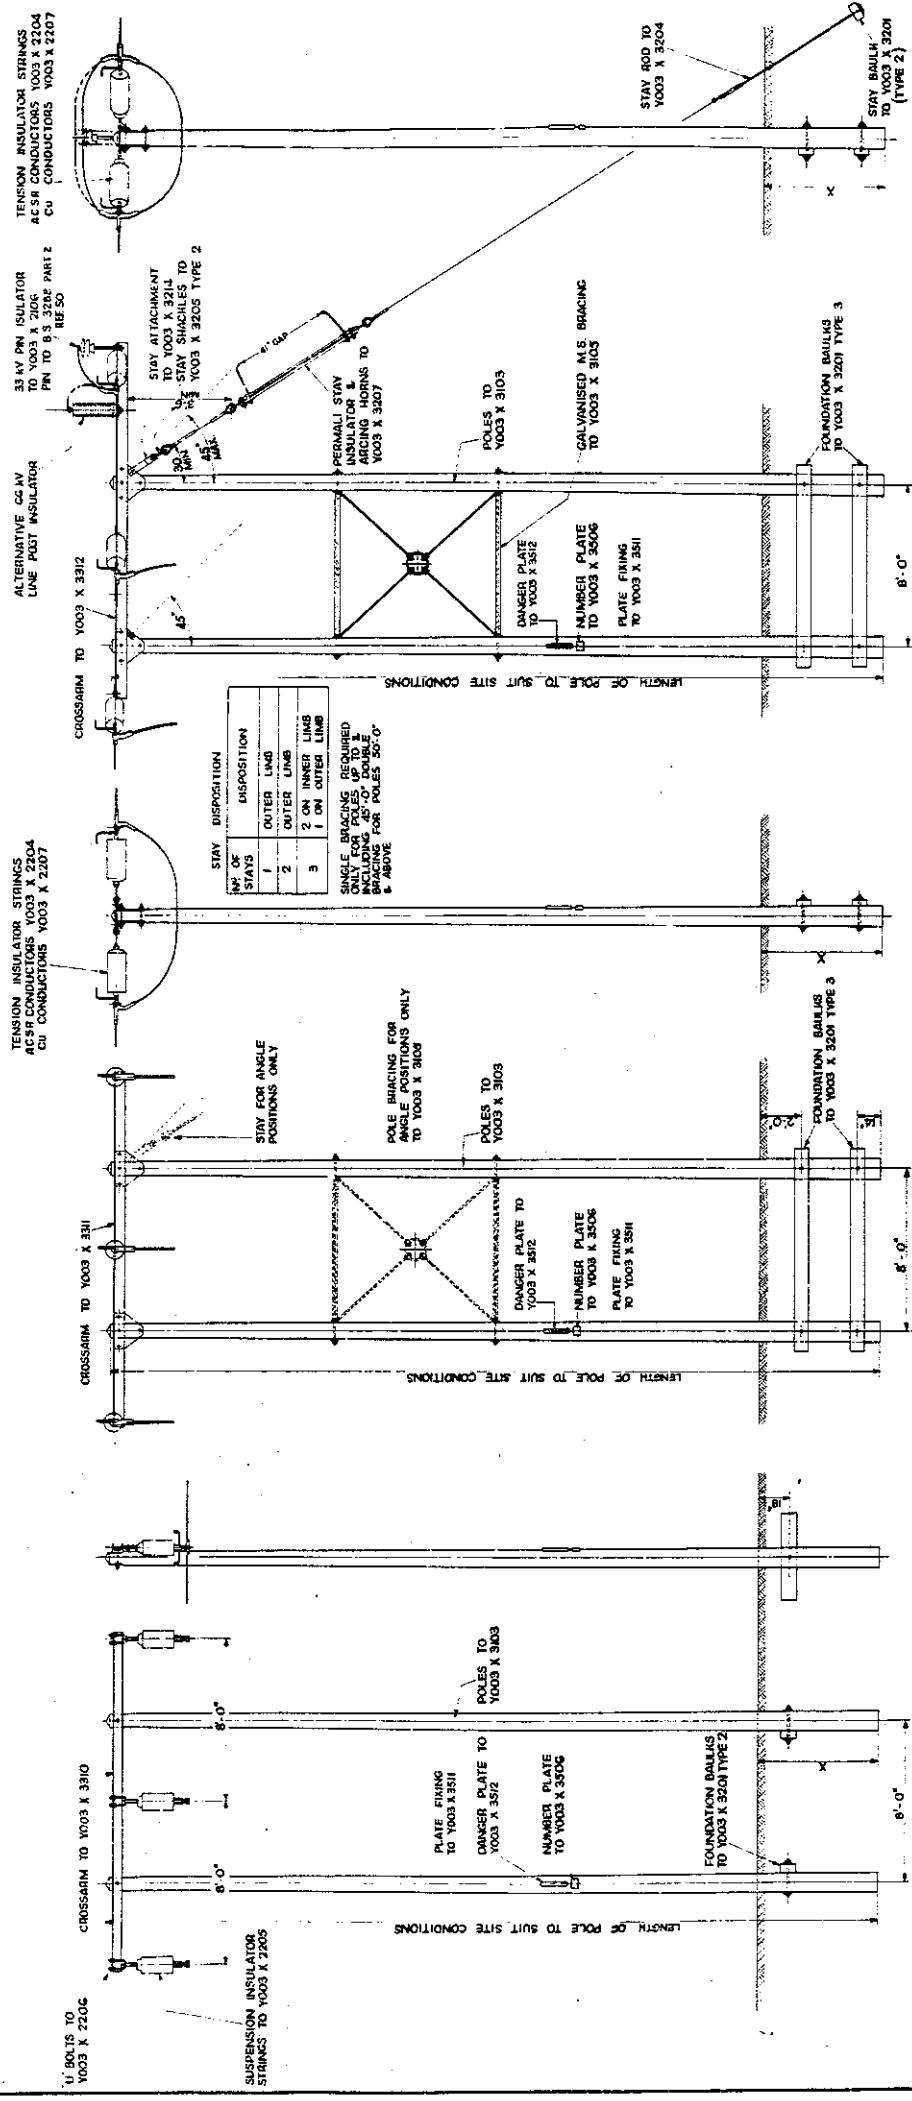

SIDE ELEVATION




FRONT ELEVATION

SIDE ELEVATION

FRONT ELEVATION

SIDE ELEVATION

FRONT ELEVATION

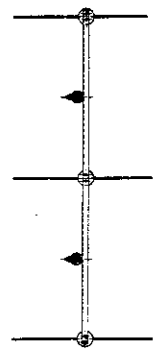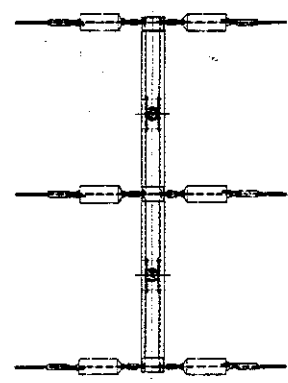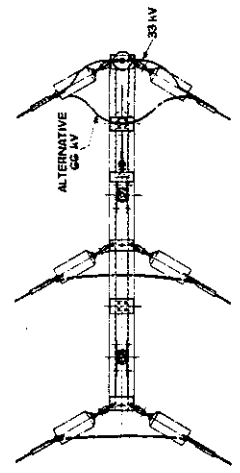

PLAN

PLAN

PLAN

POLE LENGTH IN FEET	DIMENSION X
UP TO 1 INCL 30'-0"	6'-0"
30'-0" TO 40'-0"	6'-6"
40'-0" TO 50'-0"	7'-0"
50'-0" TO 55'-0"	7'-6"
OVER 55'-0"	8'-0"

OVERHEAD LINES SPEC CE/C/37

GENERAL ARRANGEMENT OF INTERMEDIATE SECTION & ANGLE POLES

Scale: 1/4" = 1'

YOO3 X 1103

PLATING DETAIL SHOWN	A	B	C	D	E	F	G	H	I	J	K	L	M	N	O	P	Q	R	S	T	U	V	W	X	Y	Z	
PLATE BRACING & DANGER PLATE DATE OF REVISION: 1970 DESIGNED BY: JMW CHECKED BY: JMW APPROVED BY: JMW																											