


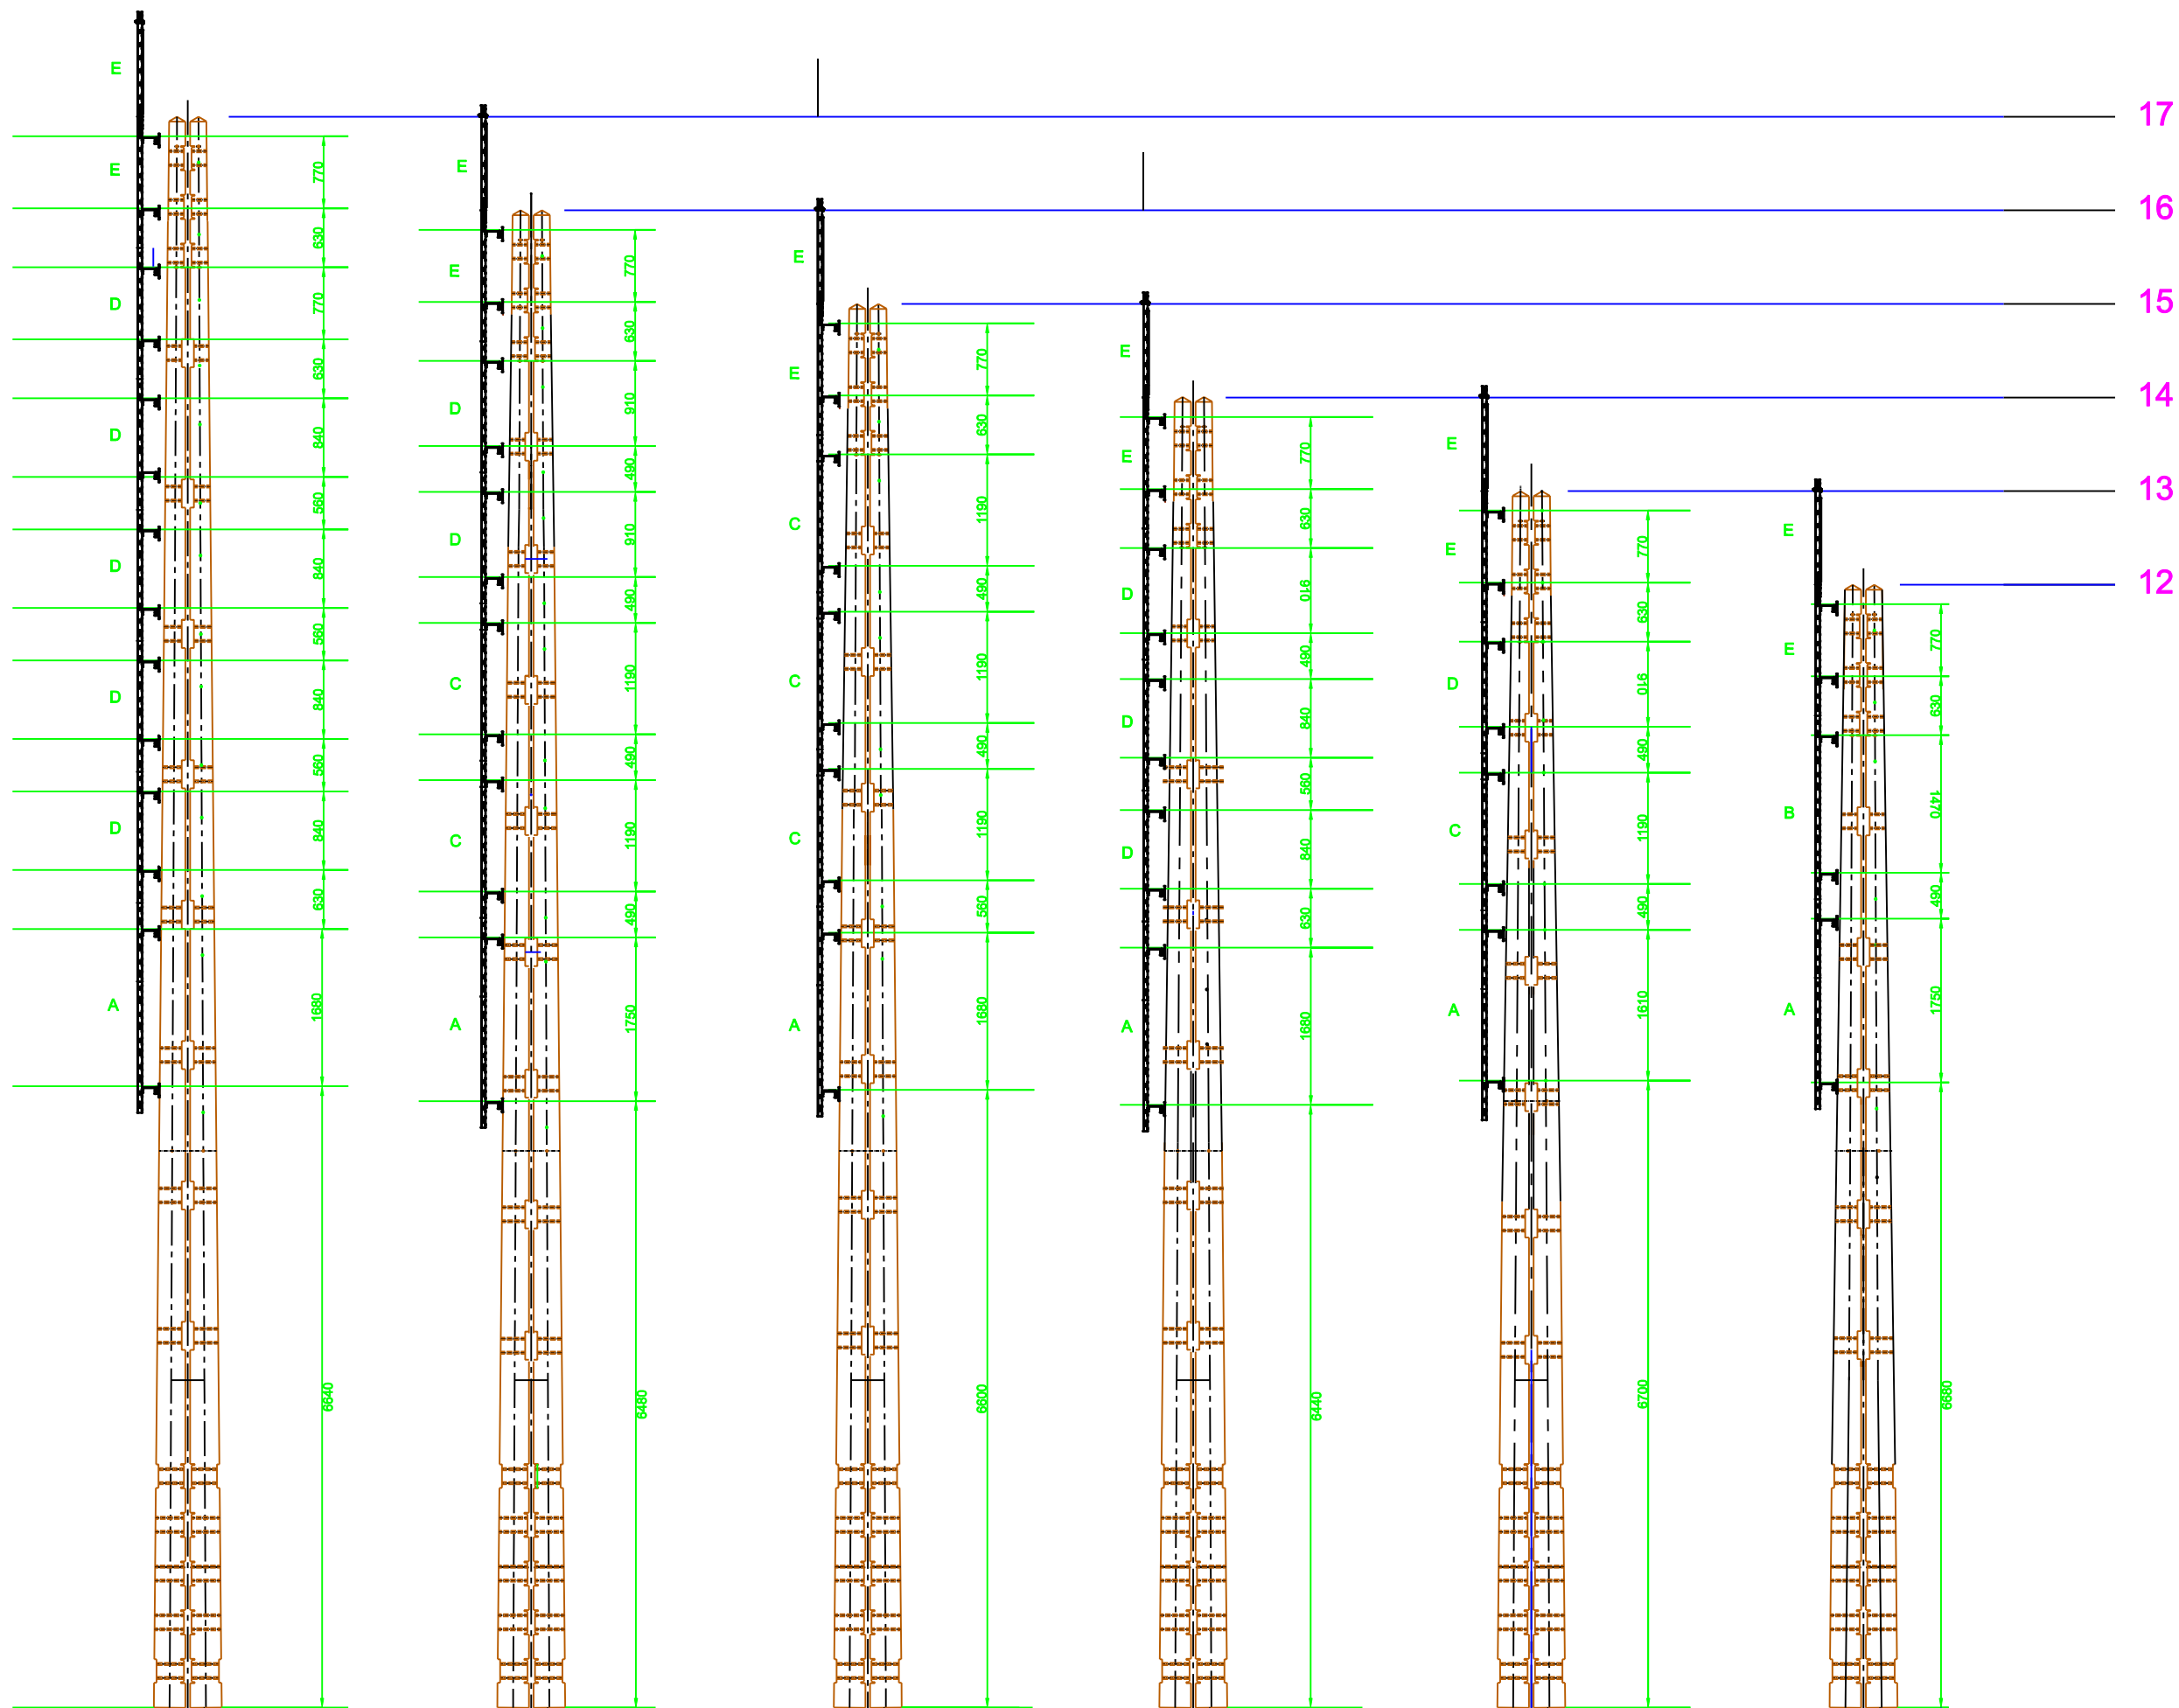

SCALE IS 1:25

A = 2240R
B = 1960
C = 1680
D = 1400
E = Top Plug-In Extension Section

CE Electric UK		Lloyds Court, 76 Grey Street, Newcastle Upon Tyne, NE1 6AF	
Manufacturer Details		ADDITIONAL FABRICATION DETAILS FOR THE ATTACHMENT OF THE HCL CLIMBING ACCESS SYSTEM TO DRG 1091390003 SHEET 2	
Sheet No. 1	Scale	TYPE OVERHEAD	POLES
Prepared By Jodie Webb		Ref No. CS00639	Historic Dwg. No. 1091390008
Revision 100907	Grid Reference	Revision	Notes
Date Issued 03/09/07	Created By G. HARRIS		