



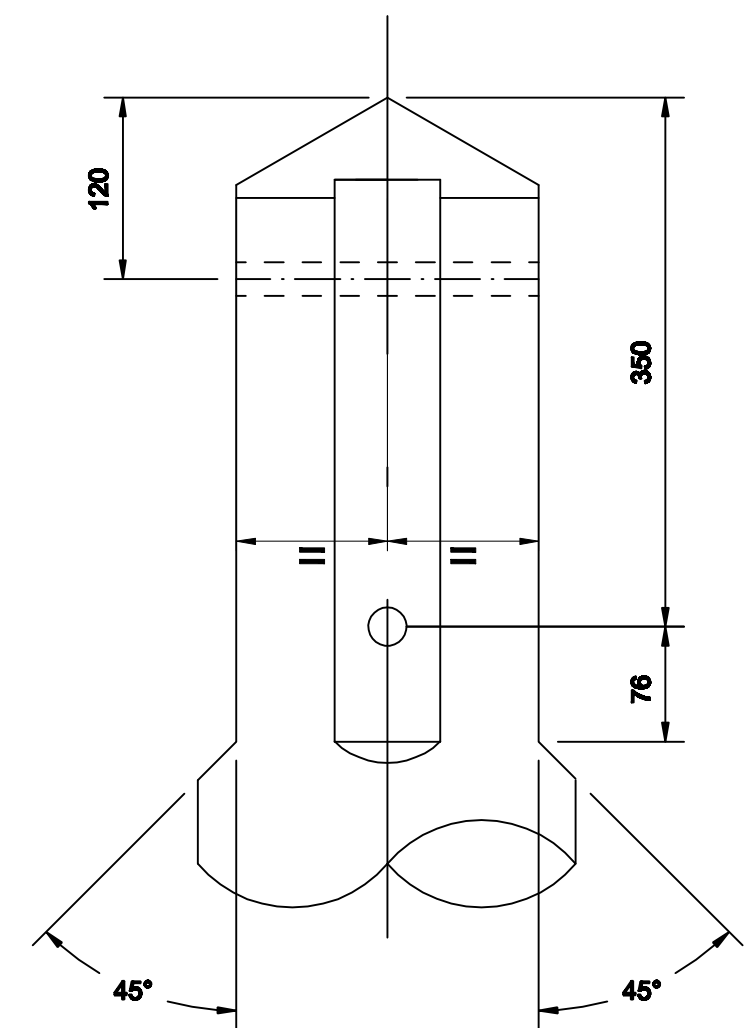

SCALE 1:5

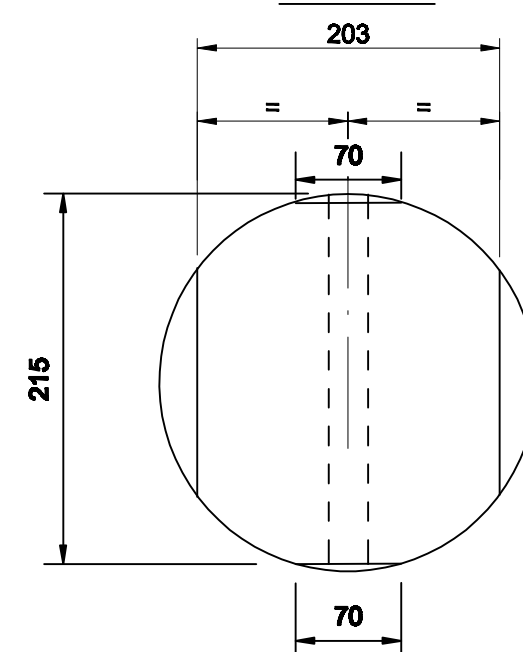

DETAIL 'A'

SCALE 1:5

NOTES

- All dimensions shown are in millimetres unless stated otherwise

 CE Electric UK		Lloyds Court, 78 Grey Street, Newcastle Upon Tyne, NE1 6AF	
Manufacturer Details		132KV SINGLE CIRCUIT OVERHEAD LINES DRILLING, SCARFING AND MARKING FOR TERMINAL 'H' POLE STRUCTURE	
Sheet No. 2	Scale 1:20	Type OVERHEAD STANDARDS	
Prepared By Carolyn.Palmer		Ref No. C949776	
Revised 25/09/07	Grid Reference	Historic Drg. No.	1091390019
Date Issued 03/07/07	Checked By G. HAMMEL	Revision B Notes	