


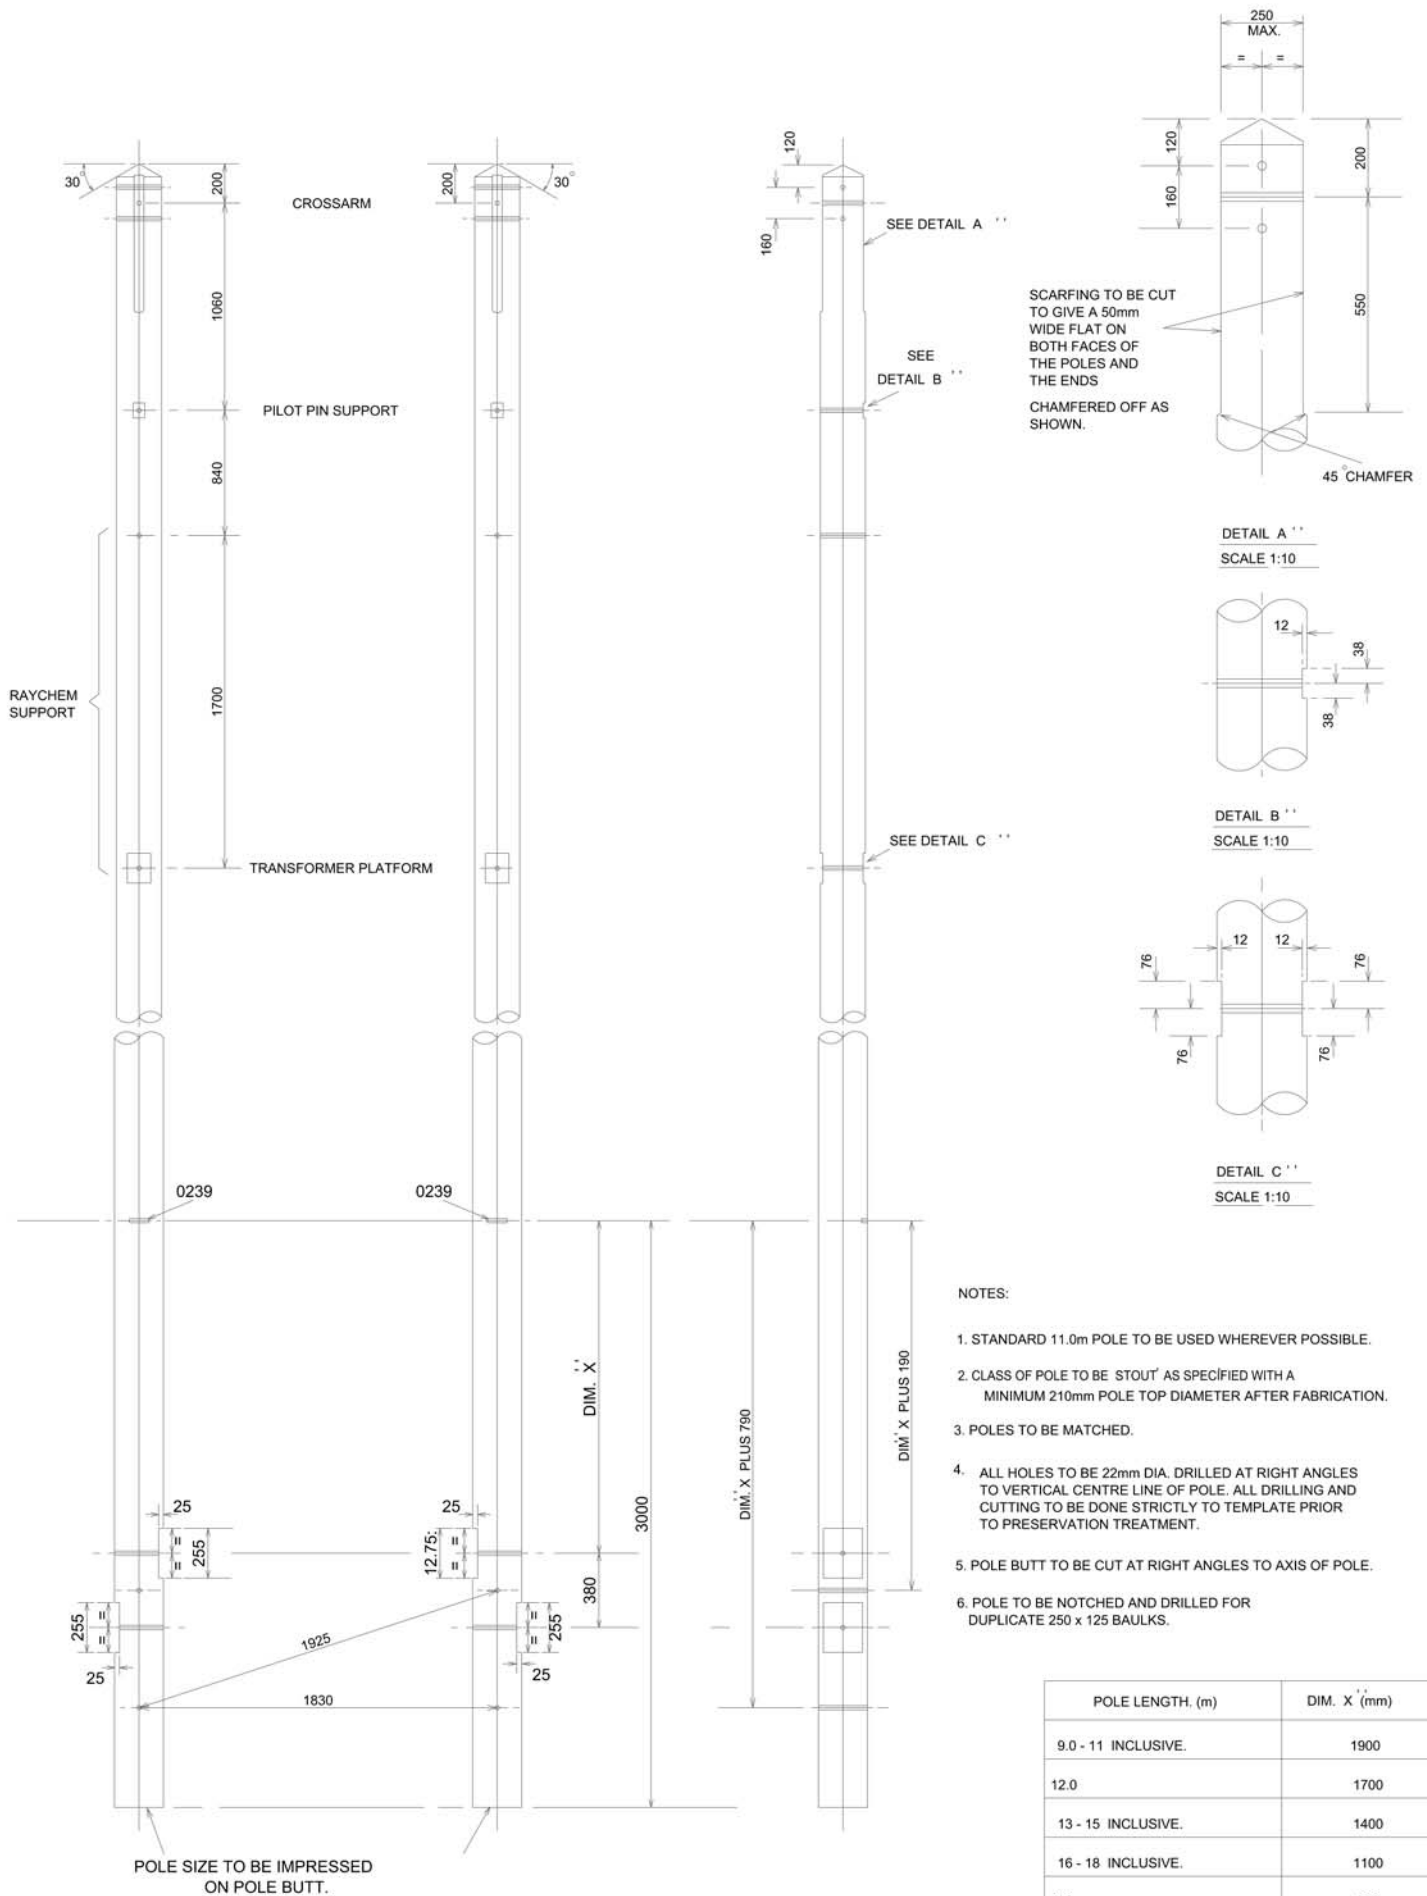

FABRICATION DRAWING FOR USE WITH THE FOLLOWING ARRANGEMENT DRAWINGS:

DRG. No. 1.00.043.4006 SHEET 1.
 DRG. No. 1.00.043.4007 SHEET 1 & 2.
 DRG. No. 1.00.043.4011 SHEET 1.
 DRG. No. 1.00.043.4011 SHEET 6.
 DRG. No. 1.09.108.0860 SHEET 1.
 DRG. No. 1.09.108.0860 SHEET 3.

ALL DIMENSIONS SHOWN ARE IN MILLIMETRES UNLESS OTHERWISE STATED.

		Lloyds Court, 78 Grey Street, Newcastle Upon Tyne, NE1 6AF	
Manufacturer Details		HV OVERHEAD LINES MULTI-FABRICATION 'H' POLE SUITABLE FOR LINE SECTION OR TERMINAL ARRANGEMENT & PLANT RELATED CABLE OR PLATFORM MOUNTED TRANSFORMER	
Sheet No. 2	Scale 1:20	Type ESI	ESI
Prepared By Jonis Webb	Grid Reference	Ref No. C147654	Historic Drg. No. 1000434002
Revised 24/04/06 Date Issued 23/02/05	Checked By G HAMMEL	Revision C	Notes