

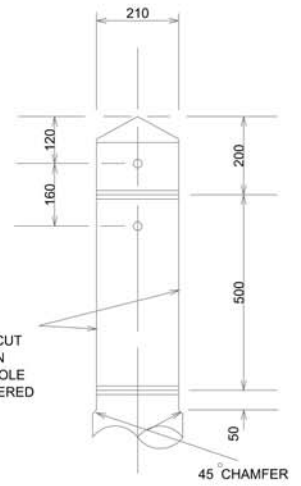
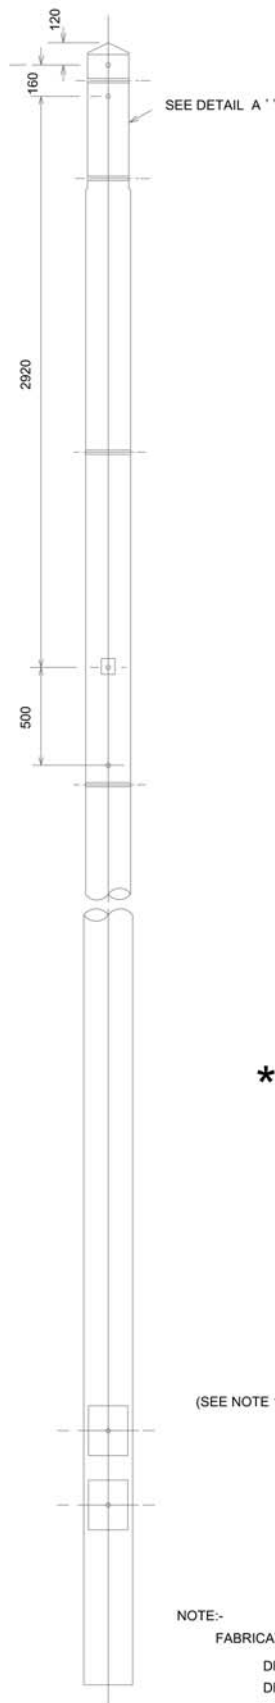


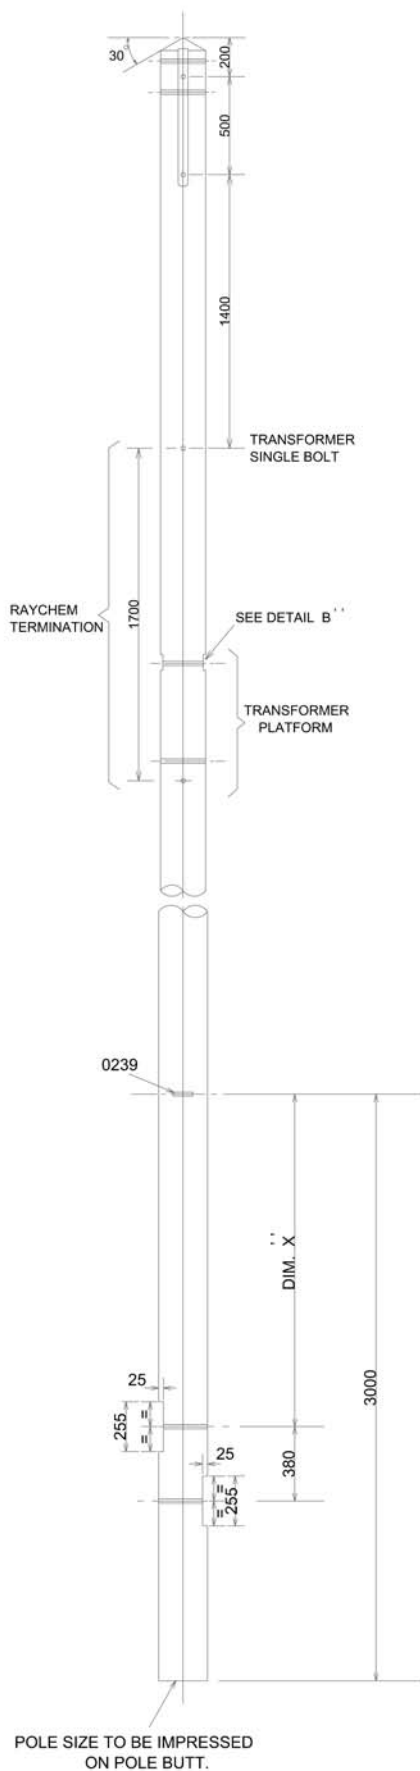

DETAIL A
SCALE 1:10

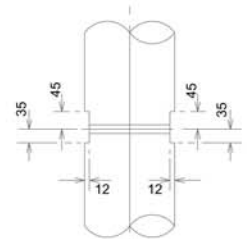

DETAIL B
SCALE 1:10

NOTES:

- * 1. STANDARD 11.0m POLE TO BE USED WHEREVER POSSIBLE.
- 2. CLASS OF POLE TO BE STOUT, POLE TOP 210mm AFTER FABRICATION.
- 3. ALL HOLES TO BE 22mm DIA. DRILLED AT RIGHT ANGLES TO VERTICAL CENTRE LINE OF POLE. ALL DRILLING AND CUTTING TO BE DONE STRICTLY TO TEMPLATE PRIOR TO PRESERVATION TREATMENT.
- 4. POLE BUTT TO BE CUT AT RIGHT ANGLES TO AXIS OF POLE.
- 5. POLE TO BE NOTCHED AND DRILLED FOR DUPLICATE 250 x 125 BAULKS.

(SEE NOTE 1)

*

POLE LENGTH. (m)	DIM. X' (mm)
9.0 - 11 INCLUSIVE	1900
12.0	1700
13 - 15 INCLUSIVE	1400
16 - 18 INCLUSIVE	1100

NOTE:-

FABRICATION DRAWING FOR USE WITH THE FOLLOWING ARRANGEMENT DRAWINGS.

DRG.No.1.00.043.4010 SHT.1
 DRG.No.1.00.043.4010 SHT.6
 DRG.No.1.09.107.0810 SHT.1
 DRG.No.1.09.107.0810 SHT.2
 DRG.No.1.09.107.0811 SHT.1
 DRG.No.1.09.107.0811 SHT.2
 DRG.No.1.09.107.0814 SHT.1
 DRG.No.1.09.107.0814 SHT.2