


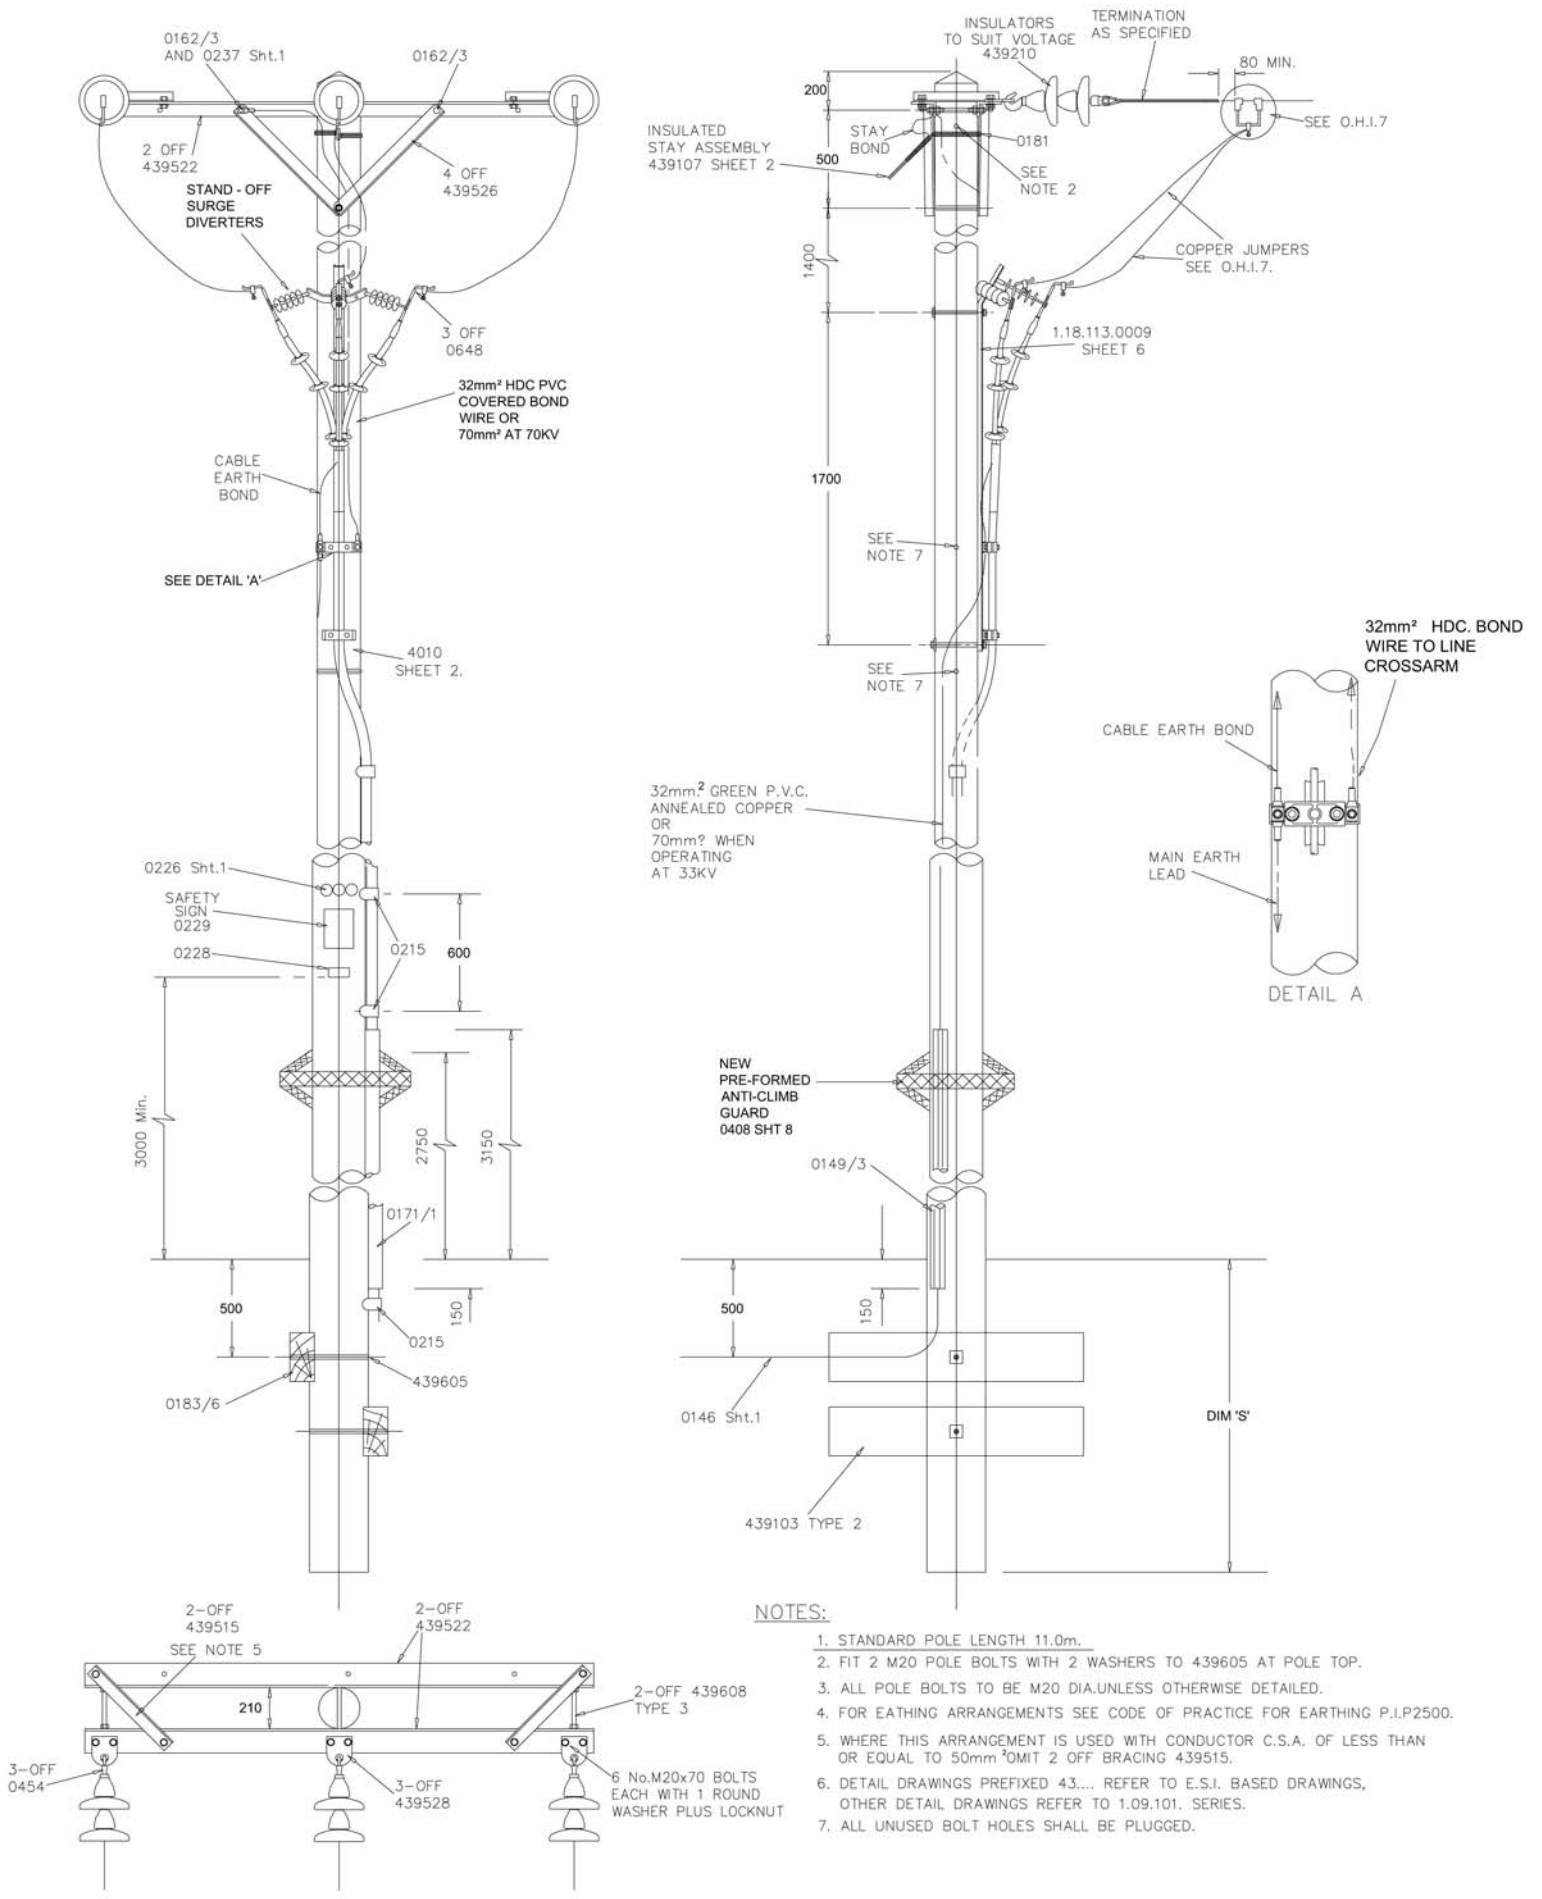

SEE NOTE 1 *

POLE LENGTH	DIM.S
11.0m.	1.9m.
12.0m.	1.9m.
13.0 - 14.0 INCL	2.1m.
15.0 - 18.0 INCL	2.4m.

ALL DIMENSIONS SHOWN ARE IN MILLIMETRES UNLESS OTHERWISE STATED

THIS DRAWING ALSO REFERRED TO IN WORKS SPEC. REF. No. 04/141

CE Electric UK Manufacturer Details		Lloyds Court, 78 Grey Street, Newcastle Upon Tyne, NE1 6AF HV OVERHEAD LINES 11KV, 20KV & 33KV TERMINAL POLE WITH HEAT SHRINK TERMINATION	
Sheet No. 6	Scale 1:20	Type ESI	ESI
Prepared By Christopher Markie	Grid Reference	Ref No. C147687	Historic Drg. No. 1000434010
Revised 11/12/08	Checked By S SALKELD	Revision G	Notes
Date Issued 16/03/05			