
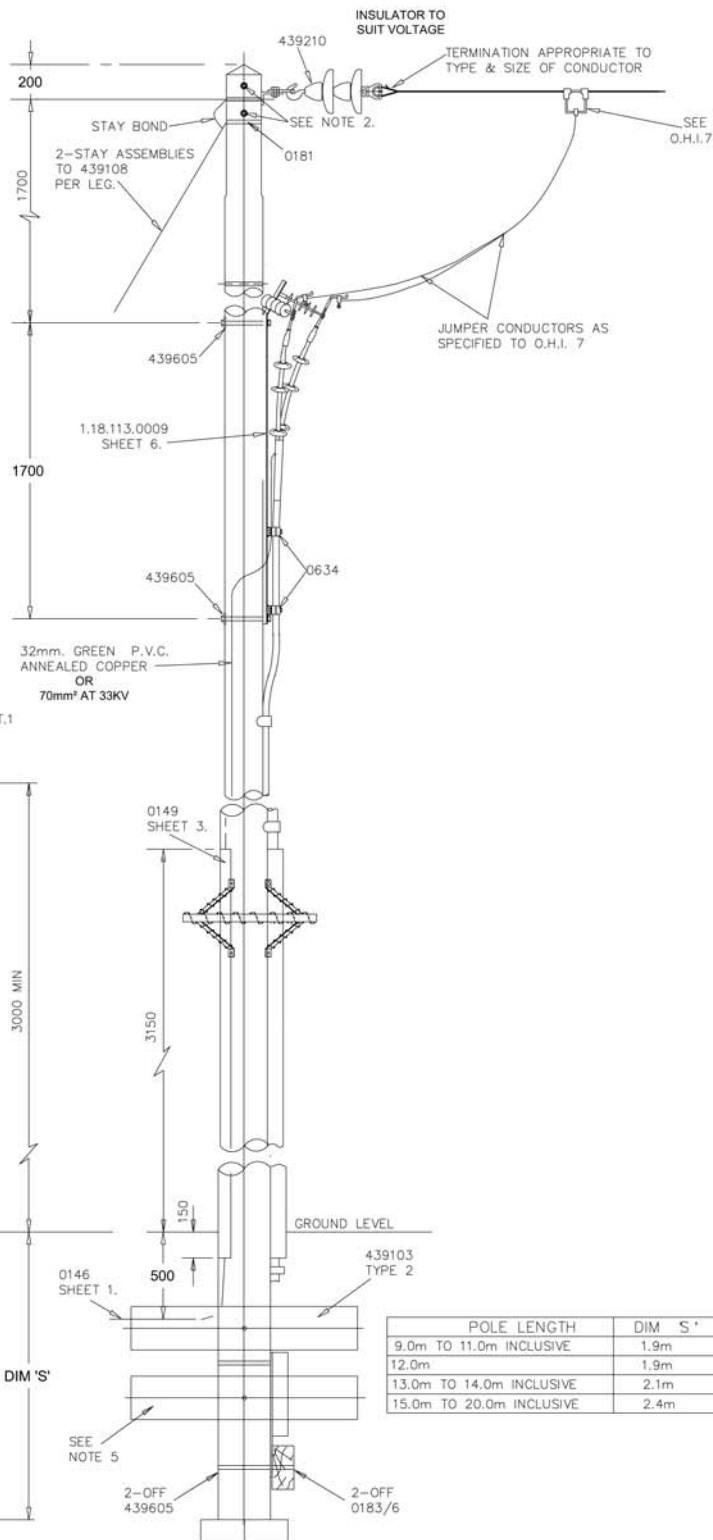
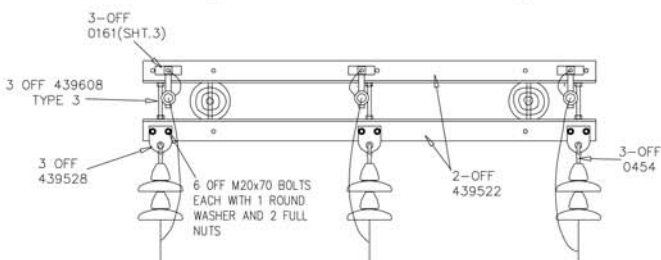


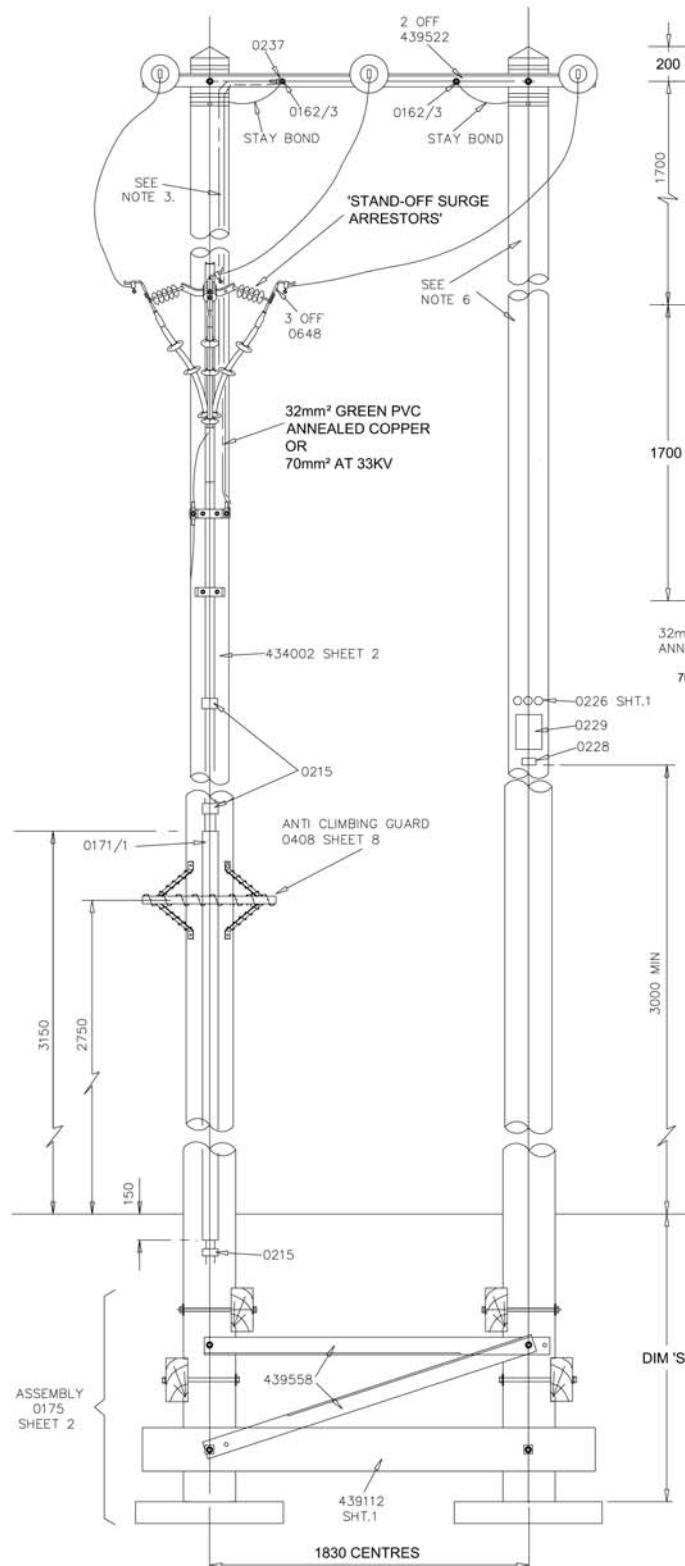

NOTES:-

1. STANDARD POLE HEIGHT - 11.0m.
2. ALL POLE BOLTS TO BE M20 DIA. UNLESS OTHERWISE DETAILED.
3. FIT 2 M20 POLE BOLTS WITH 2 WASHERS 439605 AT EACH POLE TOP.
4. DETAIL DRGS. PREFIXED 43.... REFER TO E.S.I. STANDARD DRGS. OTHER DETAIL DRGS. REFER TO 1.09.101. SERIES.
5. THE LOWER BLOCKS MAY BE OMITTED IN GOOD GROUND CONDITIONS.
6. ALL UNUSED POLE BOLT HOLES TO BE PLUGGED.

POLE LENGTH	DIM 'S'
9.0m TO 11.0m INCLUSIVE	1.9m
12.0m	1.9m
13.0m TO 14.0m INCLUSIVE	2.1m
15.0m TO 20.0m INCLUSIVE	2.4m

WORK SPEC 04/137

ALL DIMENSIONS SHOWN ARE IN MILLIMETRES UNLESS OTHERWISE STATED.

CE Electric UK

Manufacturer Details

Sheet No. 6

Scale 1:20

Prepared By Christopher Markie

Revised 11/12/08

Grid Reference

Date Issued 15/03/05

Checked By G HAMMEL

Lloyds Court, 78 Grey Street, Newcastle Upon Tyne, NE1 6AF

HV OVERHEAD LINES 'H' TERMINAL POLE (1830 CENTRES) WITH HEAT SHRINK TERMINATION FOR 11KV, 20KV AND 33KV SYSTEMS

Type ESI

ESI

Ref No. C147697

Historic Drg.No.

1000434011

Revision

Notes