


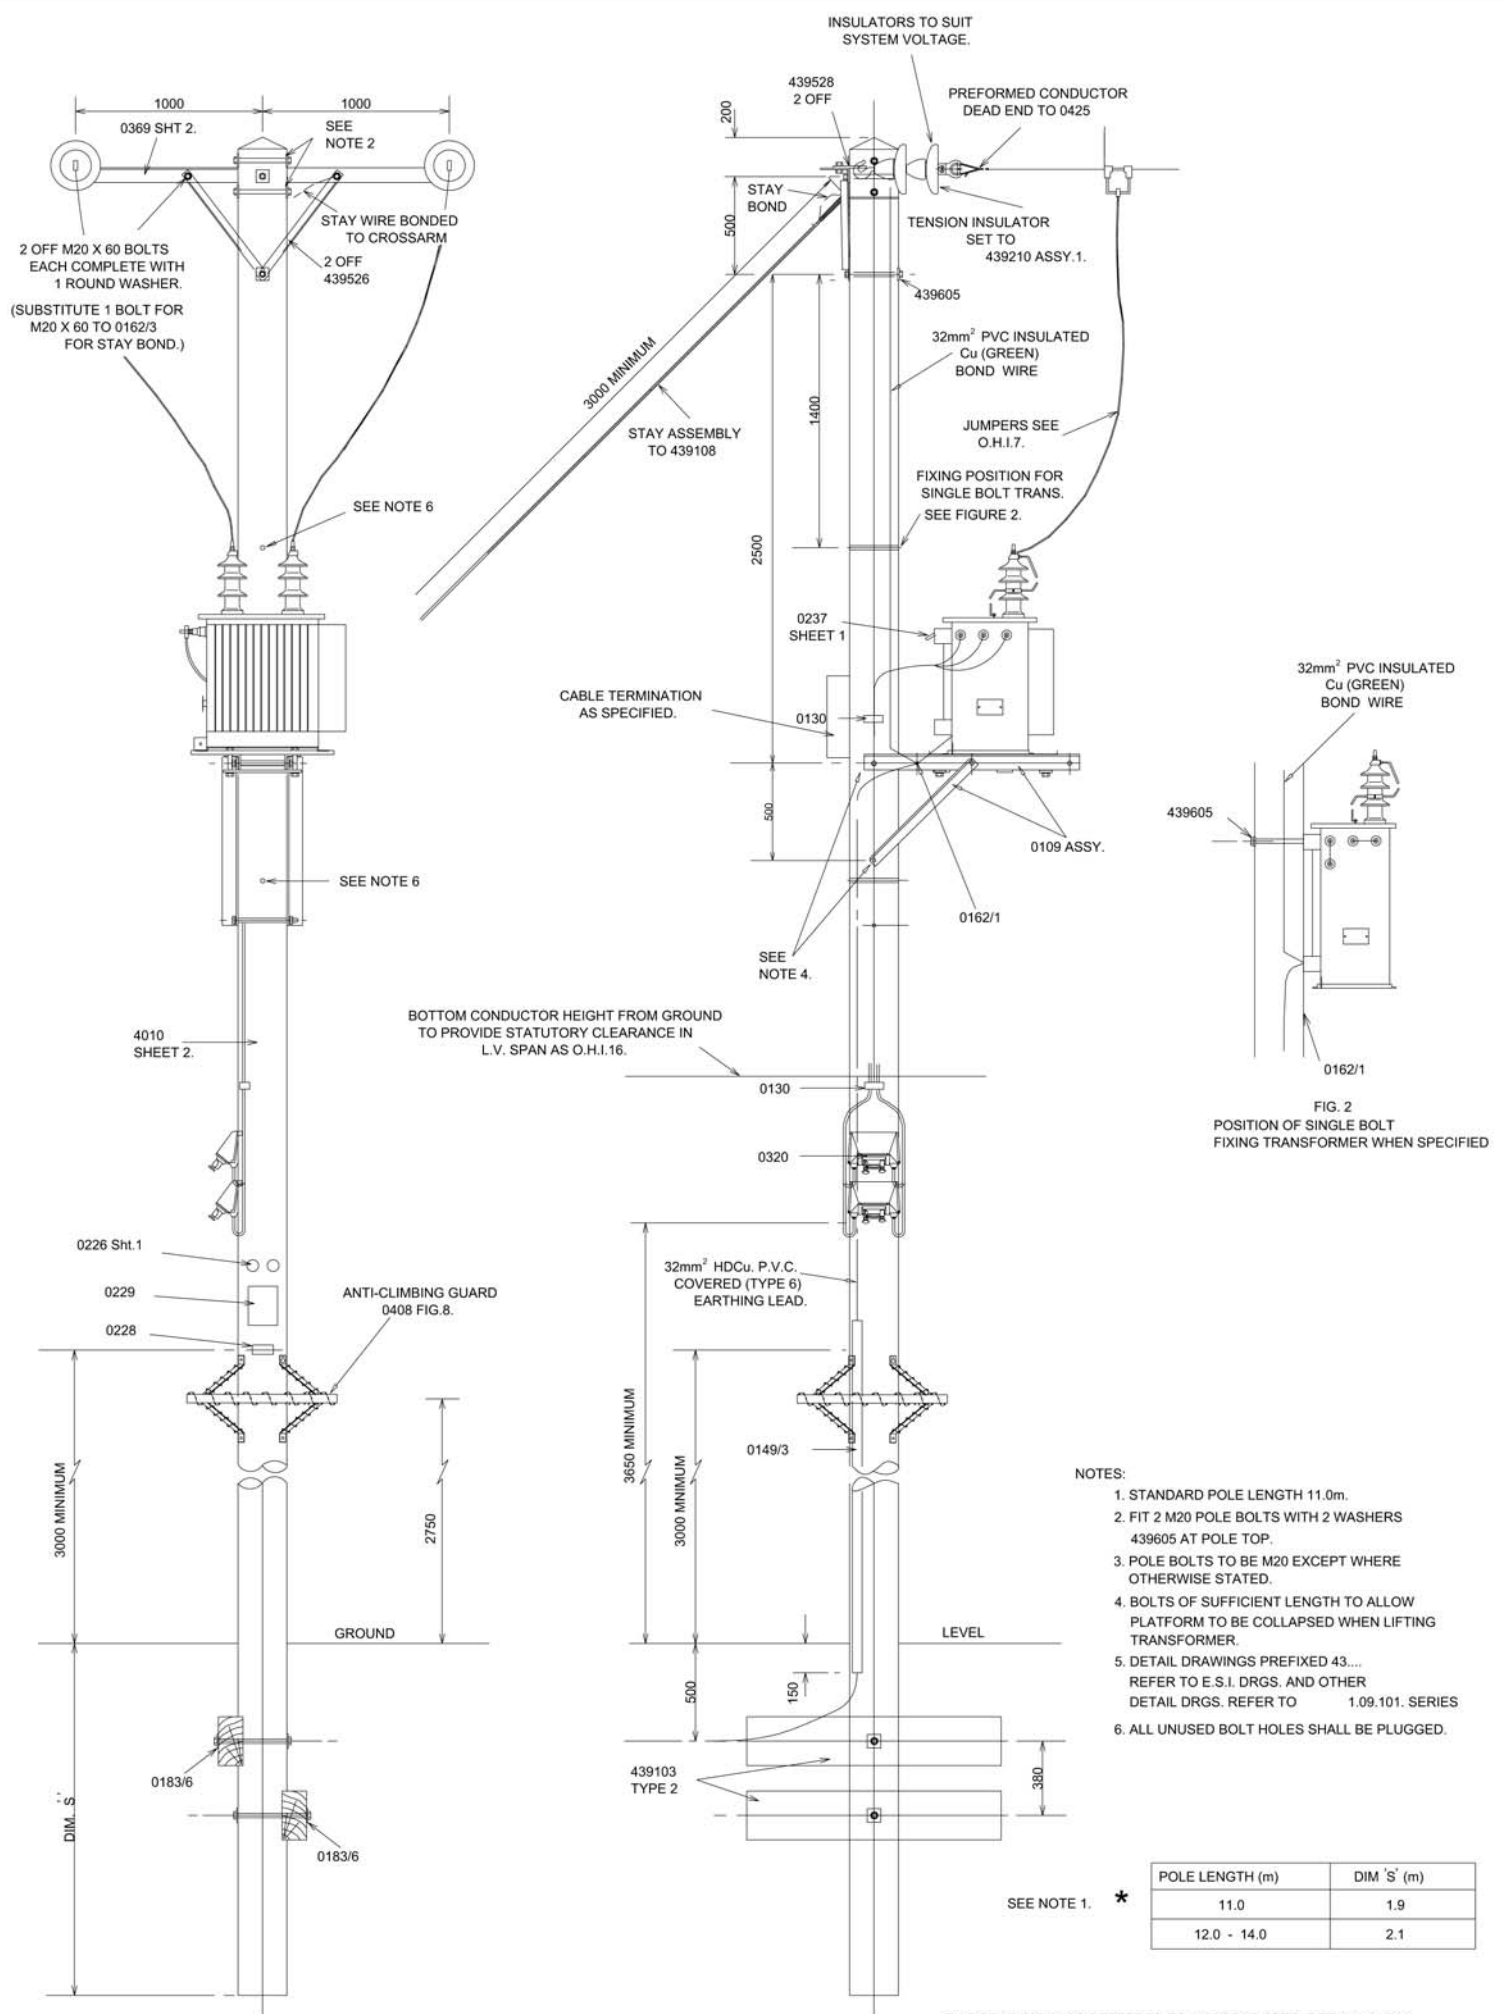

THIS DRAWING ALSO REFERRED TO IN WORKS SPEC. REF. No. 04/081

CE Electric UK

Lloyds Court, 78 Grey Street, Newcastle Upon Tyne, NE1 6AF

Manufacturer Details

11KV OVERHEAD LINES
SINGLE PHASE TERMINAL POLE SUBSTATION
WITH POLE MOUNTED TRANSFORMER

Sheet No. 1

Scale 1:20

Prepared By Barbara Gordon

Type OVERHEAD

Revised 16/06/09

Grid Reference

Ref No. C101699

Historic Drg. No.

1091070810

Date Issued 26/07/99

Checked By G HAMMEL

Revision J

Notes

ALL DIMENSIONS SHOWN ARE IN MILLIMETRES UNLESS OTHERWISE STATED.