

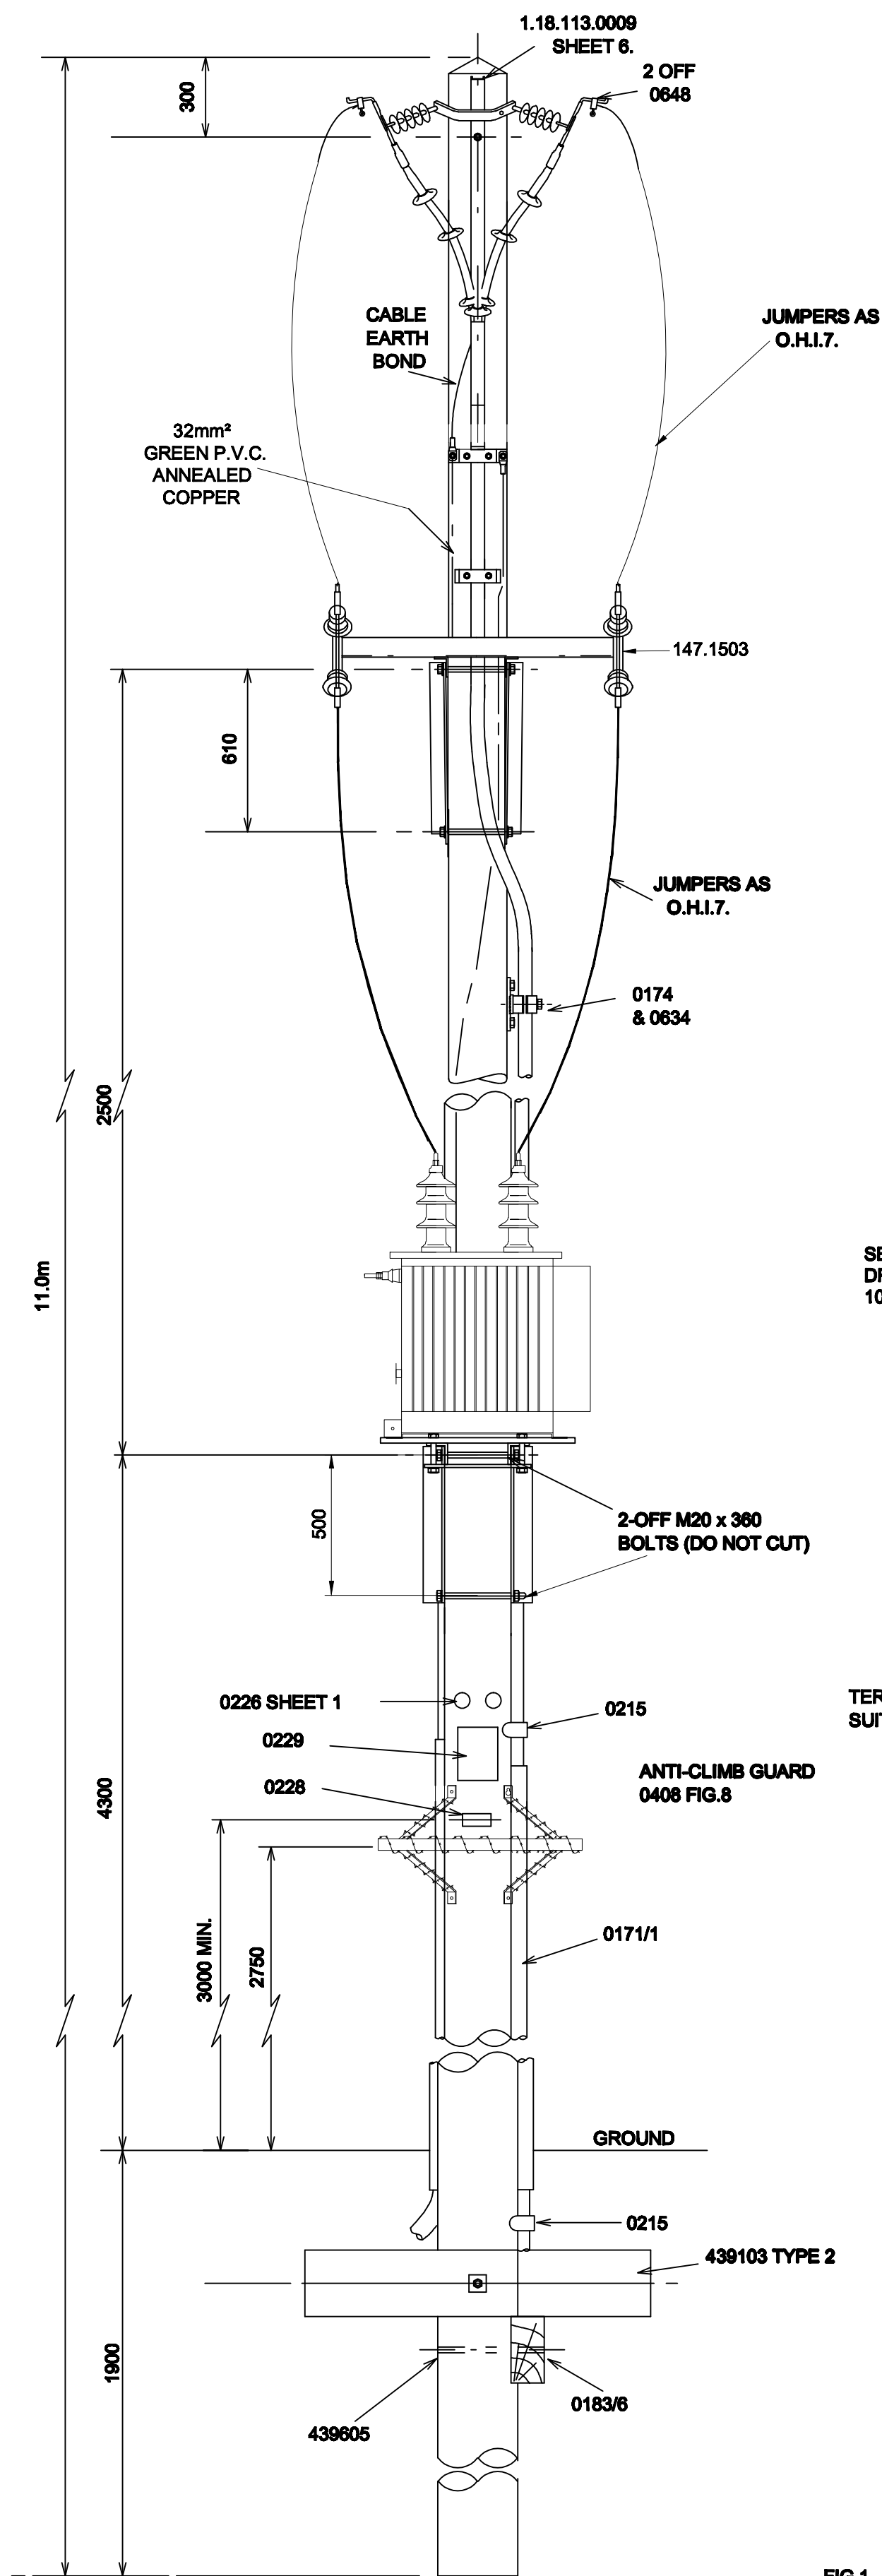


FIG. 1.

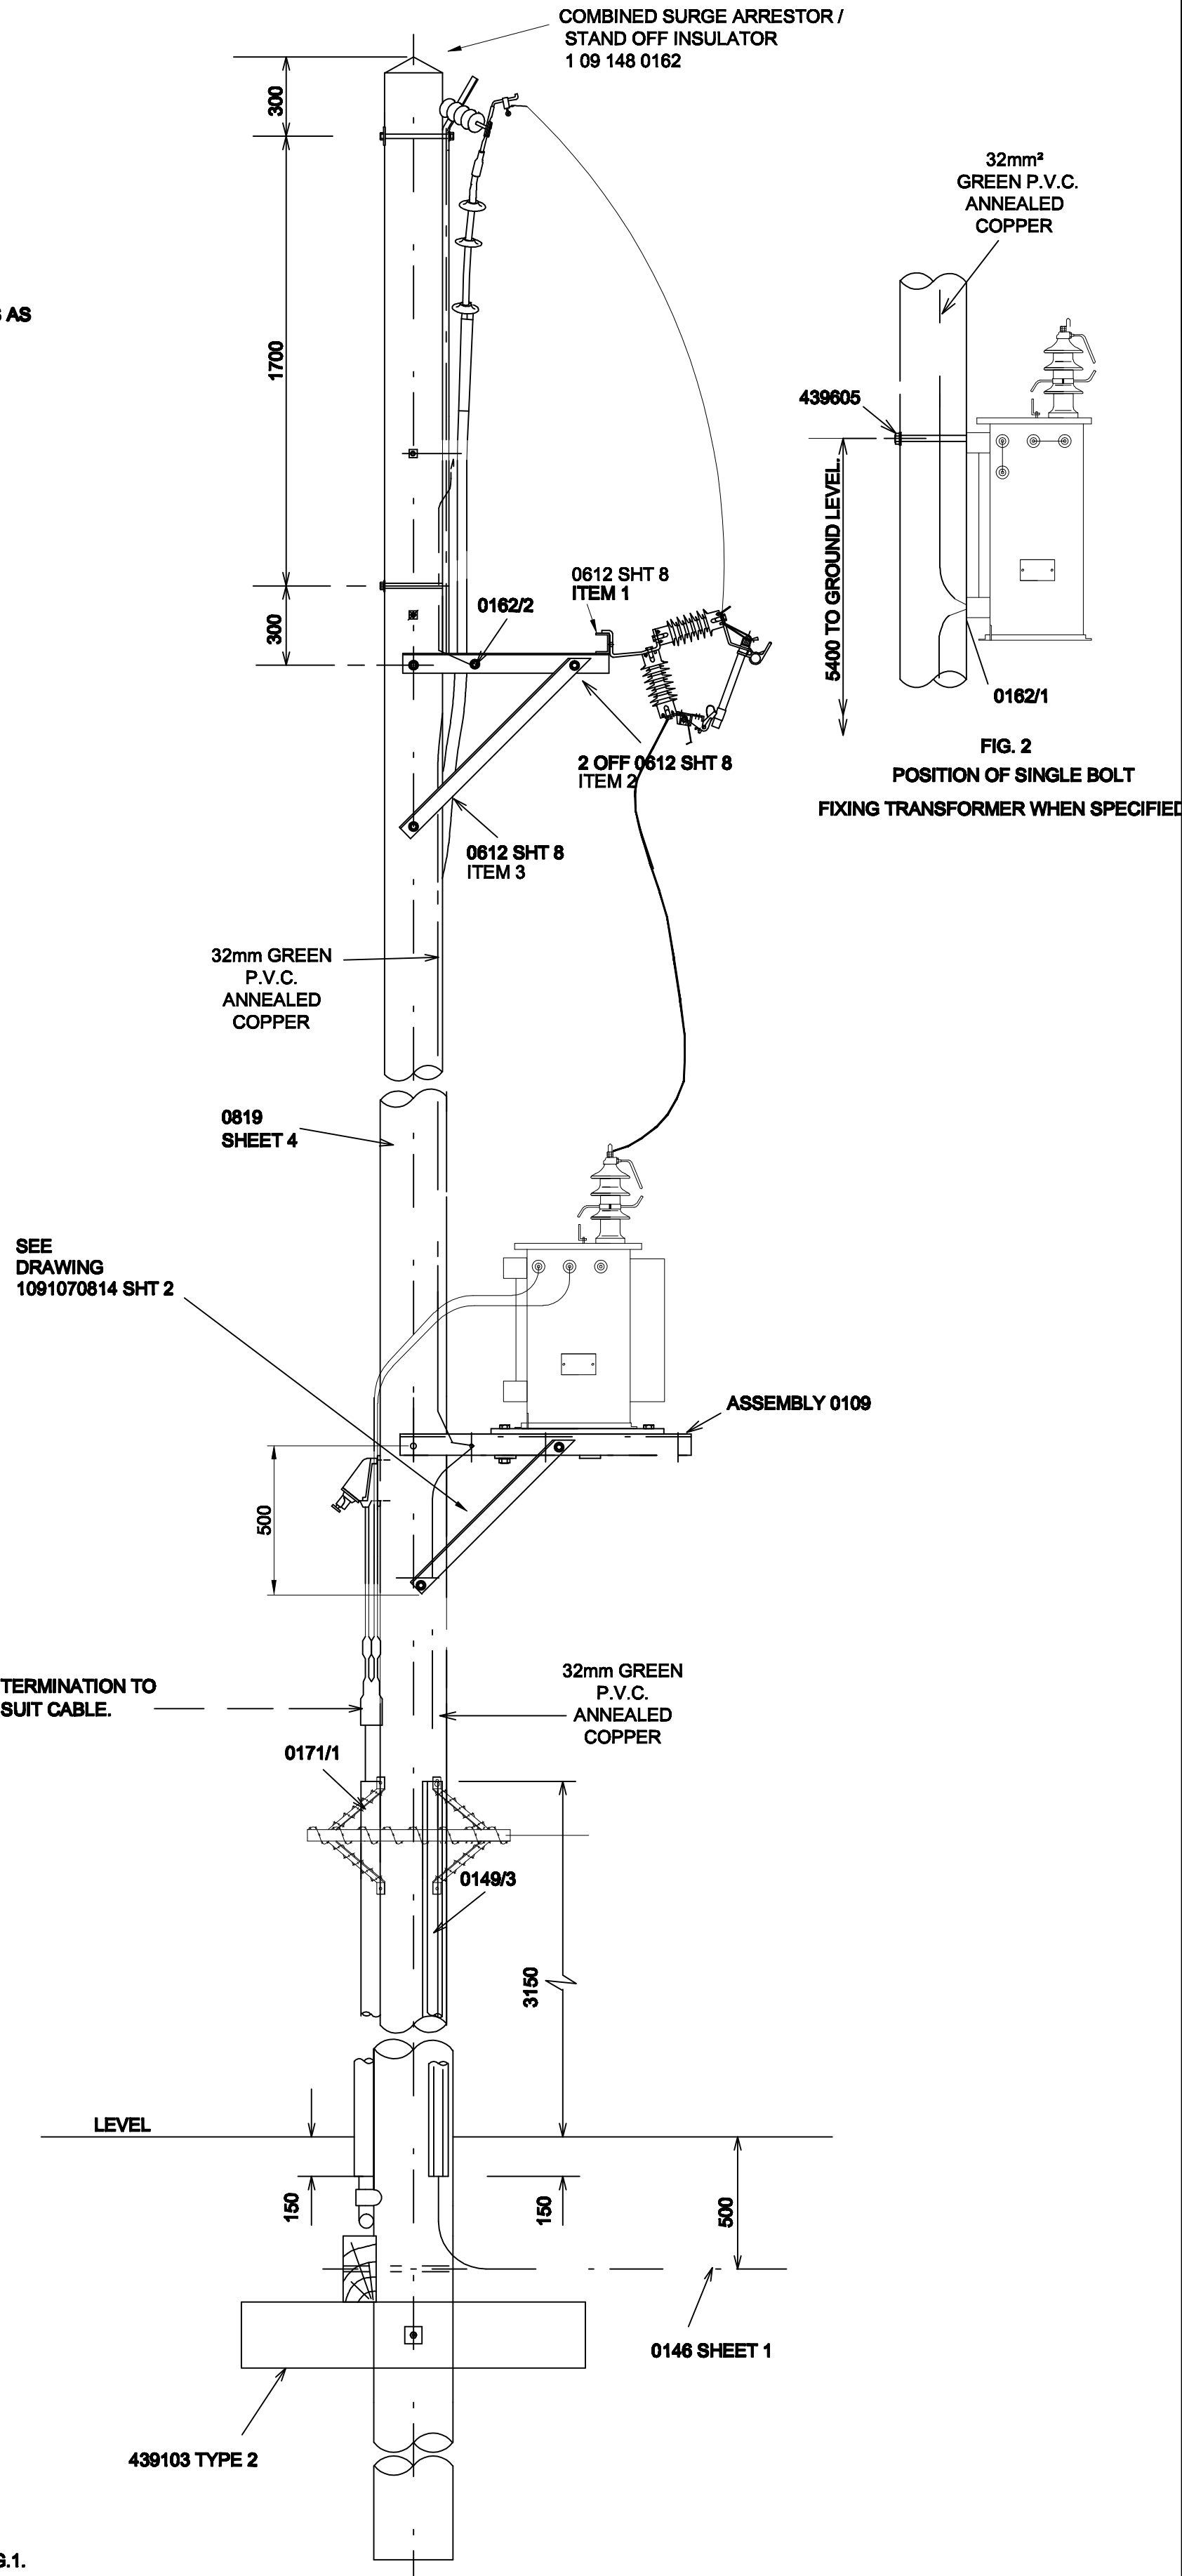


FIG. 2
POSITION OF SINGLE BOLT
FIXING TRANSFORMER WHEN SPECIFIED

NOTES:

1. POLE LENGTH TO BE 11.0m.
2. DETAIL DRGS. PREFIXED 43.... REFER TO E.S.I. BASED DRAWINGS. OTHER DETAIL DRGS. REFER TO 1.09.101. SERIES.
3. TRANSFORMER CAPACITY 50kVA MAX (SINGLE BOLT FIXING.) 100kVA MAX (PLATFORM MOUNTED)

ALL DIMENSIONS SHOWN ARE IN MILLIMETRES UNLESS OTHERWISE STATED.

THIS DRAWING ALSO REFERRED TO IN WORKS SPEC. REF. No. 04/085

CE Electric UK Manufacturer Details		Lloyds Court, 78 Grey Street, Newcastle Upon Tyne, NE1 6AF	
Sheet No. 3	Scale 1:20	11/ 20KV O/H LINES SINGLE PHASE TOTEM POLE S/S WITH H.V. FUSE UNITS & H.V. SUPPLY OFF UNDERGROUND CABLE & UNDERGROUND SUPPLY TO L.V. NETWORK	
Prepared By Pauline.Moore	Grid Reference	Type OVERHEAD	
Revised 20/08/09	Checked By G HAMMEL	Ref No. C101705	Historic Drg.No. 1091070819
Date Issued 24/02/05		Revision E	Notes