
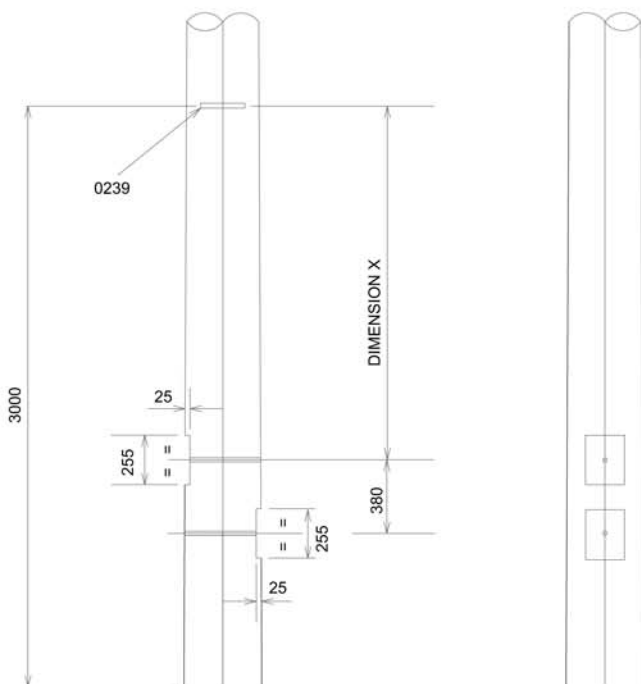


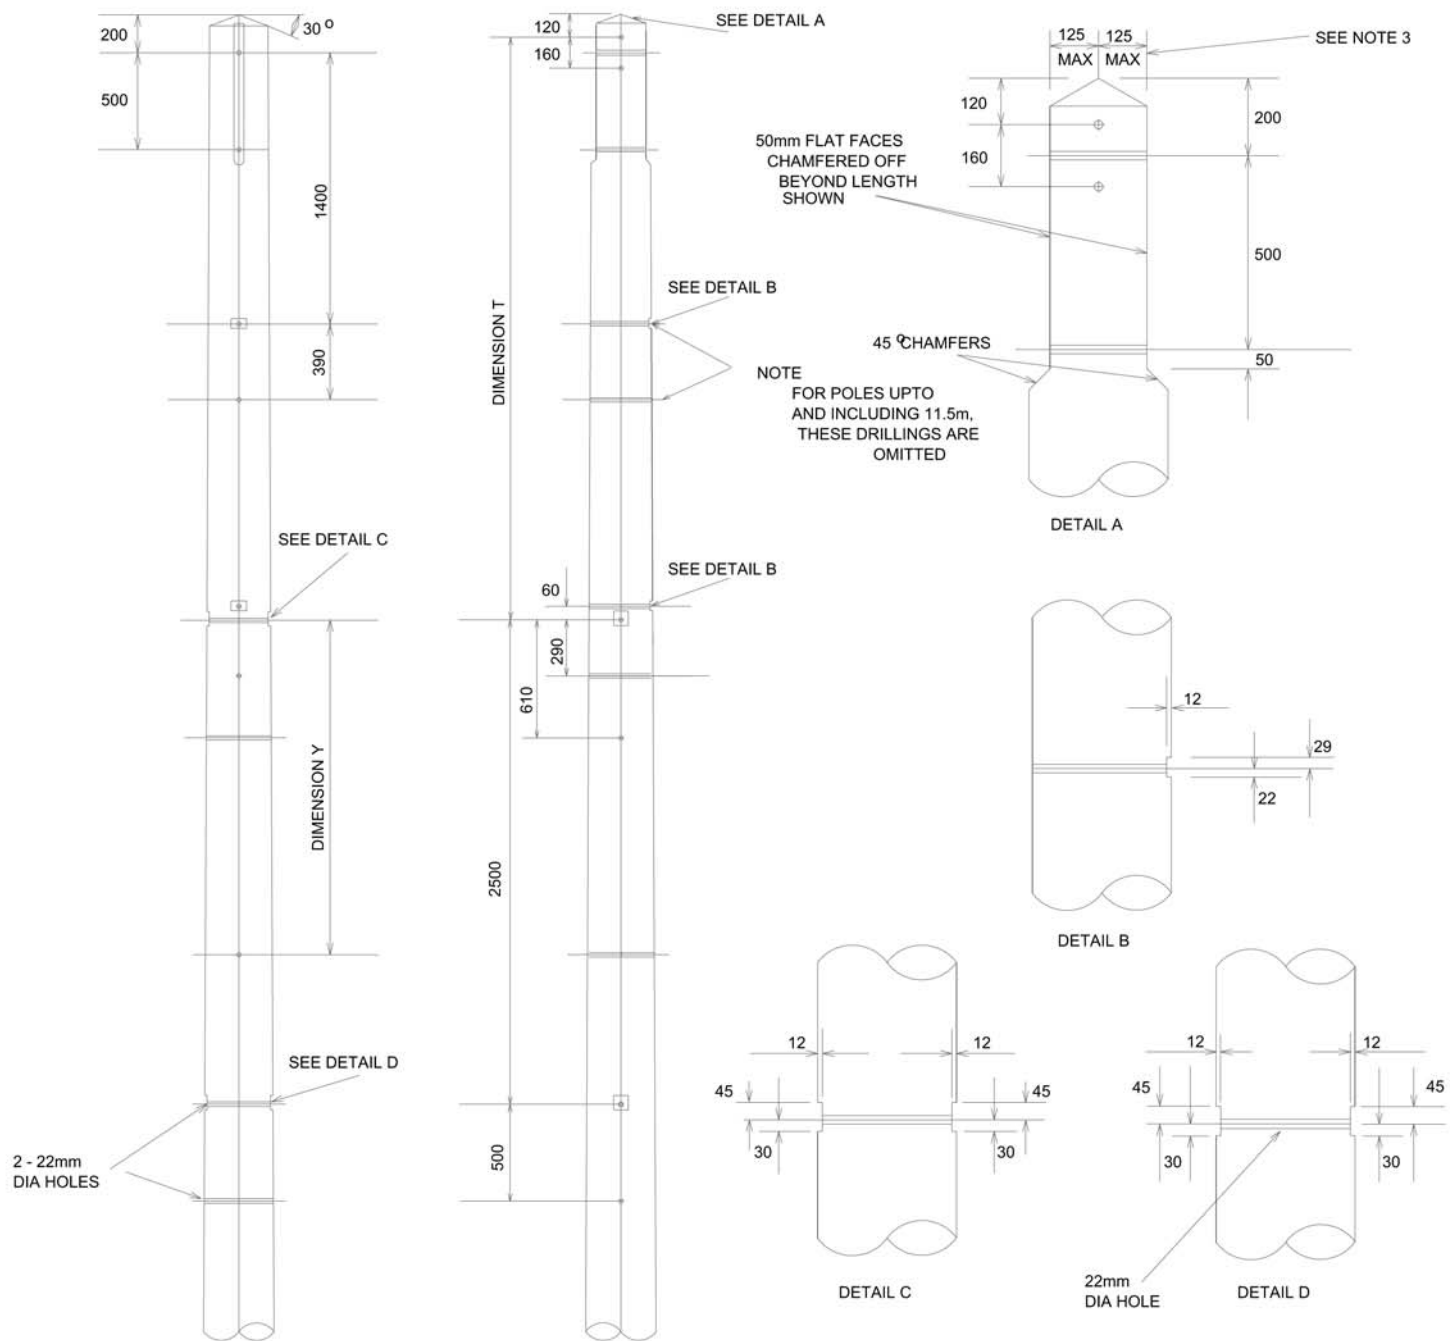

NOTES

1. MINIMUM POLE LENGTH 11.0m
2. CLASS OF POLE STOUT
3. MINIMUM POLE TOP DIAMETER TO BE 210mm AFTER FABRICATION
4. HOLES TO BE 22mm DIA. UNLESS OTHERWISE STATED, DRILLED AT RIGHT ANGLES TO VERTICAL CENTRE LINE OF POLE. ALL DRILLING AND CUTTING TO BE DONE STRICTLY TO TEMPLATE PRIOR TO CREOSOTING.
5. POLE BUTT TO BE CUT AT RIGHT ANGLES TO AXIS OF POLE

POLE LENGTH metres	DIMENSION T metres	DIMENSION X metres	DIMENSION Y metres
11.0	1.95	1.9	2.05
12.0	2.95	1.7	1.85
13.0	3.65	1.4	1.85
14.0	3.65	1.4	1.85

FIGS 1,2,3 AND 4
FOR SHEETS 1 AND 3

ALL DIMENSIONS SHOWN ARE IN MILLIMETRES UNLESS OTHERWISE STATED



Manufacturer Details

Sheet No. 2 Scale 1:20

Prepared By Barbara Simpson

Revised 08/03/06 Grid Reference

Date Issued 19/08/99 Checked By G HAMMEL

Lloyds Court, 78 Grey Street, Newcastle Upon Tyne, NE1 6AF

11KV OVERHEAD LINES. HV CONSTRUCTION DRILLING, SCARFING & MARKING IN LINE TERMINAL & LAYPOLE S/S WITH HV FUSE UNITS (SEE DRG. 1091080821 S1 & 3)

Type OVERHEAD

Ref No. C101709

Revision G Notes

Historic Drg. No. 1091080821