

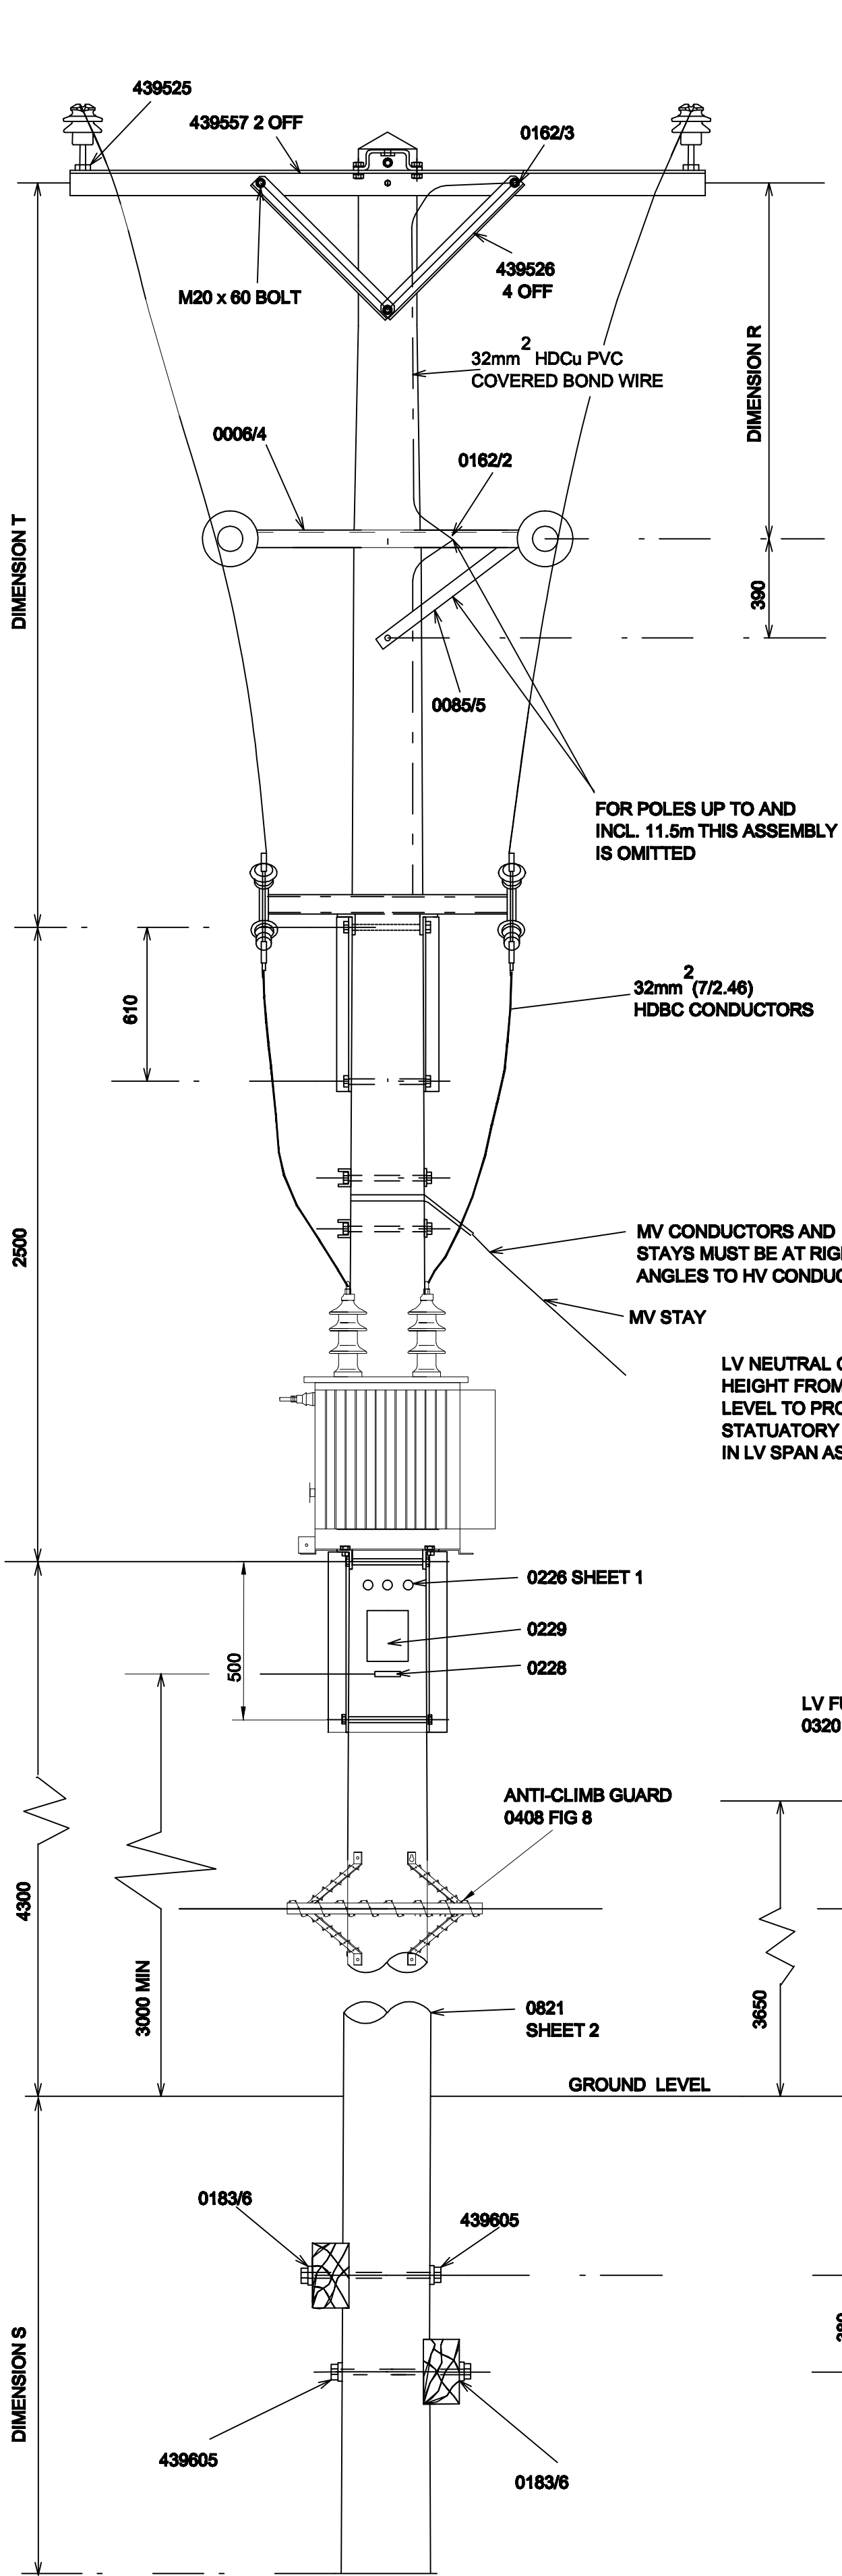


FIG 1 PLATFORM MOUNTED TRANSFORMER
IN LINE ARRANGEMENT

POLE LENGTH	DIMENSION S	DIMENSION R	DIMENSION T
11.0m	1.9m	-	1.95m
12.0m	2.1m	1.4m	2.95m
13.0m	2.1m	1.4m	3.65m
14.0m	2.1m	1.4m	3.65m

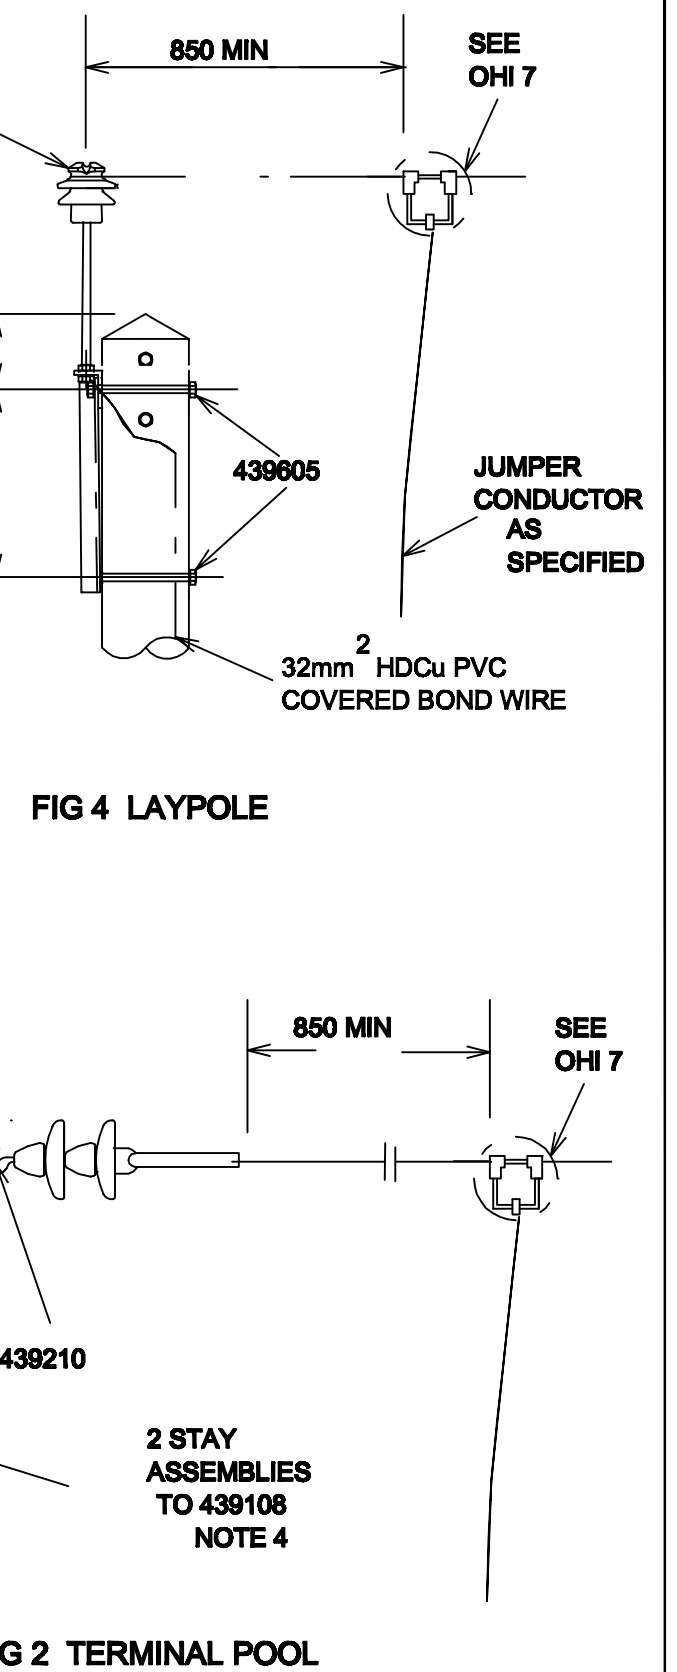
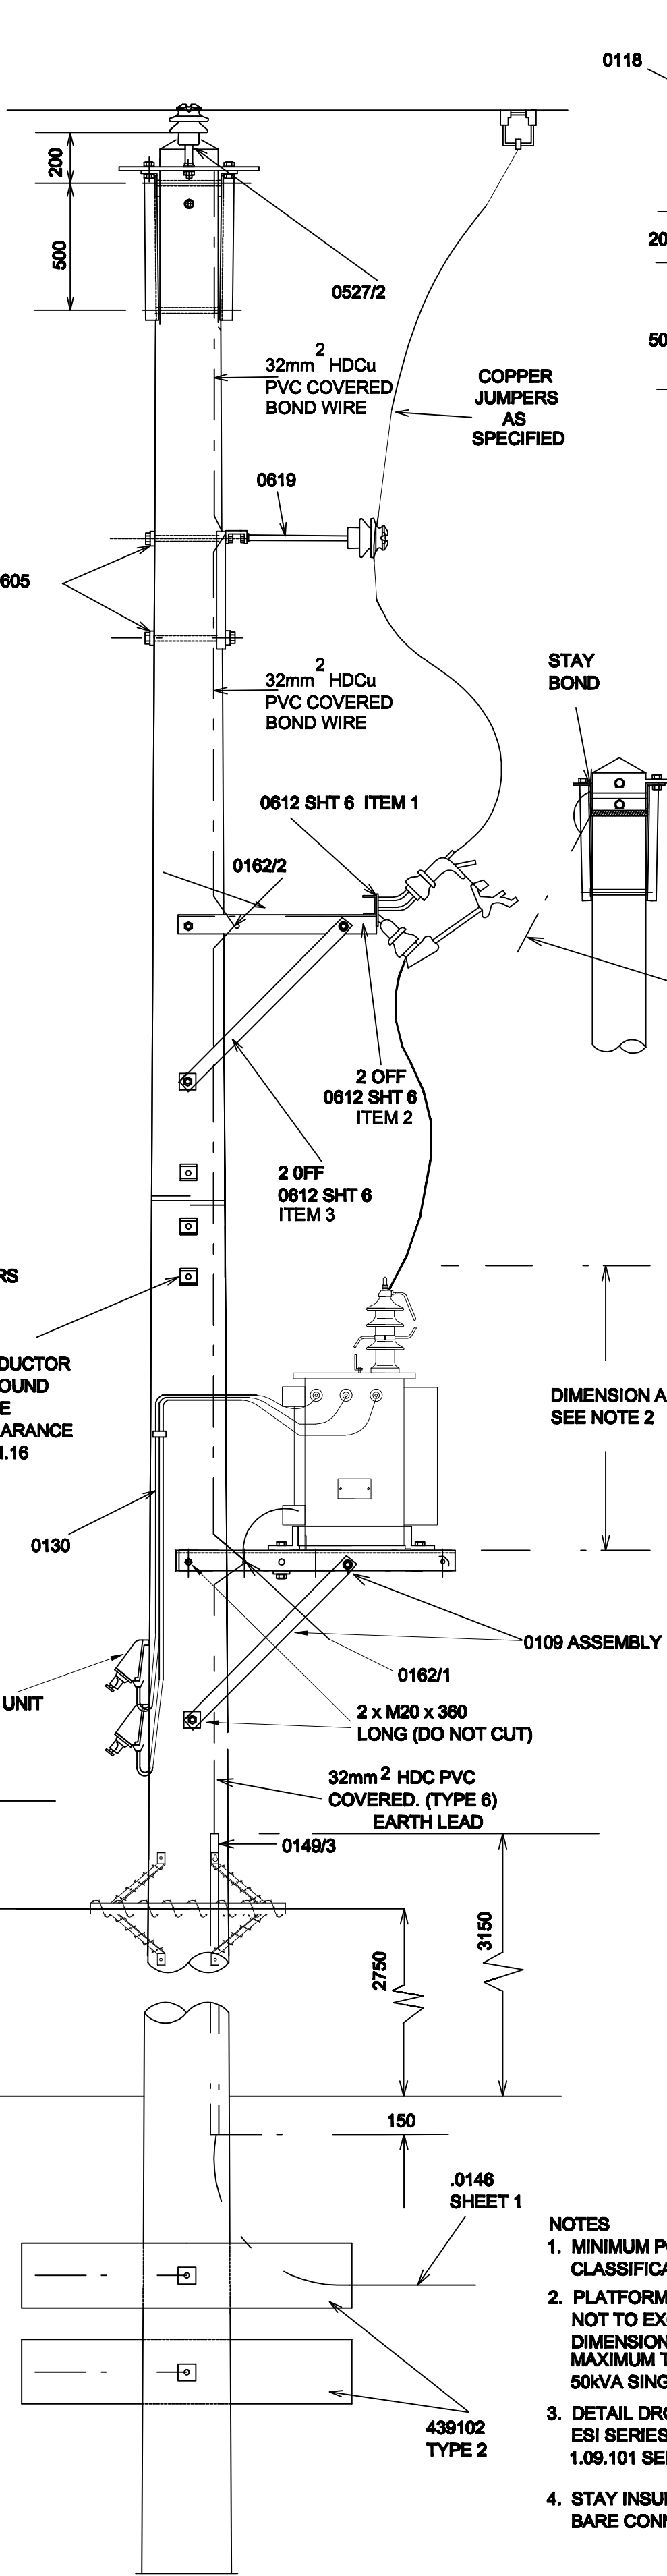


FIG 2 TERMINAL POOL

FIG 3 SINGLE BOLT
FIXING TRANSFORMER

- NOTES
1. MINIMUM POLE LENGTH 11.0M
CLASSIFICATION : STOUT
 2. PLATFORM MOUNTED TYPE TRANSFORMER
NOT TO EXCEED THE FOLLOWING DIMENSIONS
DIMENSION A 1320
MAXIMUM TRANSFORMER 100kVA PLATFORM MOUNTED
50kVA SINGLE BOLT MOUNTED
 3. DETAIL DRGS PREFIXED 43..... REFER TO
ESI SERIES, OTHER DETAIL DRGS REFER TO
1.09.101 SERIES
 4. STAY INSULATOR TO BE LOWEST LIVE
BARE CONNECTION SEE OHI.4

CE Electric UK

Manufacturer Details

Sheet No. 3

Scale 1:20

Prepared By Pauline Moore

Revised 20/08/09

Date Issued 26/07/99

Grid Reference

Checked By G HAMMEL

Lloyds Court, 78 Grey Street, Newcastle Upon Tyne, NE1 6AF

11KV O/H LINES IN LINE TERMINAL & LAYPOLE S/S
WITH OR WITHOUT LV FUSE UNITS (SINGLE PHASE)

Type OVERHEAD

Ref No. C101710

Historic Drg.No. 1091080821

Revision B

Notes