
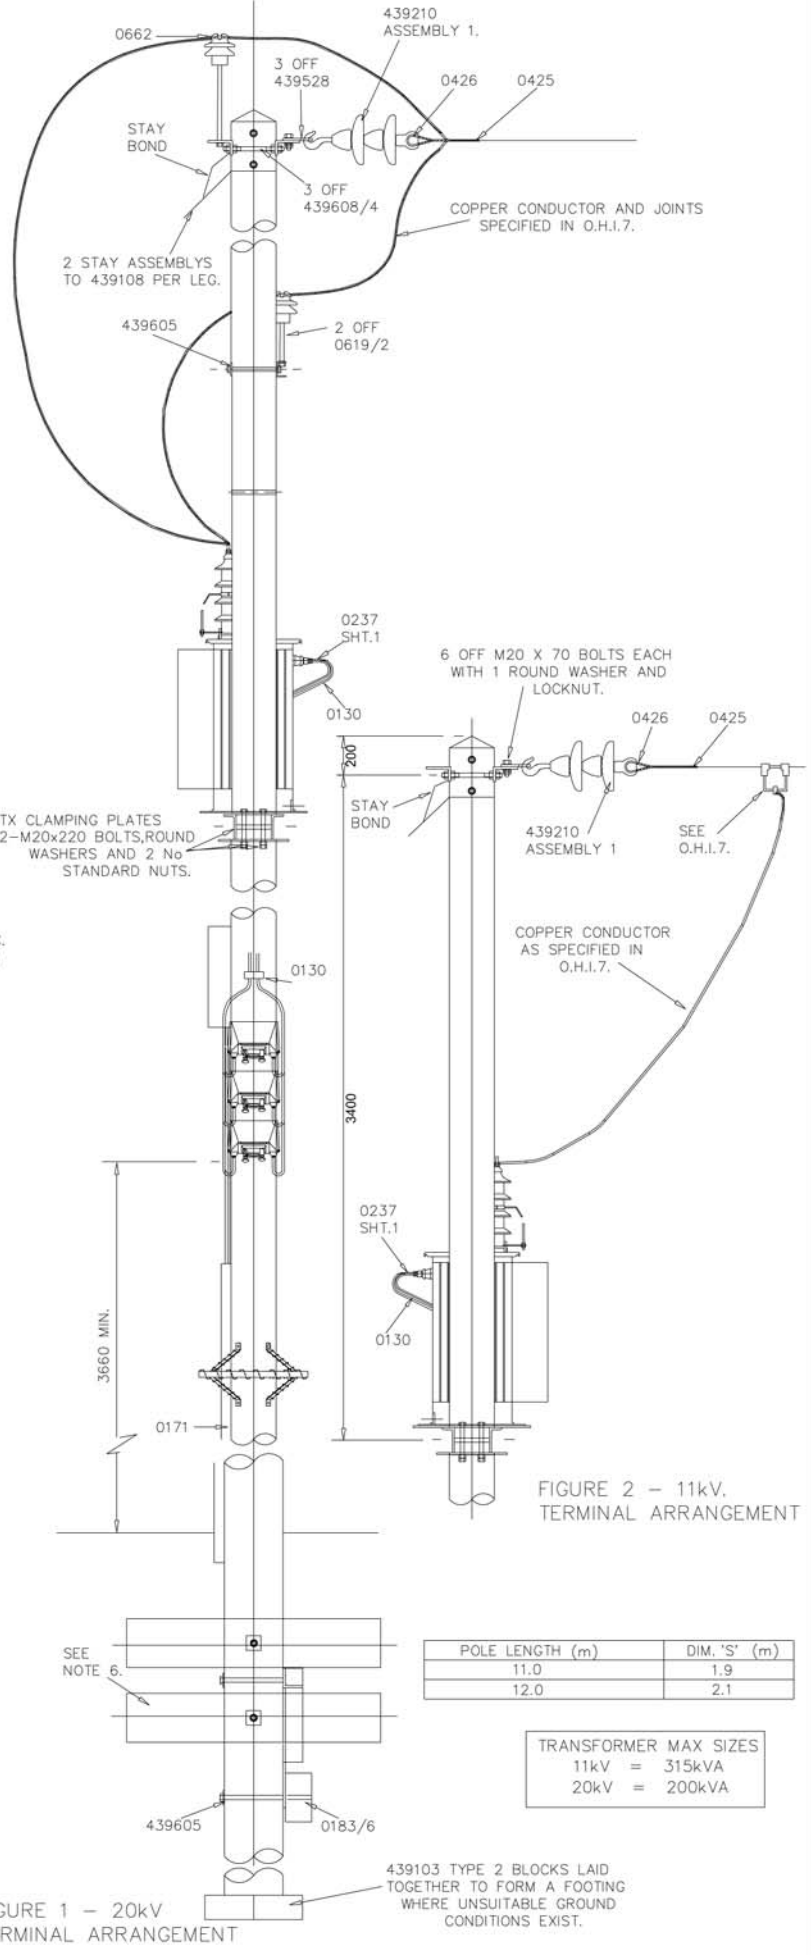


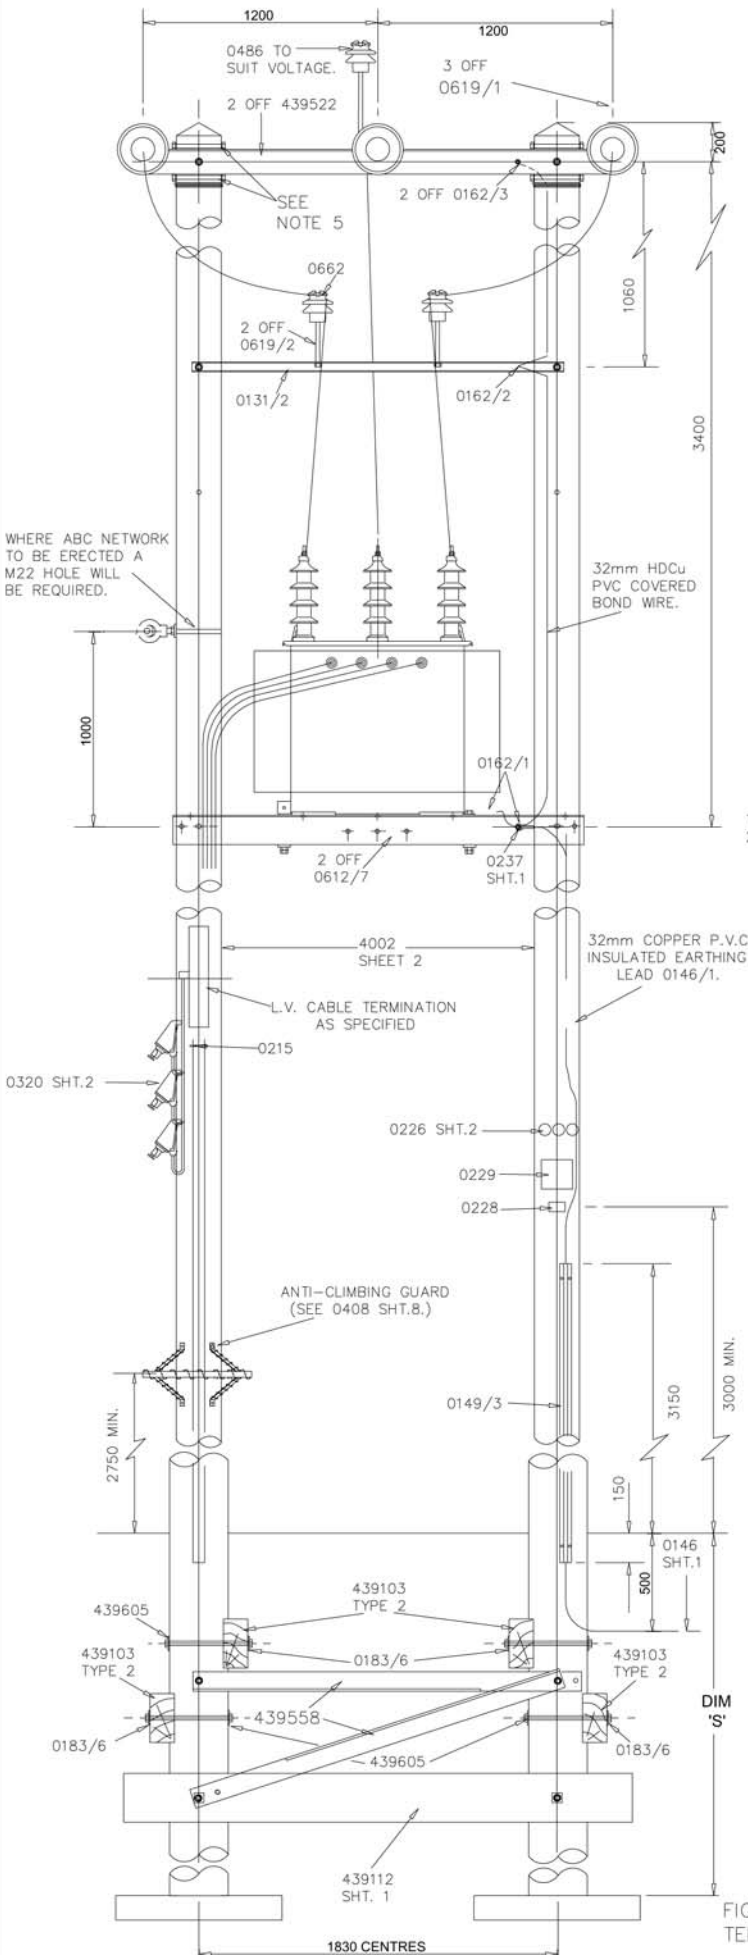

NOTES:

1. STANDARD POLE HEIGHT - 11.0m.
2. POLE BOLTS TO BE M20.
3. SEE CODE OF PRACTICE FOR EARTHING - E500.
4. DETAIL DRAWINGS PREFIXED 43... REFER TO E.S.I. BASED DRAWINGS. OTHER DETAIL DRAWINGS REFER TO 1.09.101.SERIES.
5. FIT M20 BOLTS WITH 2 WASHERS 439605 AT POLE TOP.
6. THE LOWER BLOCK MAY BE OMITTED IN GOOD GROUND CONDITIONS.
7. ALL UNUSED POLE BOLT HOLES TO BE PLUGGED.

ALL DIMENSIONS SHOWN ARE IN MILLIMETRES UNLESS STATED OTHERWISE.

THIS DRAWING ALSO REFERRED TO IN WORK SPEC. REF. NO 04/093.

|   |  |   |  |                              |
|---|--|---|--|------------------------------|
| <b>CE Electric UK</b><br>Manufacturer Details<br>Sheet No. 1<br>Scale 1:20<br>Prepared By Jonis Webb<br>Revised 11/04/06<br>Date Issued 26/07/99 |  | <b>Lloyds Court, 78 Grey Street, Newcastle Upon Tyne, NE1 6AF</b><br>11kV & 20kV OVERHEAD LINES<br>THREE PHASE P.M. SUBSTATION(1.83M CENTRES)<br>SUITABLE FOR SINGLE TRANSFORMER<br>UP TO 315kVA TERMINAL ARRANGEMENT<br>Type OVERHEAD LINES<br>Ref No. C101711<br>Grid Reference<br>Checked By J WEBB<br>Revision G |  | Historic Drg. No. 1091080860 |
|---|--|---|--|------------------------------|