


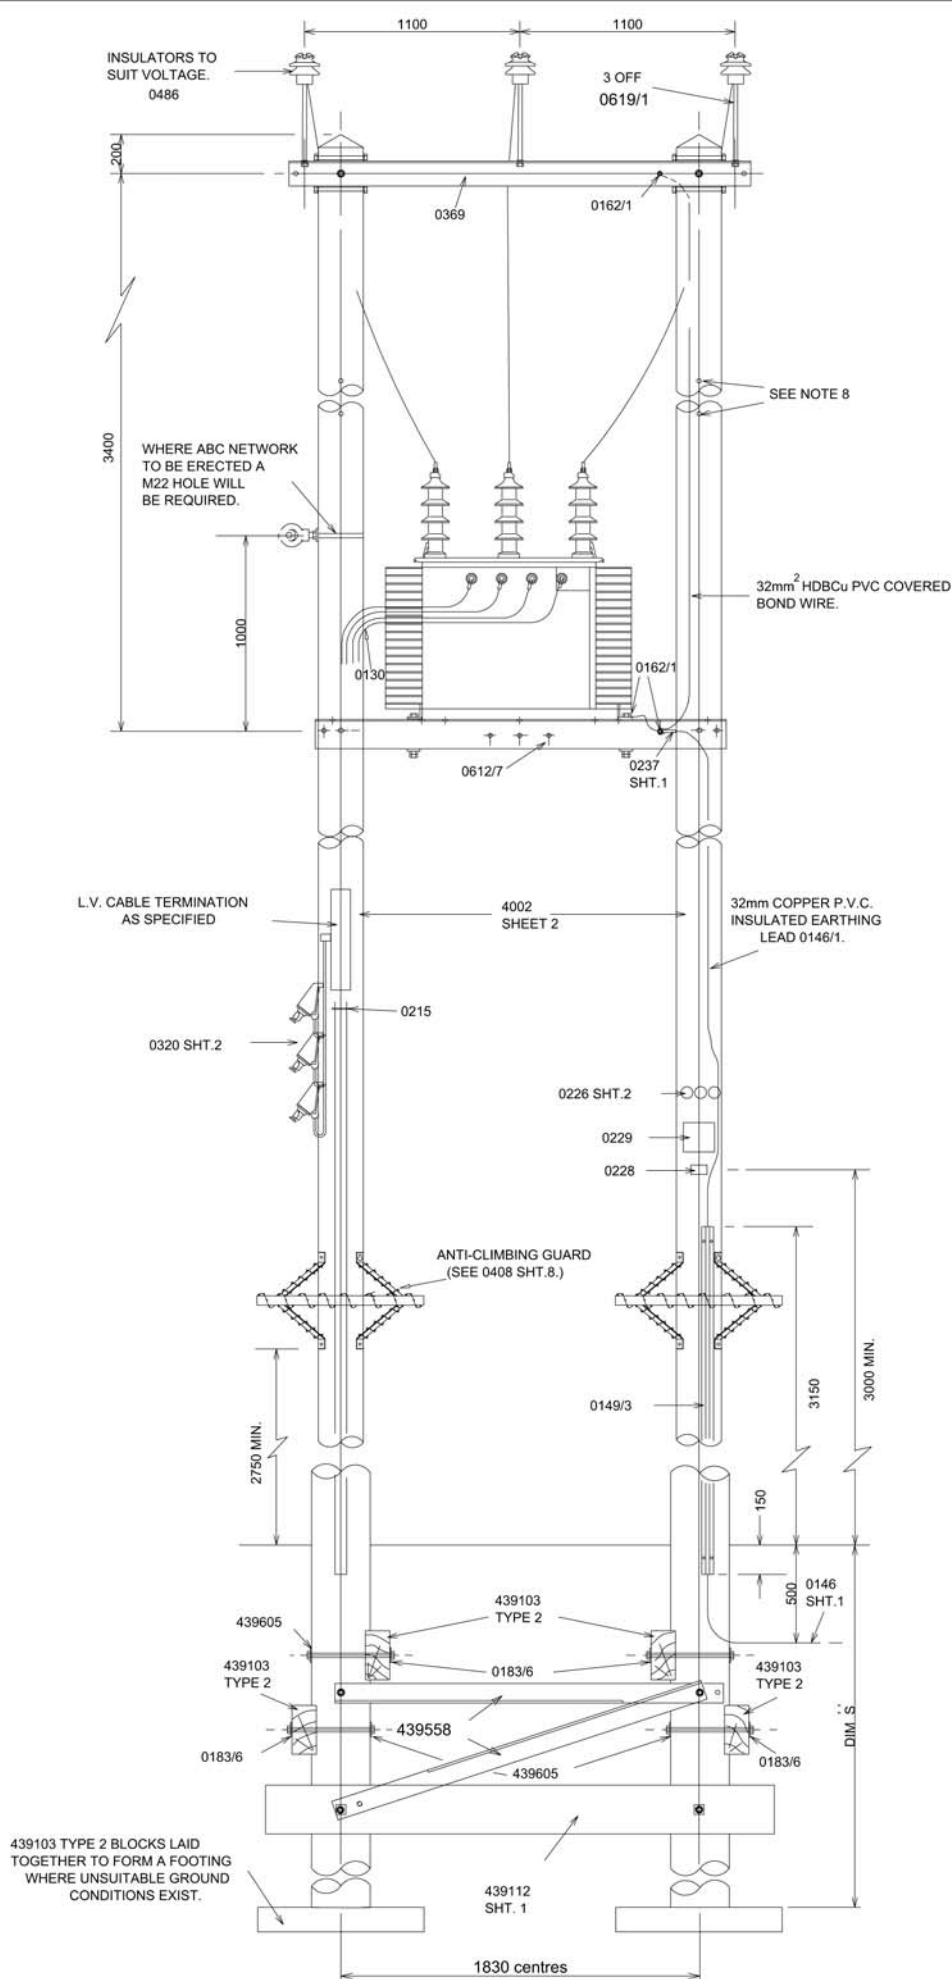

NOTES:

- STANDARD POLE HEIGHT - 11.0m.
- POLE BOLTS TO BE M20.
- SEE CODE OF PRACTICE FOR EARTHING - E500.
- MINIMUM POLE HEIGHT 10.0m.
- DETAIL DRAWINGS PREFIXED 43... REFER TO E.S.I. BASED DRAWINGS. OTHER DETAIL DRAWINGS REFER TO 1.09.101.SERIES.
- FIT M20 BOLTS WITH 2 WASHERS 439605 AT POLE TOP.
- THE LOWER BLOCK MAY BE OMITTED IN GOOD GROUND CONDITIONS.
- ALL UNUSED POLE BOLT HOLES TO BE PLUGGED.

ALL DIMENSIONS SHOWN ARE IN MILLIMETRES UNLESS STATED OTHERWISE.

THIS DRAWING ALSO REFERRED TO IN WORK SPEC. REF. NO 04/093.



Manufacturer Details

Sheet No. 3 Scale 1:20

Prepared By Janis Webb

Revised 10/04/06 Grid Reference

Date Issued 26/07/99 Checked By G HAMMEL

Lloyds Court, 78 Grey Street, Newcastle Upon Tyne, NE1 6AF
11/20KV O/H LINES 3 PHASE PM S/S (1.83M CENTRES)
SUITABLE FOR SINGLE TRANSFORMER UP TO 315KVA.
LAYPOLE ARRANGEMENT

Type OVERHEAD

Ref No. C101712 Historic Drg. No. 1091080860

Revision F Notes