

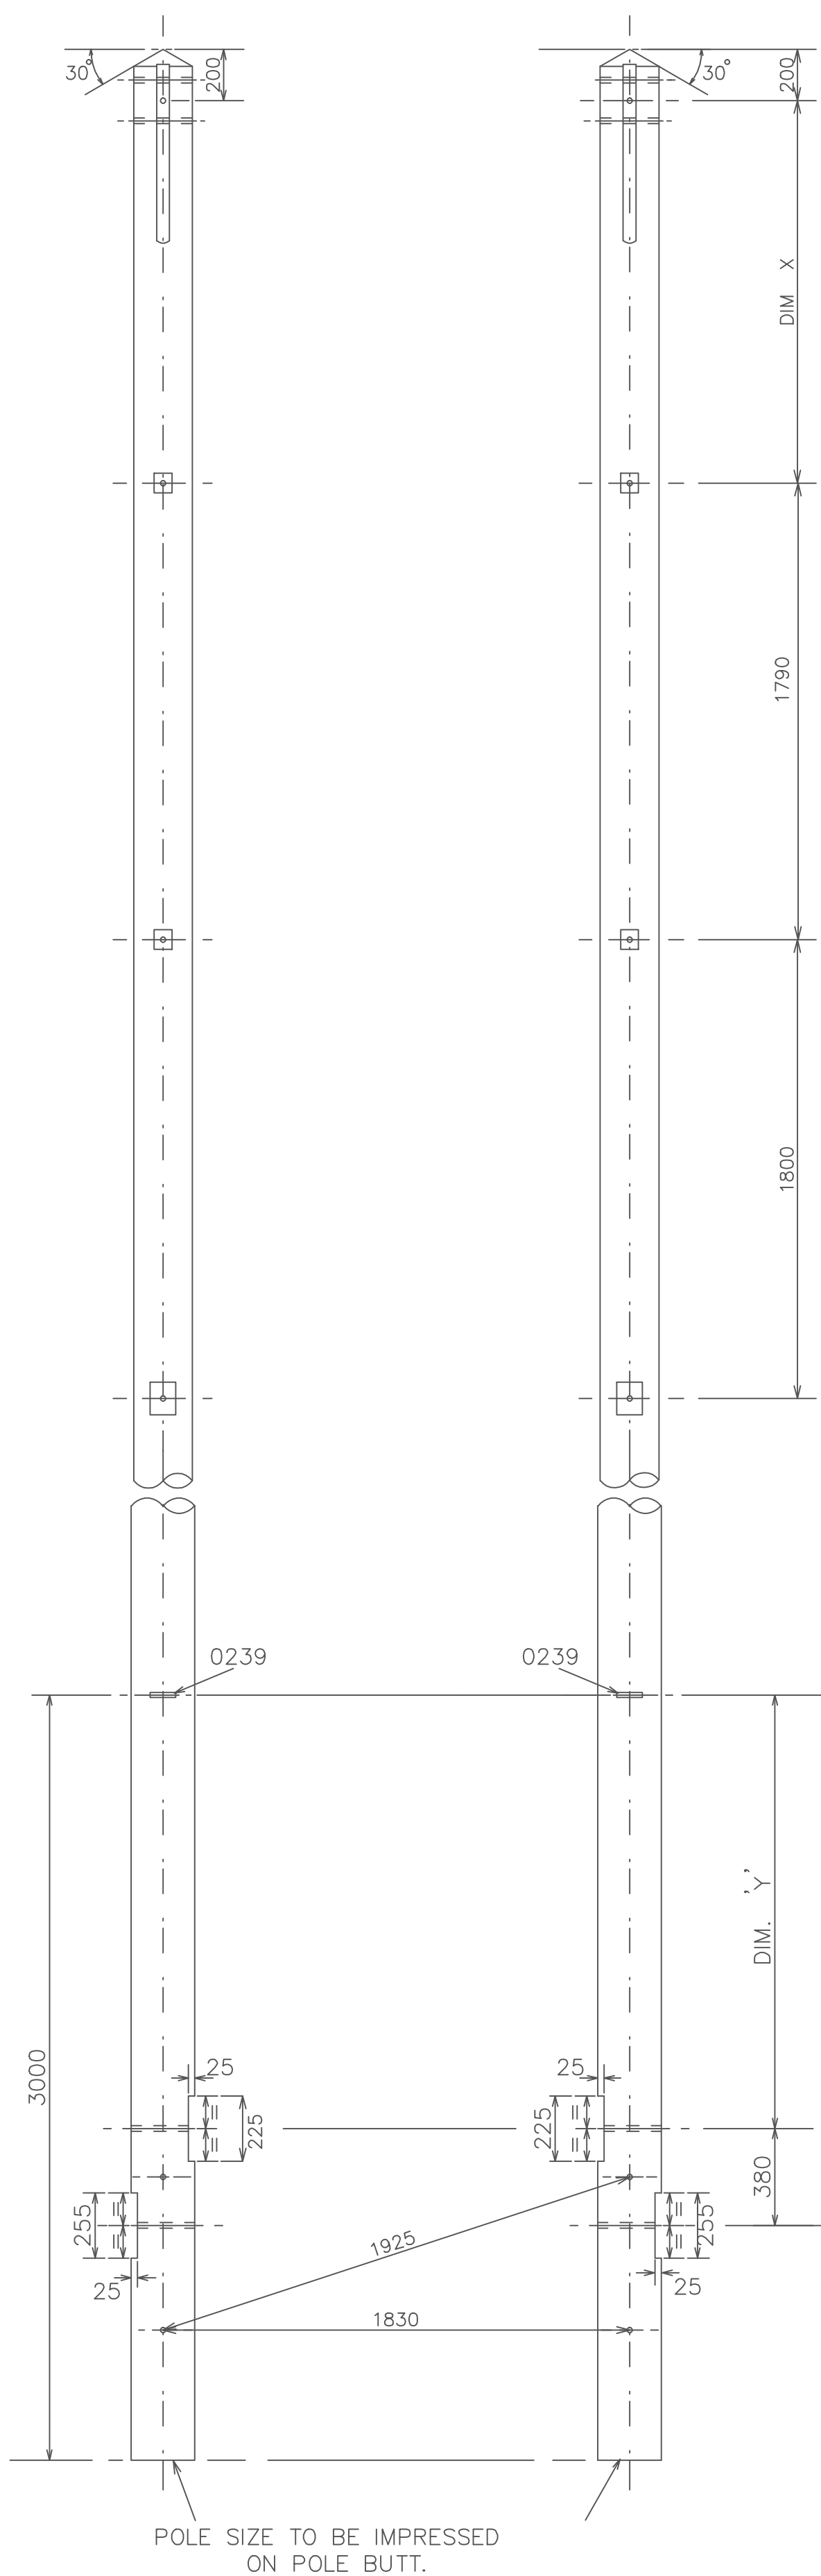
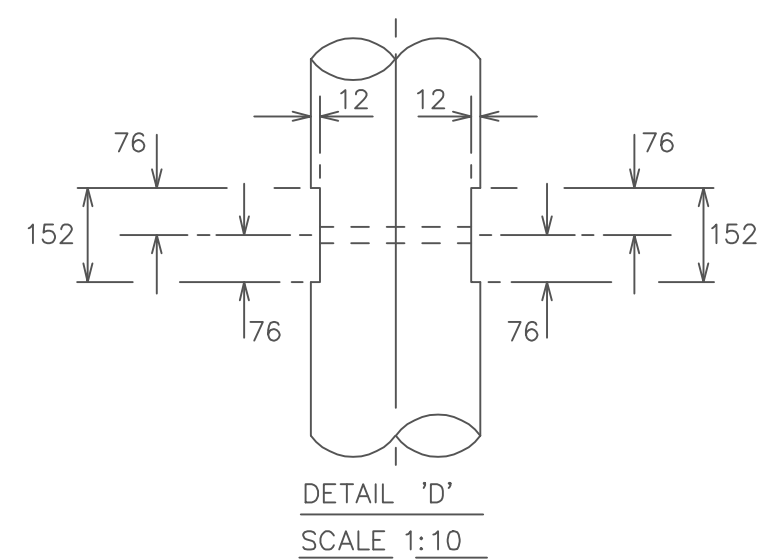
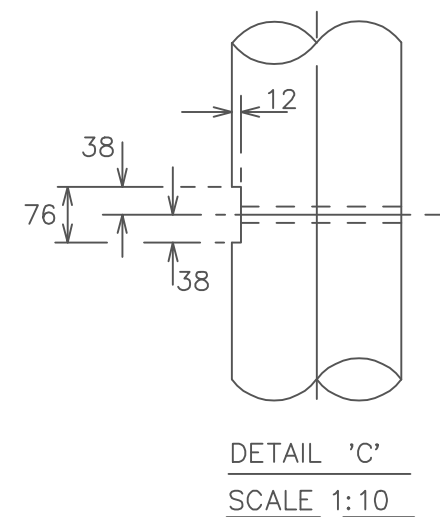
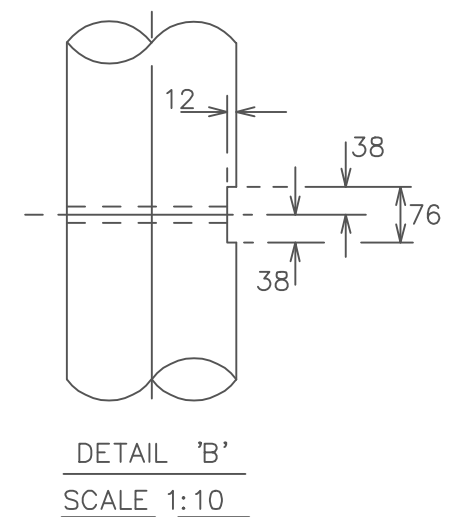


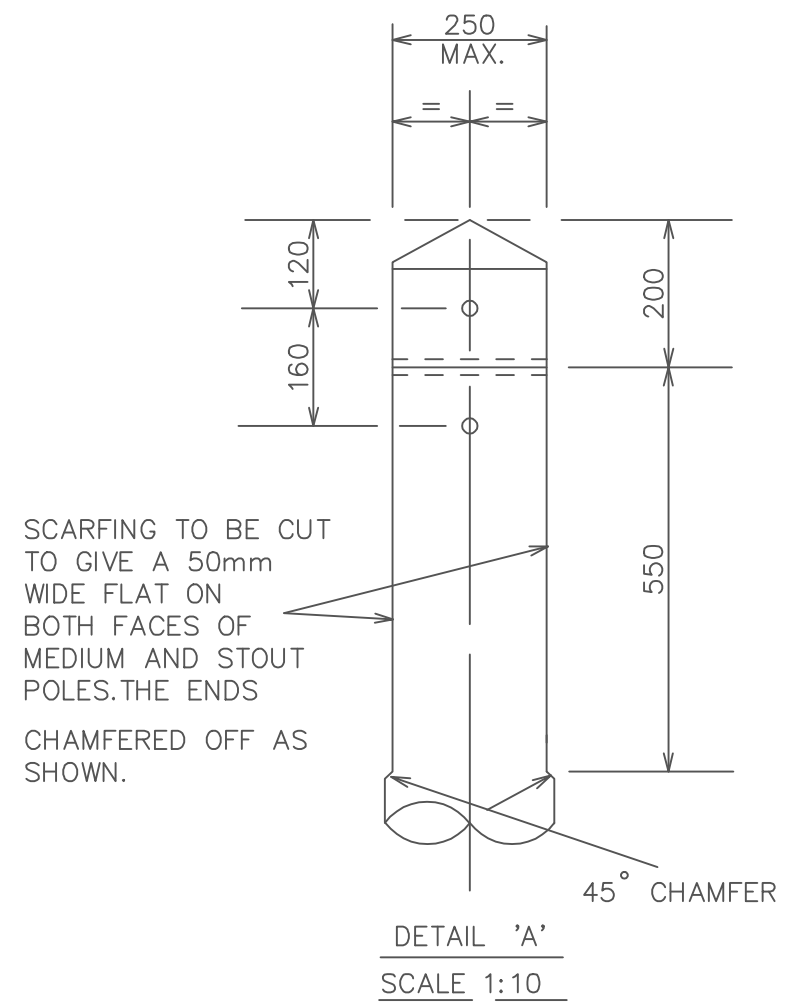

POLE LENGTH. (m)	DIM. 'Y' (mm)	DIM. 'X' (mm)
11.0	1900	1500
12.0	1400	2200

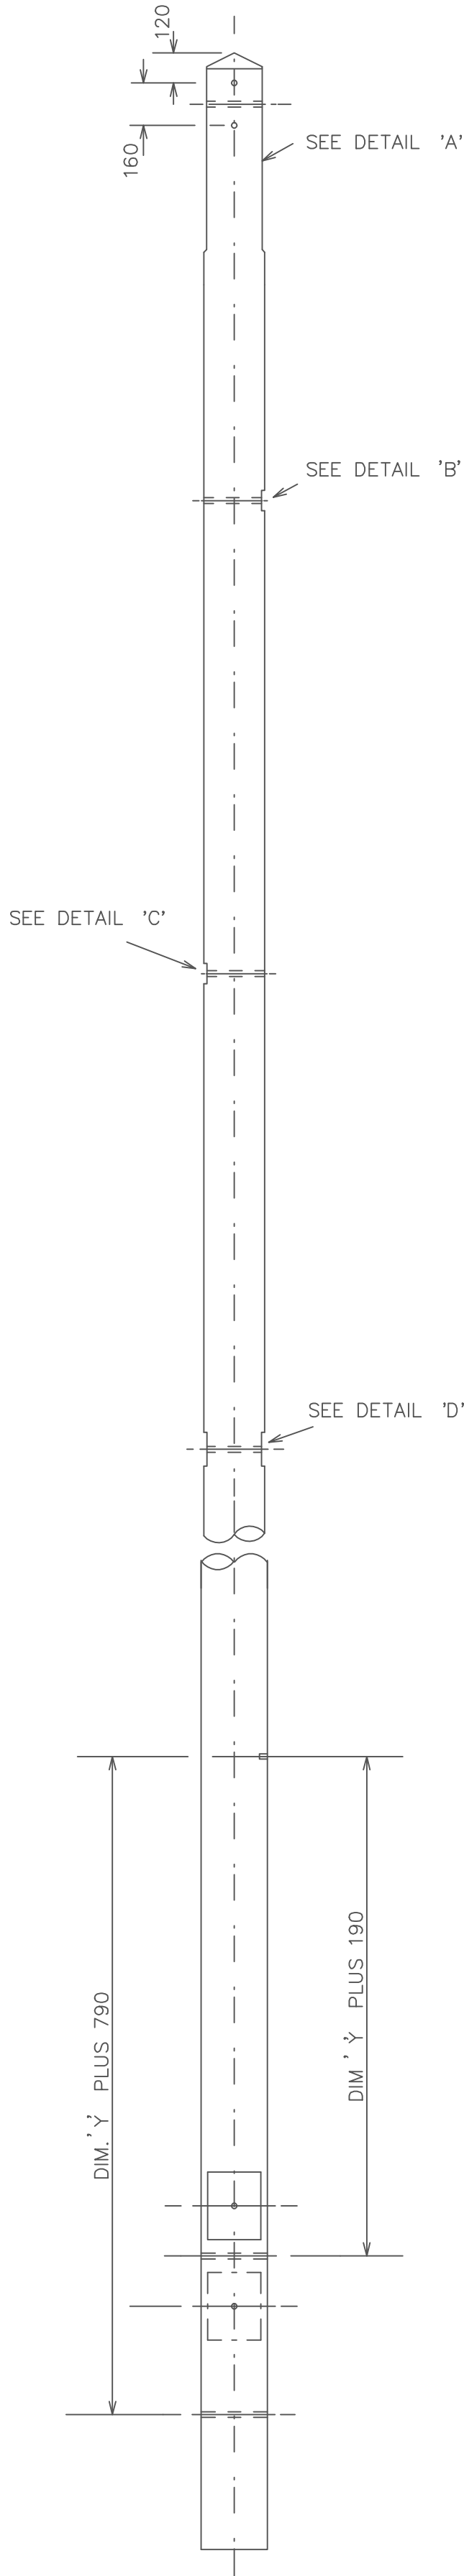

NOTES:

1. CLASS OF POLE TO BE 'STOUT.'
2. 'STOUT' CLASS POLES TO HAVE MINIMUM DIA. OF 210mm AT TOP.
3. POLES TO BE MATCHED.
4. ALL HOLES TO BE 22mm DIA. DRILLED AT RIGHT ANGLES TO VERTICAL CENTRE LINE OF POLE. ALL DRILLING AND CUTTING TO BE DONE STRICTLY TO TEMPLATE PRIOR TO PRESERVATION TREATMENT.
5. POLE BUTT TO BE CUT AT RIGHT ANGLES TO AXIS OF POLE.
6. POLE TO BE NOTCHED AND DRILLED FOR DUPLICATE 250 x 125 BAULKS.

		Lloyds Court, 78, Grey Street, Newcastle Upon Tyne, NE1 6AF										
		20kV OVERHEAD LINES 'H' POLE FABRICATION FOR DRAWING No.1.09.108.0860 SHEET 5										
Prepared by	J.B.	Drg.No.	1 09 108 0860								Sheet No.	6
Checked	M.W.	Date Issued	MAR'93								Revised	MAY 05
Mod.		A B C								Scale		1:20 & 1:10