
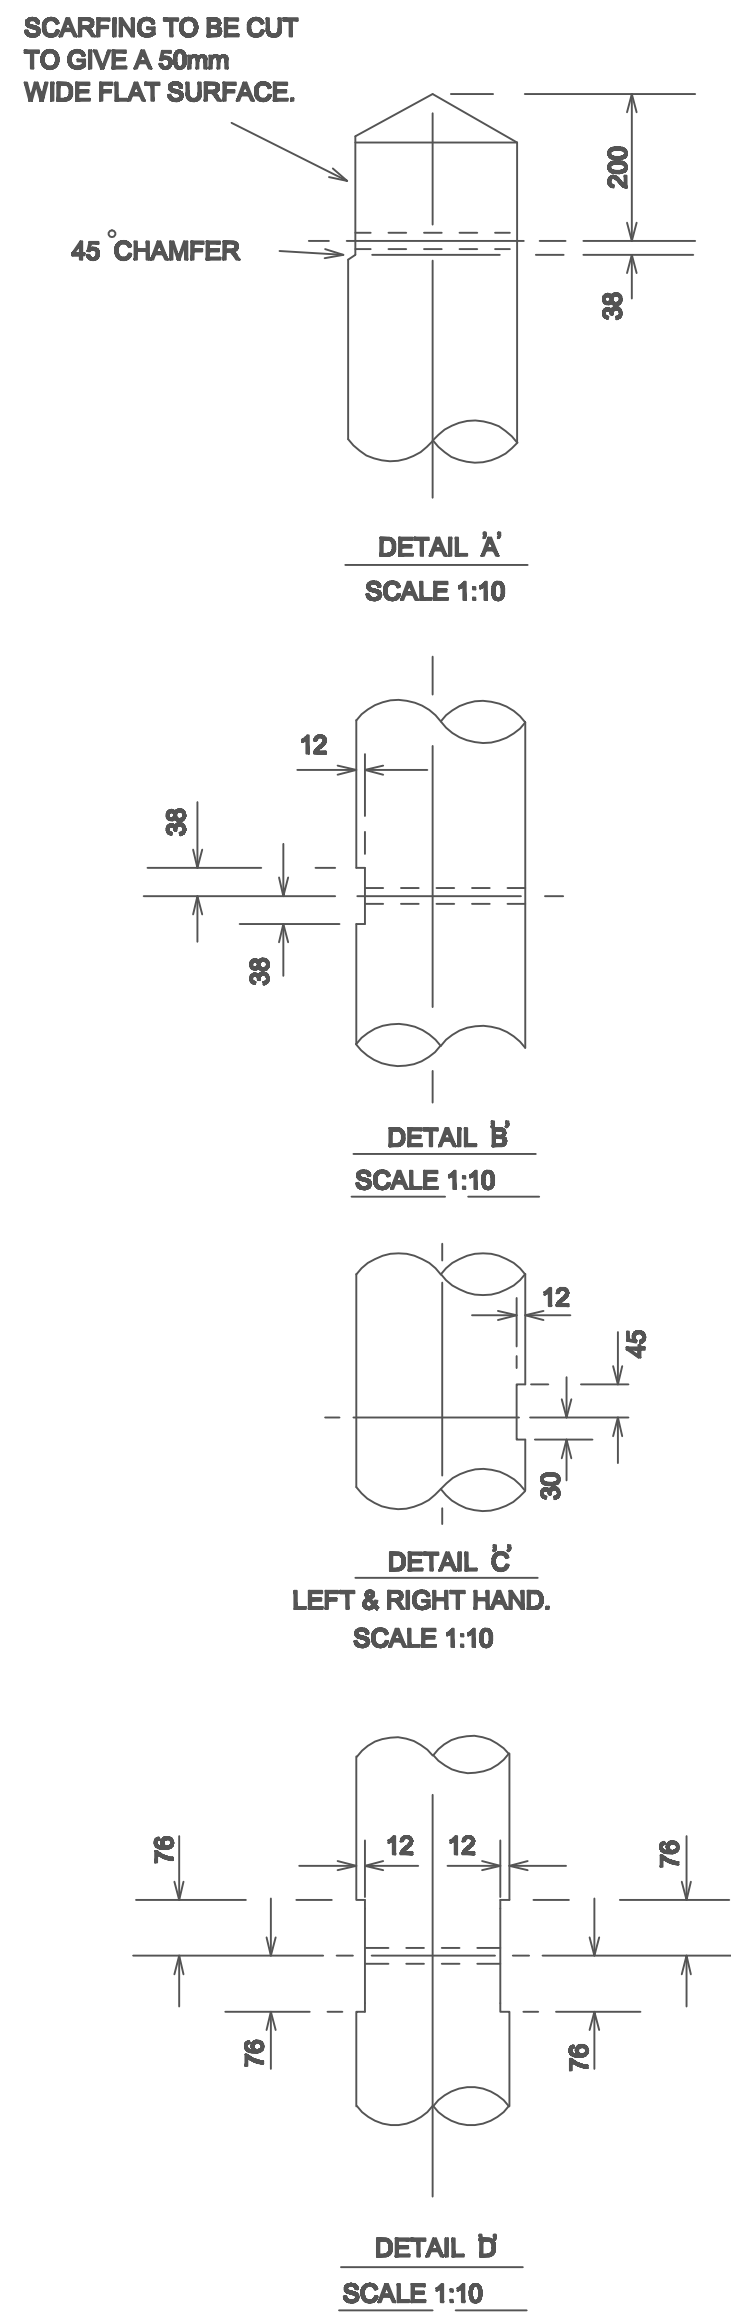
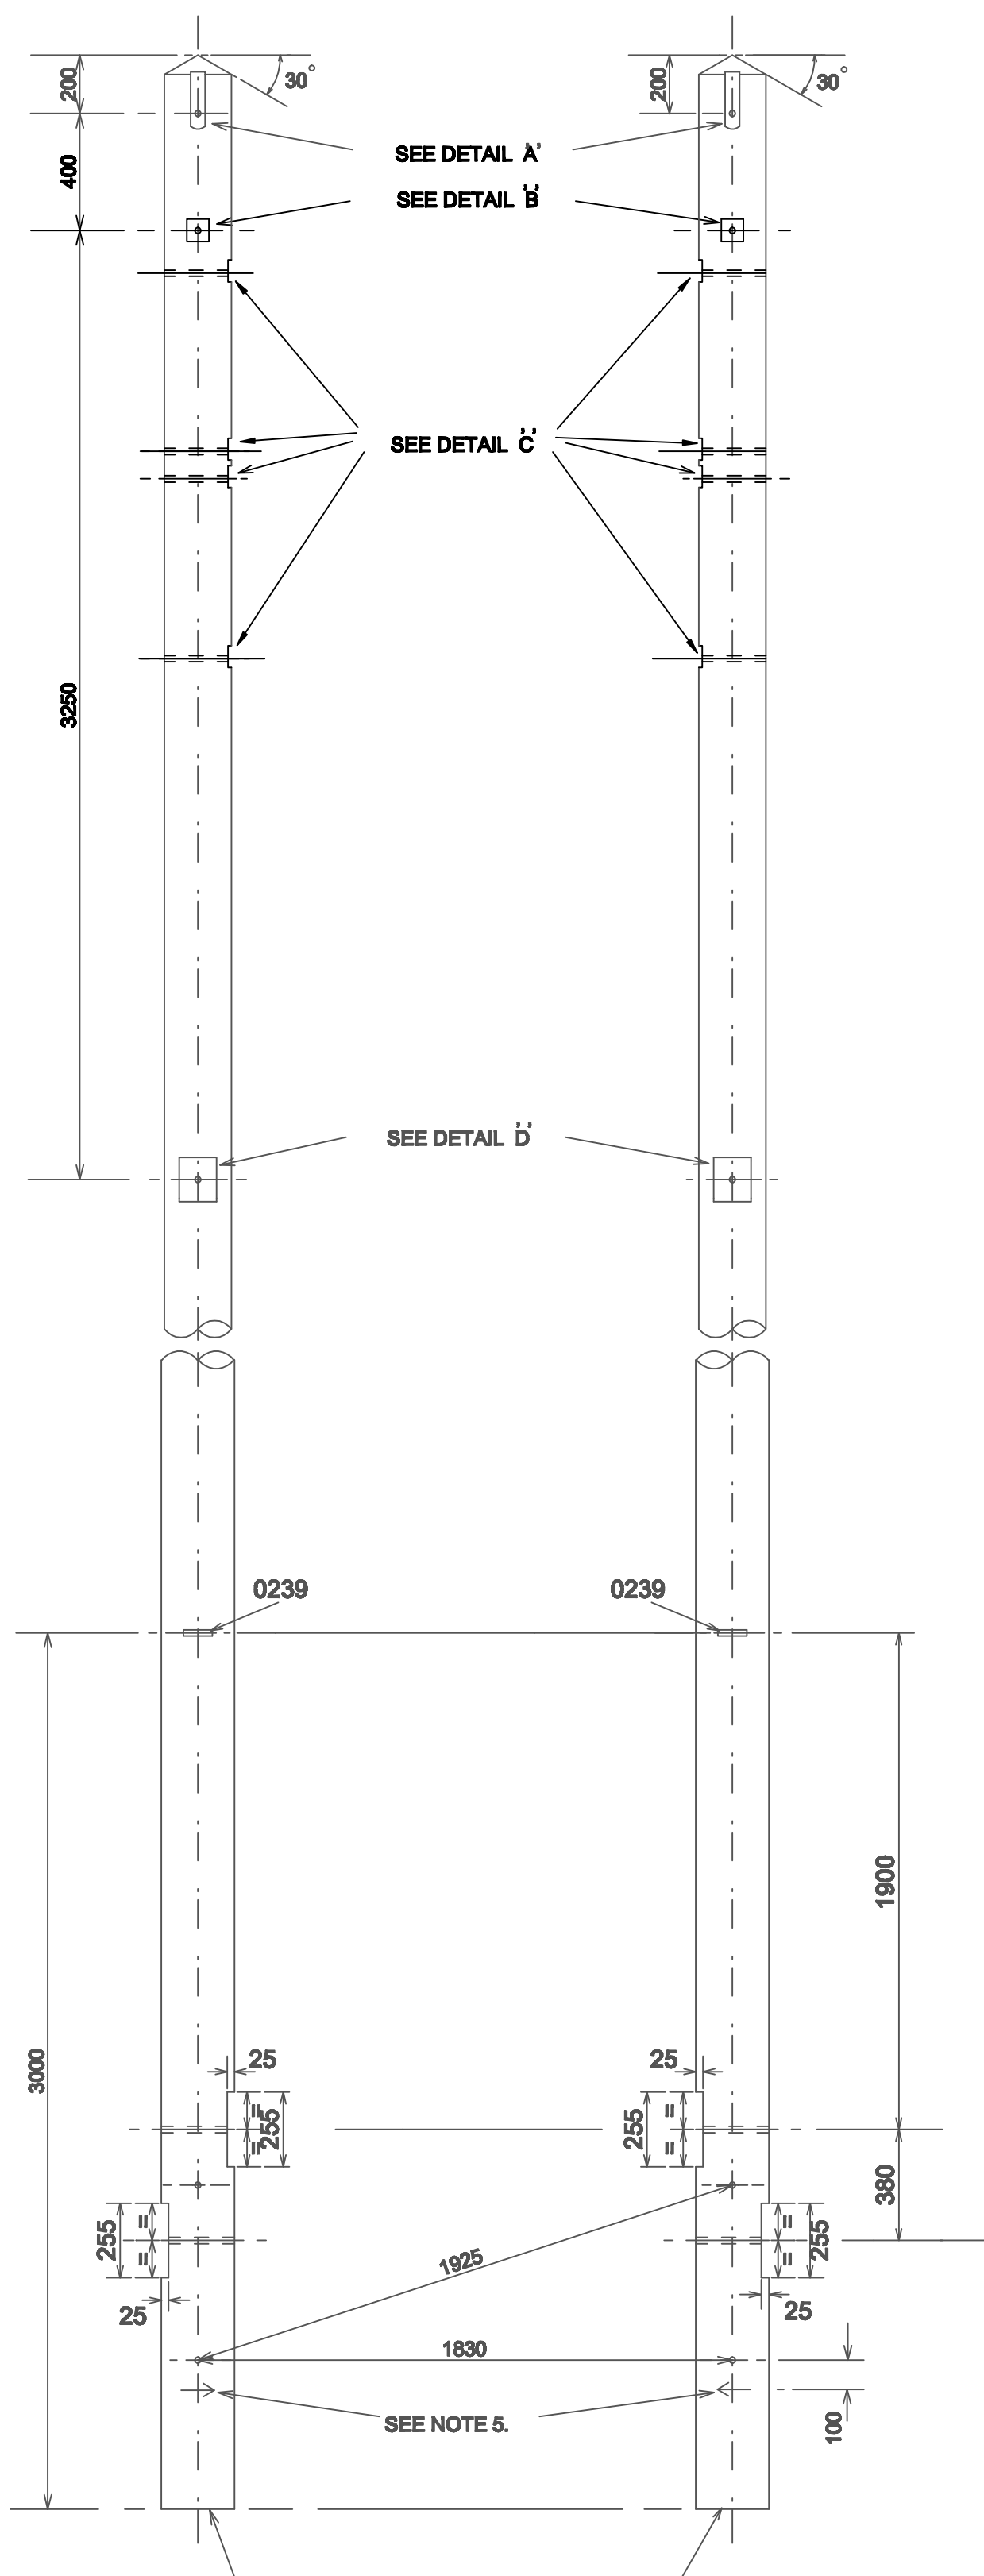


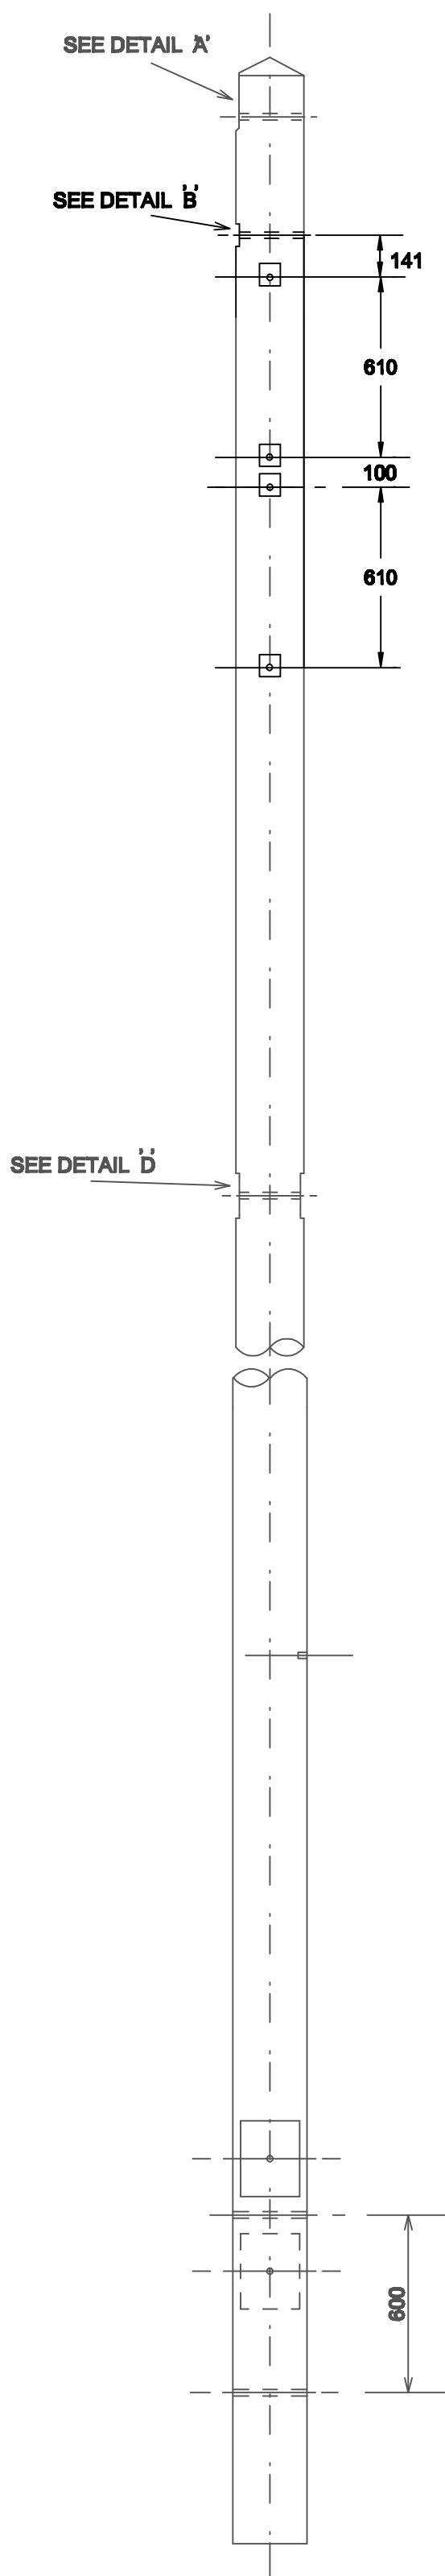

NOTES:

- POLE LENGTH 11.0m OF STOUT CLASSIFICATION WITH MINIMUM POLE TOP DIAMETER OF 175mm.
- POLE LEGS TO BE MATCHED.
- ALL HOLES TO BE 22mm DIA. DRILLED AT RIGHT ANGLES TO VERTICAL CENTRE LINE OF POLE.
- POLE TO BE NOTCHED AND DRILLED FOR 4 X 250 X 125 X 850 BAULKS.
- 50 X 6 X 6 DEEP ARROW MARK POINTING TOWARDS OPPOSITE POLE LEG, TO BE MARKED ON THE POLE FACE.

POLE SIZE TO BE IMPRESSED ON POLE BUTT.

ALL DIMENSIONS SHOWN ARE IN MILLIMETRES UNLESS OTHERWISE STATED.

		Lloyds Court, 78, Grey Street, Newcastle upon Tyne NE1 6AF											
		11kV AND 20kV OVERHEAD LINE DRILLING, SCARFING AND MARKING FOR DRAWING No 1.09.108.0862 SHEET 1 AND 3											
Prepared by J.B.	Checked H.A.J.	Date issued FEB 77	Drg.No. 1 09 108 0862	Sheet No. 2									
			Scale 1:20 & 10										