


FIG. NUMBERS SUPPLIED	CAT. No.
FIG. 1	237505
FIG. 2	237613
FIG. 3	237473

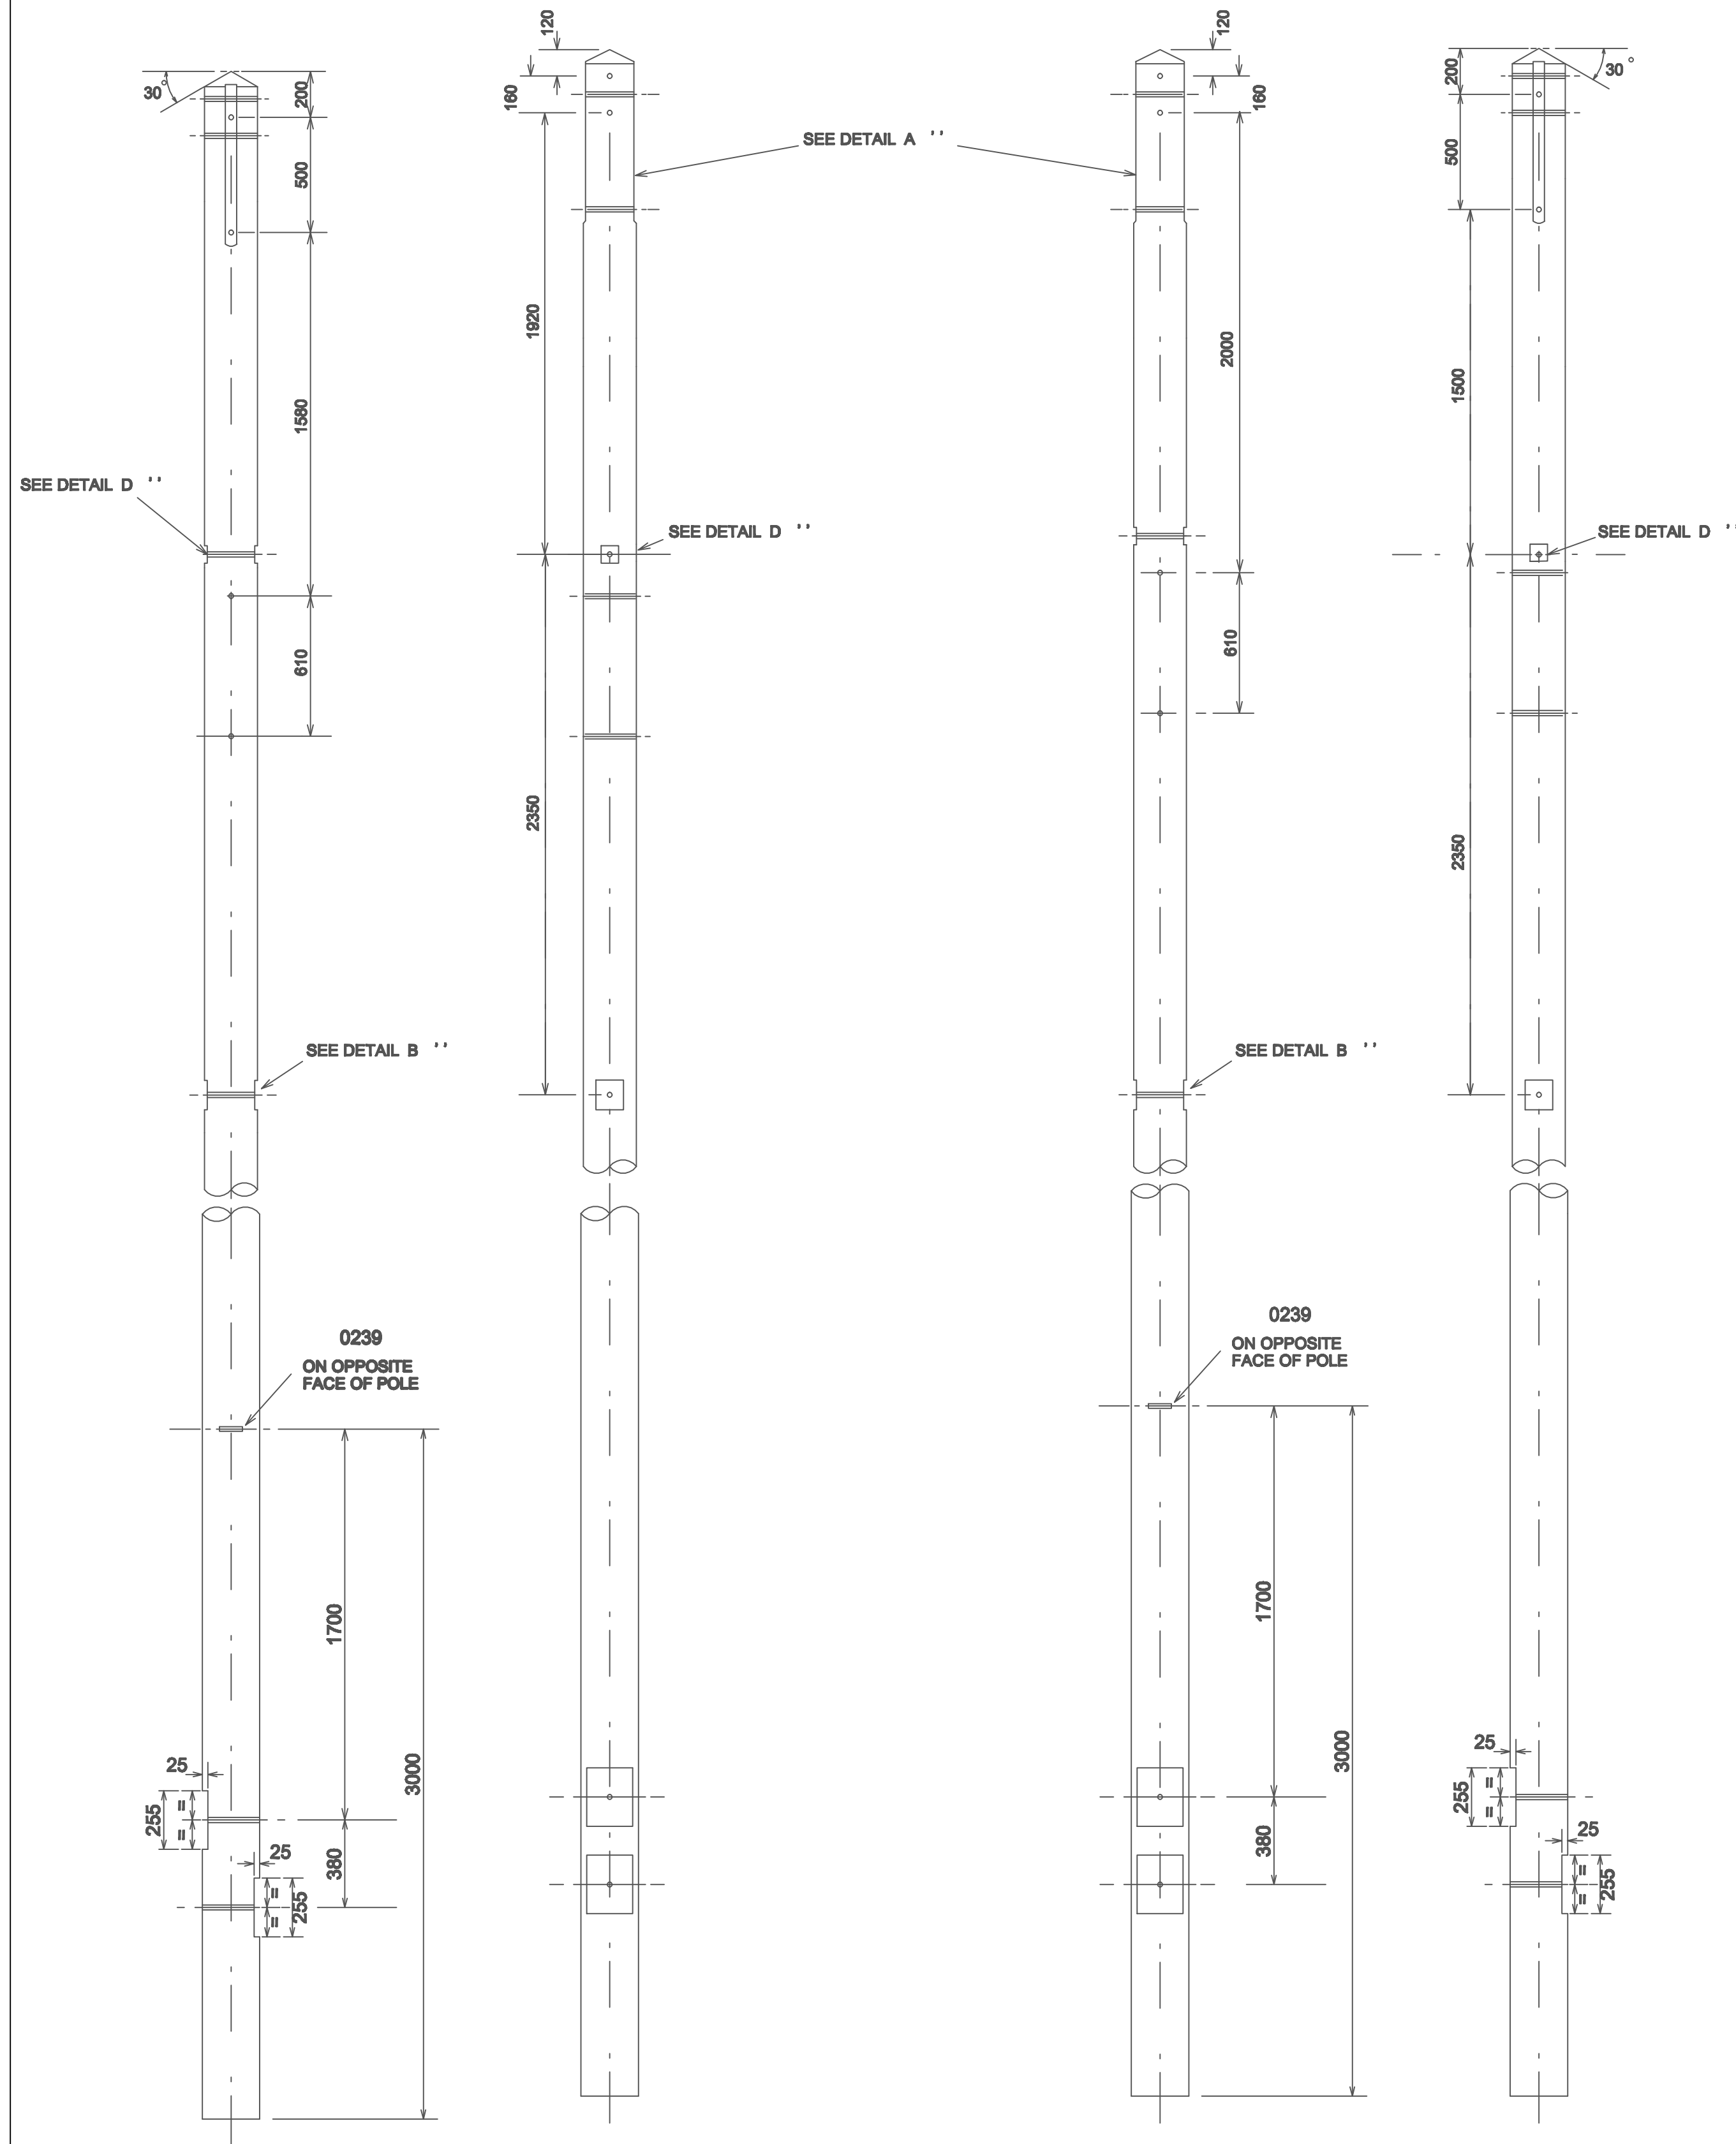


LONG LEG
0864 SHEET 1
FIG.1


LONG LEG
0864 SHEET 2
FIG.2

- NOTES:
- LONG LEG - POLE LENGTH 11.0m, CLASSIFIED STOUT.
SHORT LEG - POLE LENGTH 9.0m, CLASSIFIED STOUT.
 - WHEN COMPLETE POLE ARRANGEMENTS TO DRG.No s 0864 SHT.1 & 2 ARE REQUIRED, THE ORDERS SHALL QUOTE FABRICATION TO 1.09.108.0864 SHT.3 FIGS. 1 AND 3 OR 2 AND 3.
 - WHERE A SHORT LEG ONLY IS REQUIRED TO CONVERT EXISTING SINGLE POLE ARRANGEMENTS TO 0864 SHT.1 OR 2, THE ORDERS SHALL QUOTE FABRICATION TO 1.09.108.0864 SHT.3 FIG 3.
 - ALL HOLES SHALL BE 22mm DIA, DRILLED AT RIGHT ANGLES TO THE VERTICAL CENTRE LINE. ALL DRILLING AND CUTTING TO BE DONE STRICTLY TO TEMPLATE AND PRIOR TO CREOSOTING.
 - ALL UNUSED POLE BOLT HOLES TO BE PLUGGED.

STANDARD POLE LENGTHS

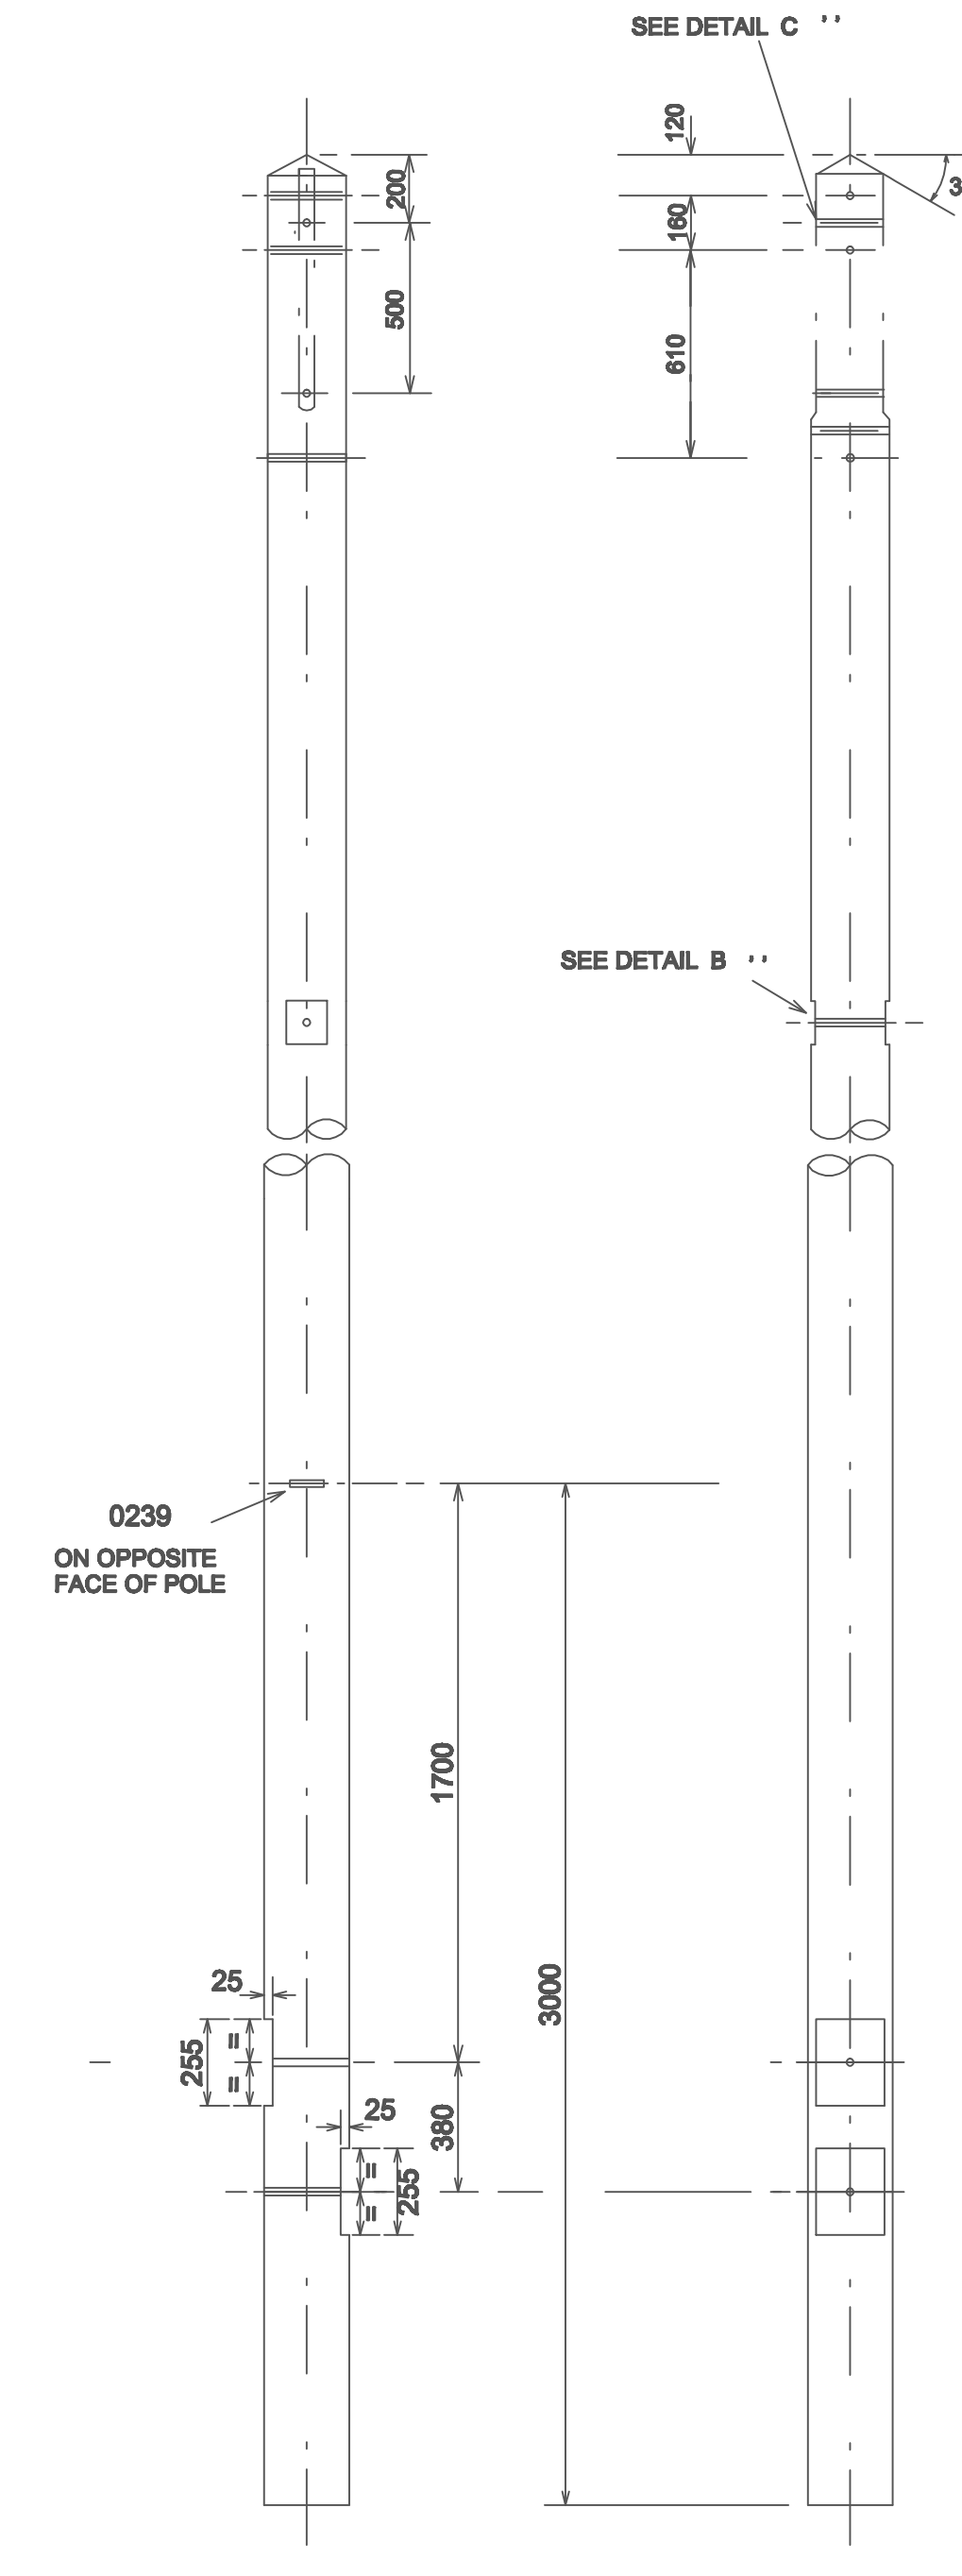

SHORT LEG
0864 SHEET 1 AND 2
FIG.3

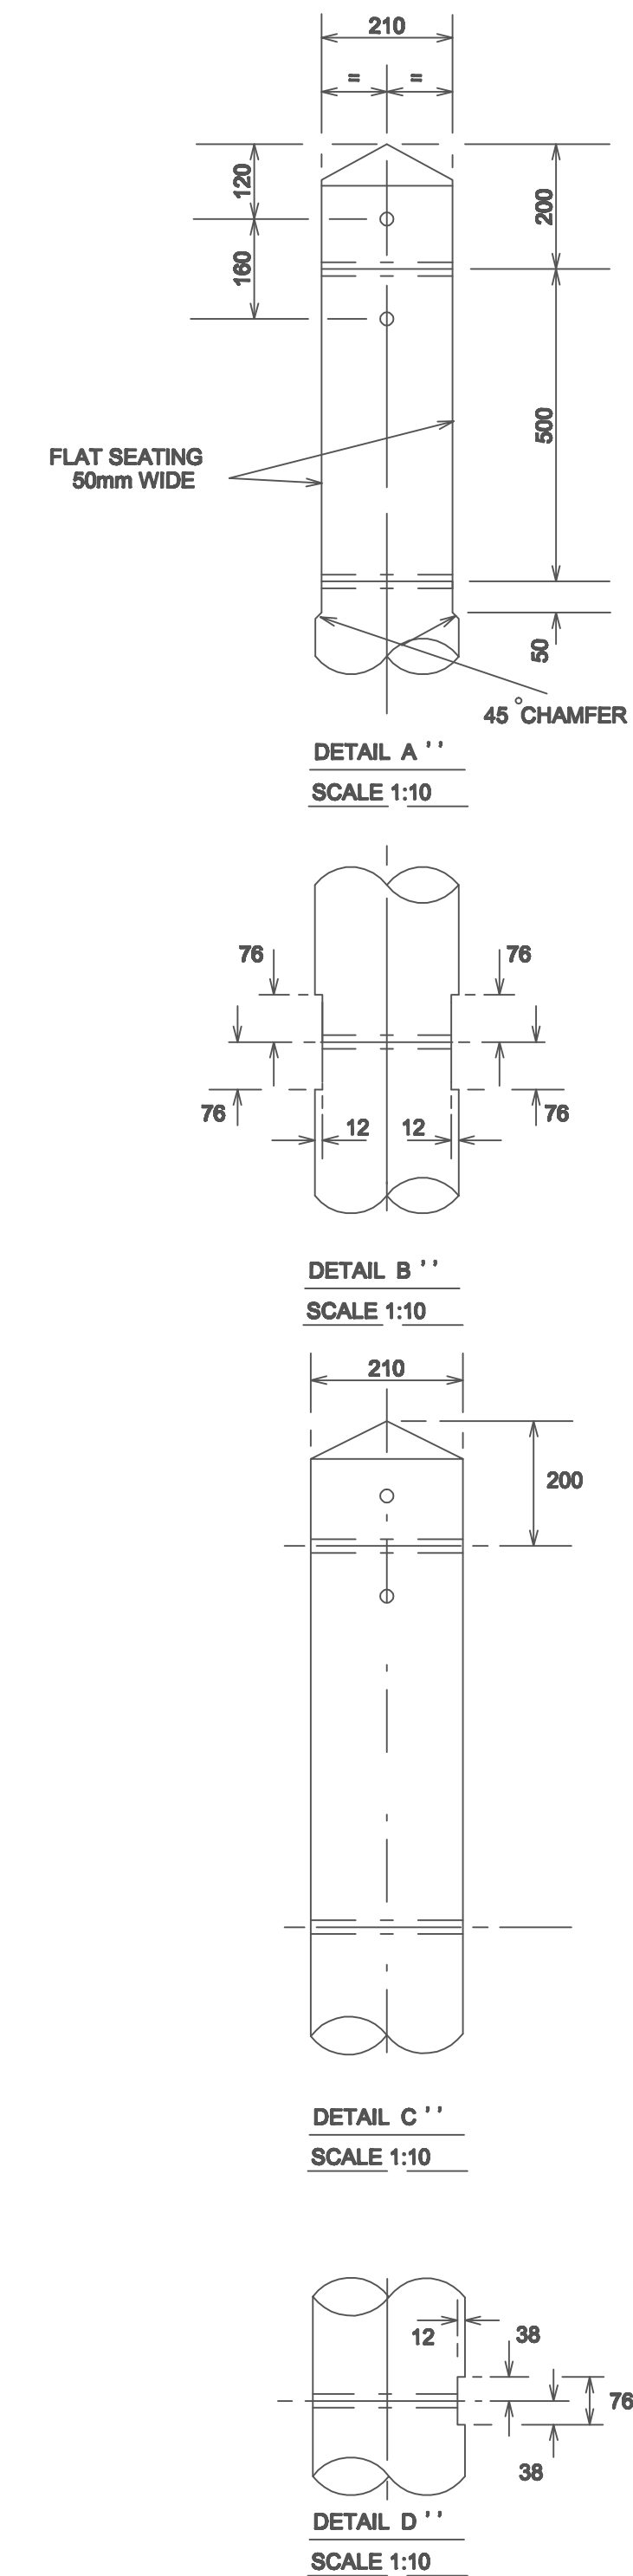

ALL DIMENSIONS SHOWN ARE IN MILLIMETRES UNLESS OTHERWISE STATED.

		Lloyds Court, 78, Grey Street, Newcastle Upon Tyne, NE1 6AF	
11 AND 20kV OVERHEAD LINES FABRICATION DETAILS FOR DRAWINGS 1.09.108.0864 SHEET 1 AND SHEET 2			
Prepared by J.B. Checked G.M.H.	Date Issued SEP'83	Drg.No. 1 09 108 0864	Sheet No. 3 Revised 23.2.2005 Scale 1:20
Mode. A B C D E F			