


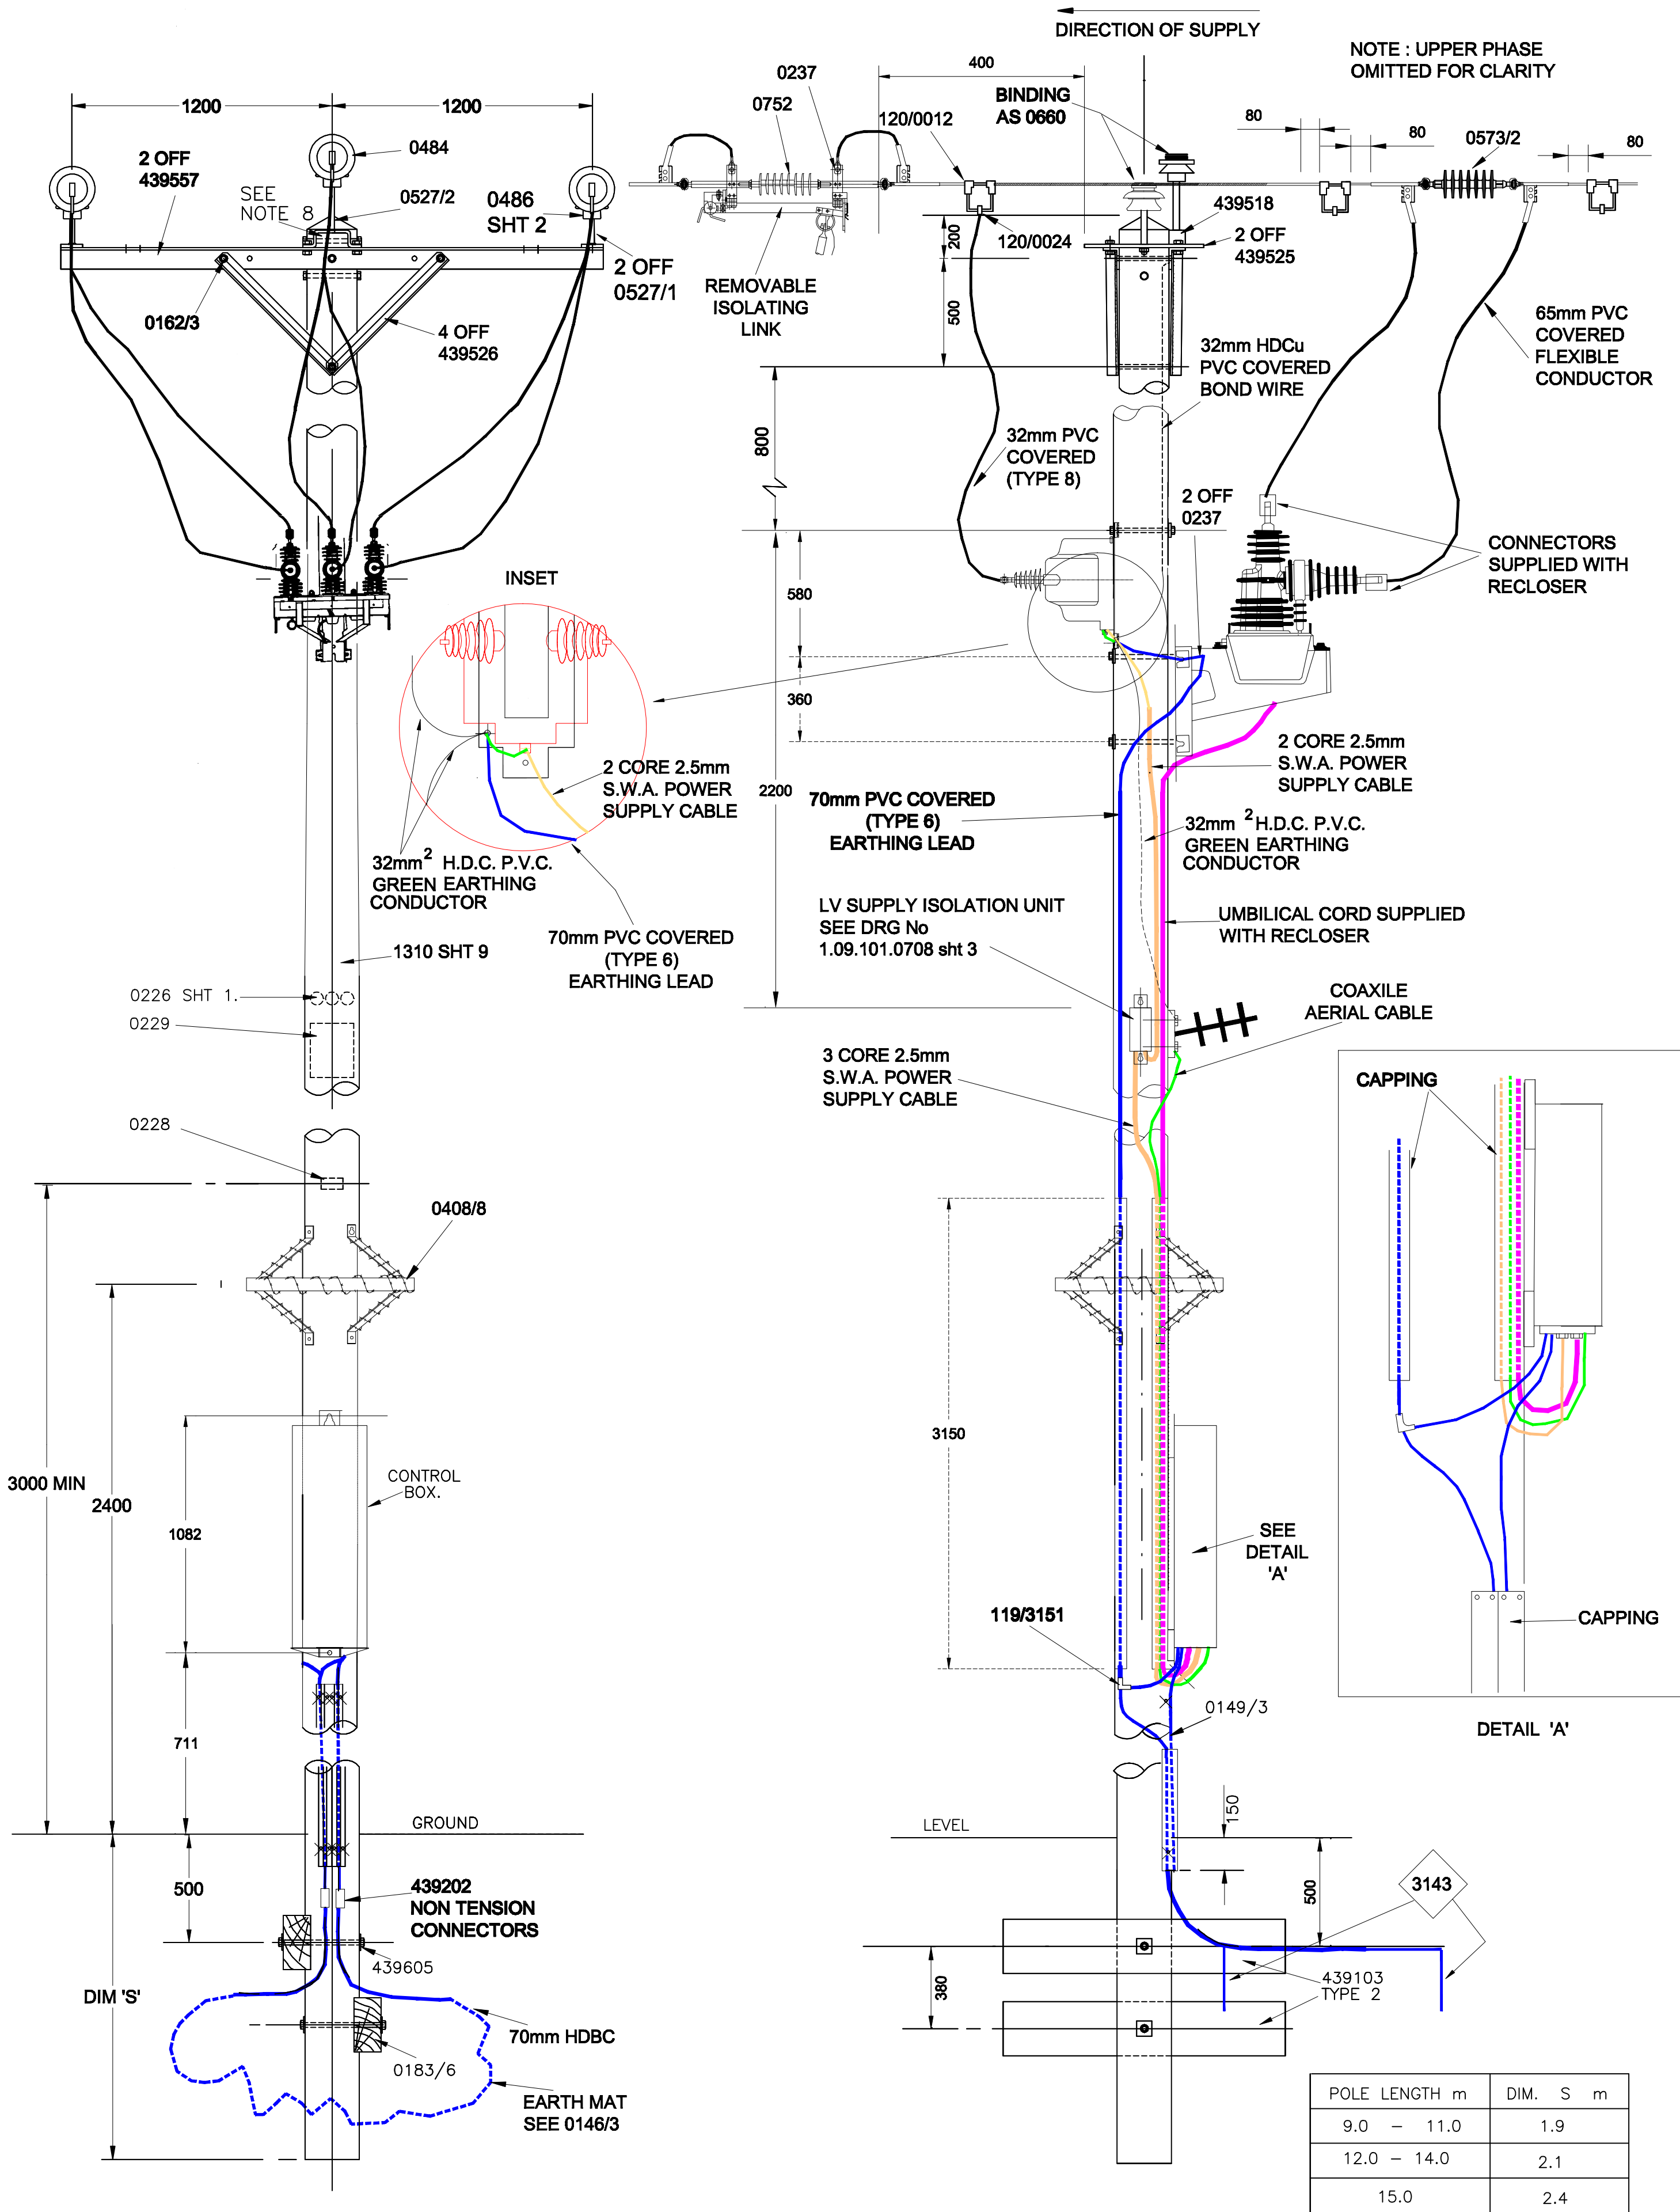

NOTES

1. ALL POLE BOLTS TO BE M20
2. DETAIL DRGS PREFIXED 443.... REFER TO ESI DRGS. OTHER DETAIL DRGS REFER TO 1.09.101. ... SERIES
3. SEE DRAWING NUMBER 1.09.101.0144 SHEET 3 FOR DETAILS OF EARTHING

ALL DIMENSIONS SHOWN ARE IN MILLIMETRES UNLESS OTHERWISE STATED

CE Electric UK		Lloyds Court, 78 Grey Street, Newcastle Upon Tyne, NE1 6AF	
Manufacturer Details		11/20KV OVERHEAD LINES ARRANGEMENT OF AUTO-RECLOSER (NELEC 'U' SERIES) ON SINGLE INTERMEDIATE POLE C/W CAST RESIN VT	
Sheet No. 10	Scale 1:20	Type OVERHEAD	
Prepared By Janis.Webb		Ref No. C101738	Historic Drg.No. 1091091310
Revised 29/03/06	Grid Reference	Revision E Notes	
Date Issued	Checked By G HAMMEL		