


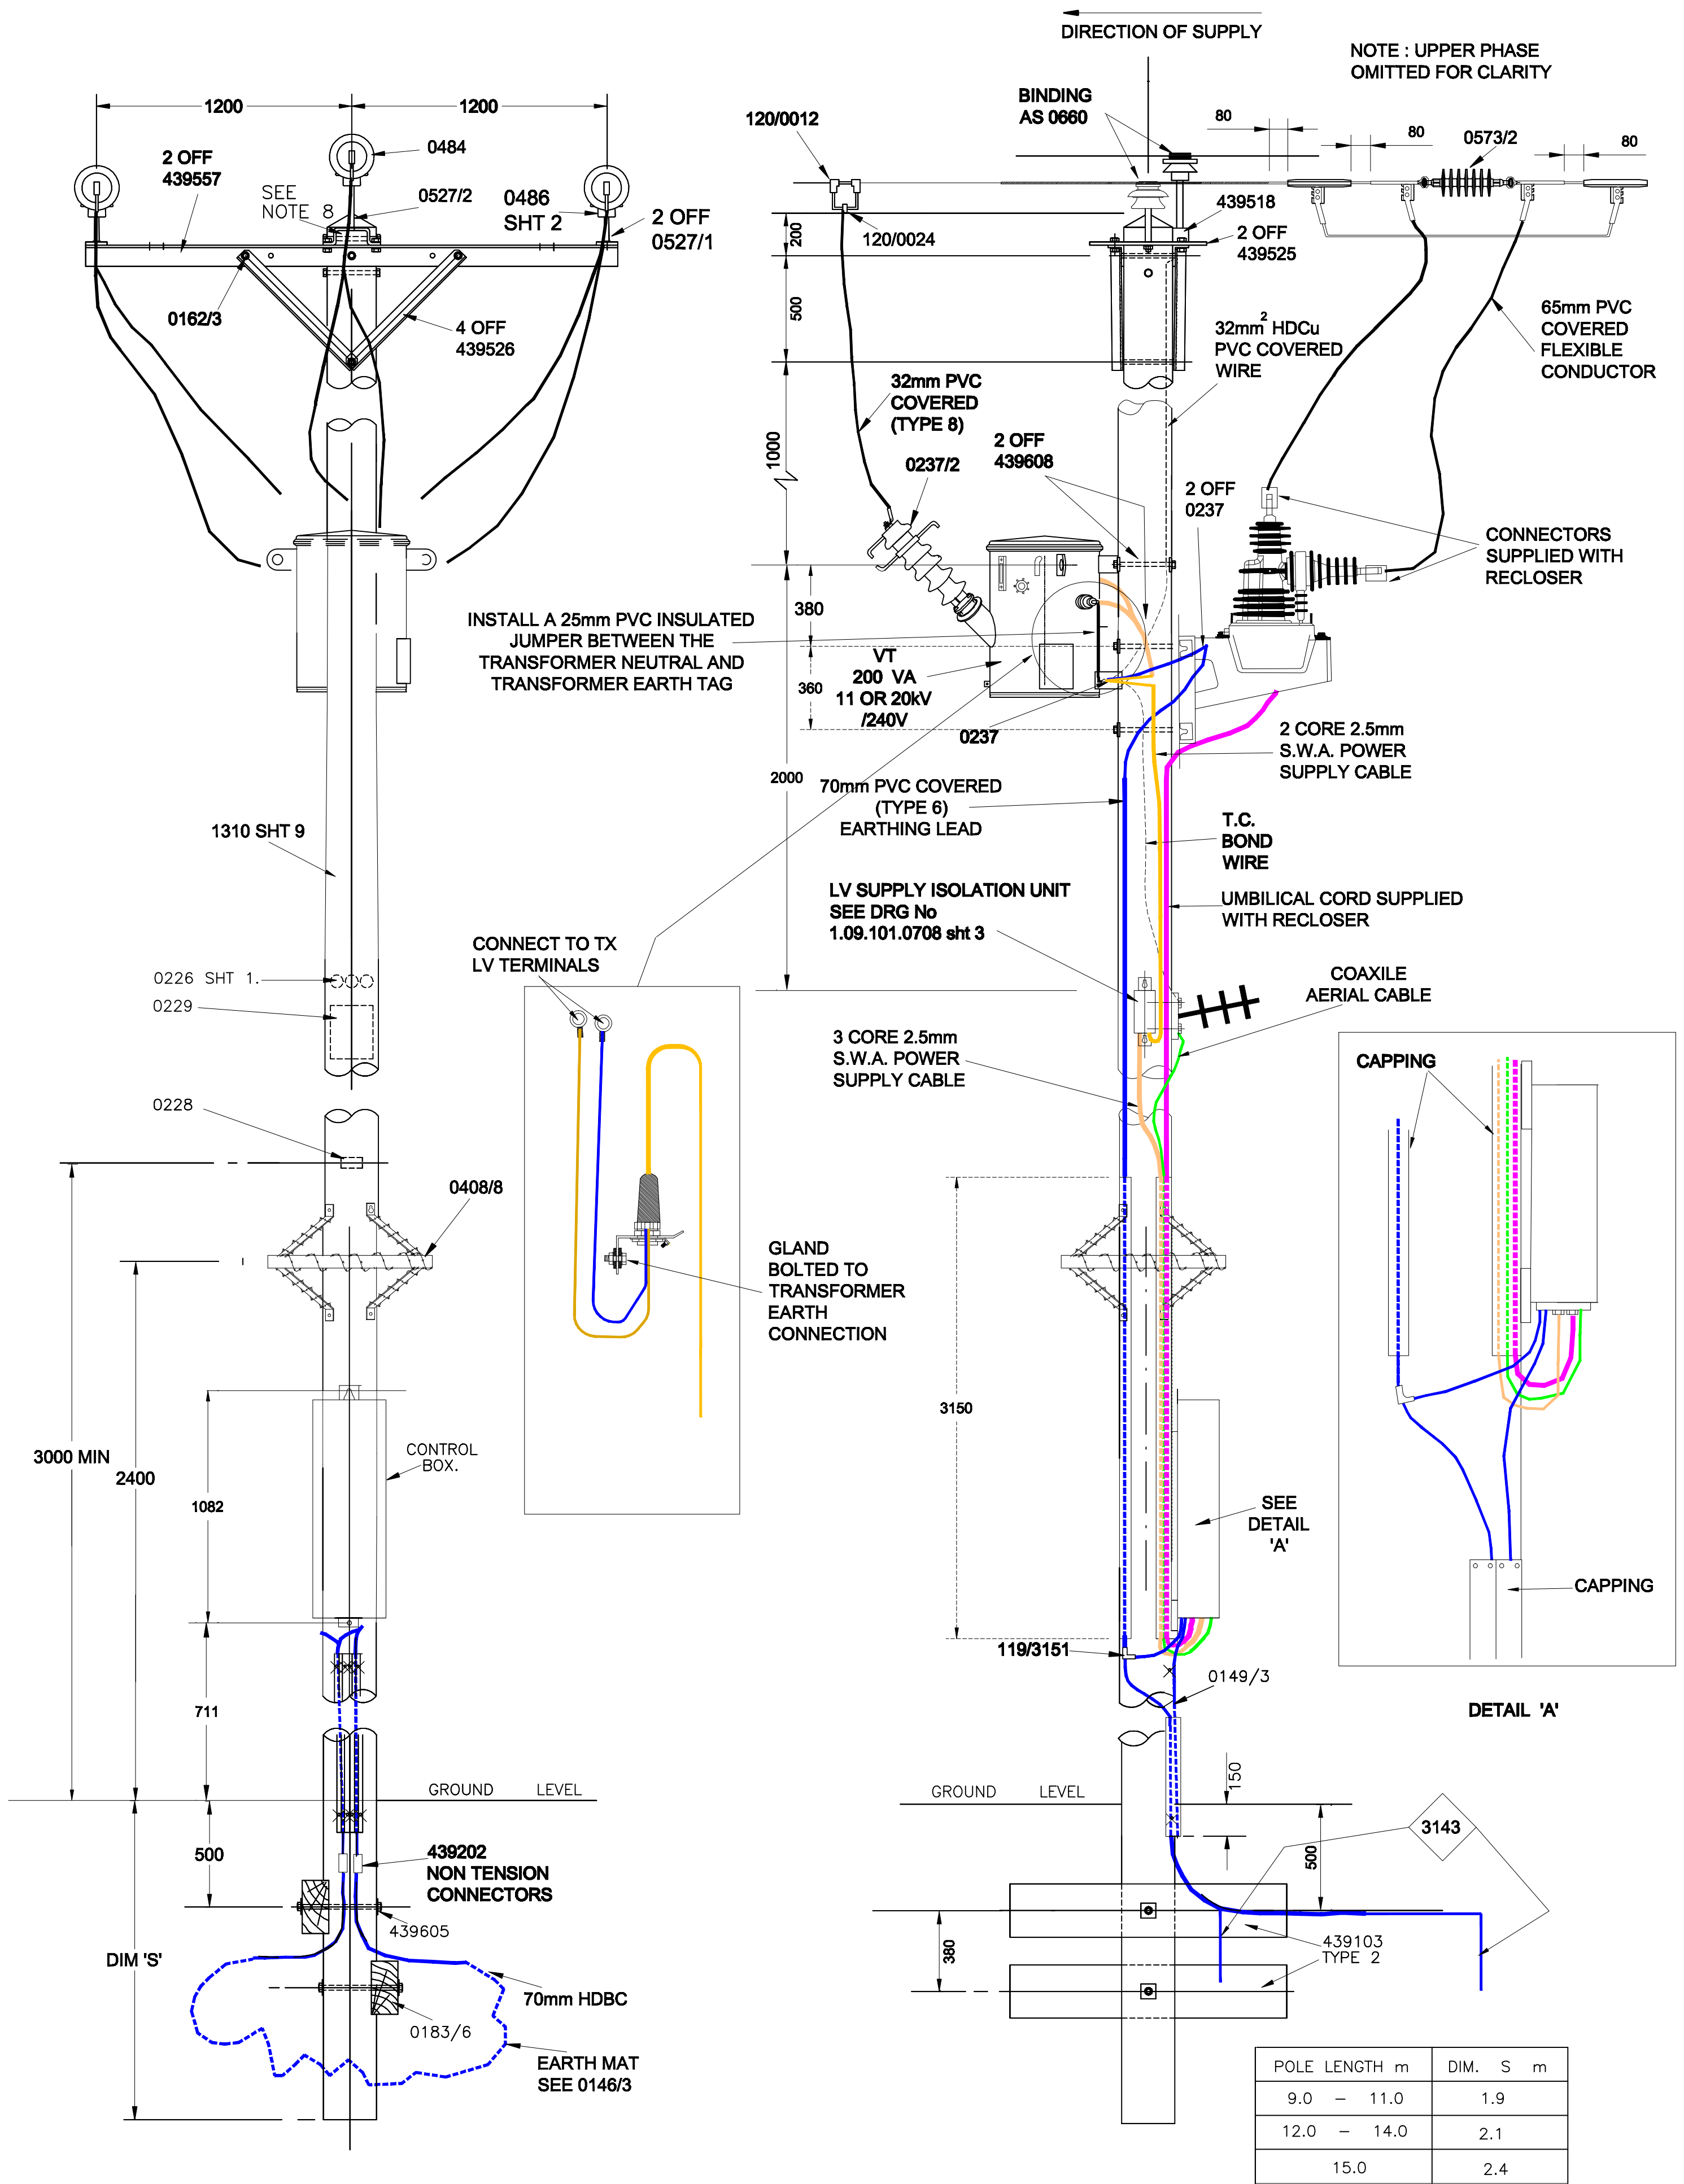

		Lloyds Court, 78 Grey Street, Newcastle Upon Tyne, NE1 6AF	
CE Electric UK Manufacturer Details		11/20kV OVERHEAD LINES ARRANGEMENT OF AUTO RECLOSER (NULEC 'U' SERIES) ON SINGLE INTERMEDIATE POLE	
Sheet No. 7	Scale 1:20	Type OVERHEAD	
Prepared By Barbara Simpson		Ref No. C101745	Historic Drg.No. 1091091310
Revised 20/03/06	Grid Reference	Revision D Notes	
Date Issued 01/02/02	Checked By G HAMMEL		