

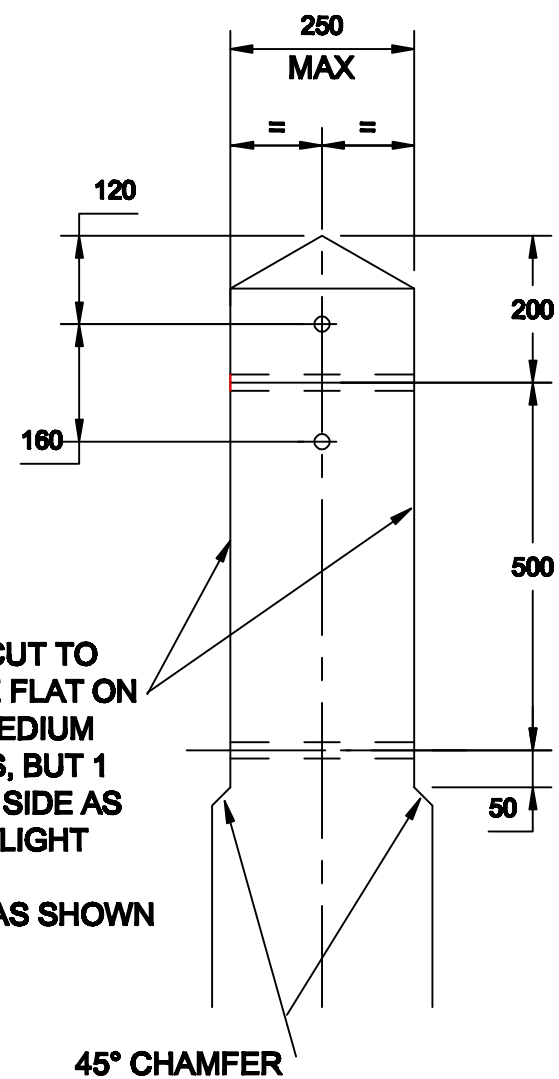
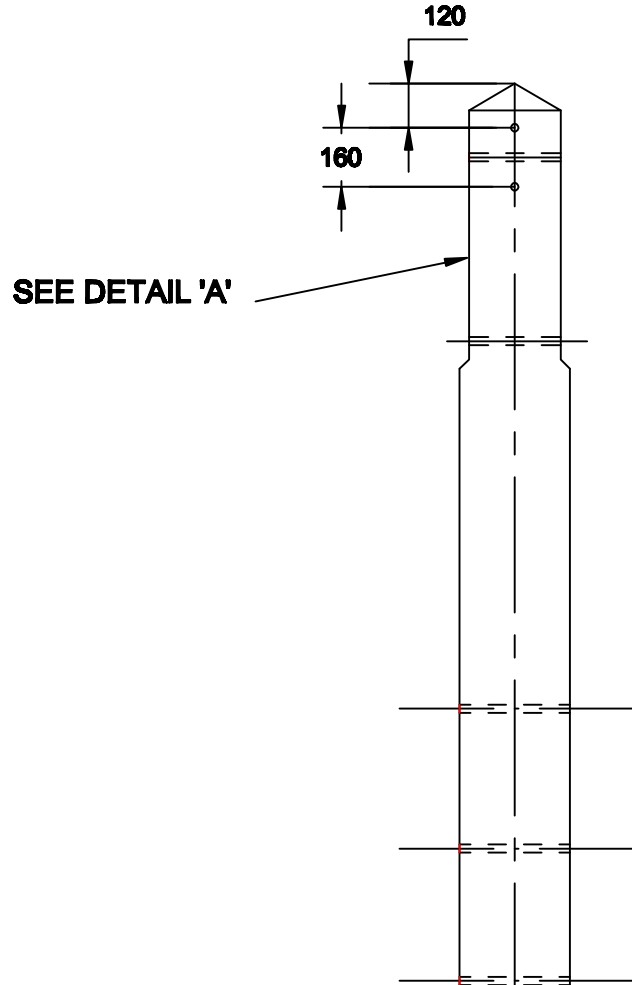
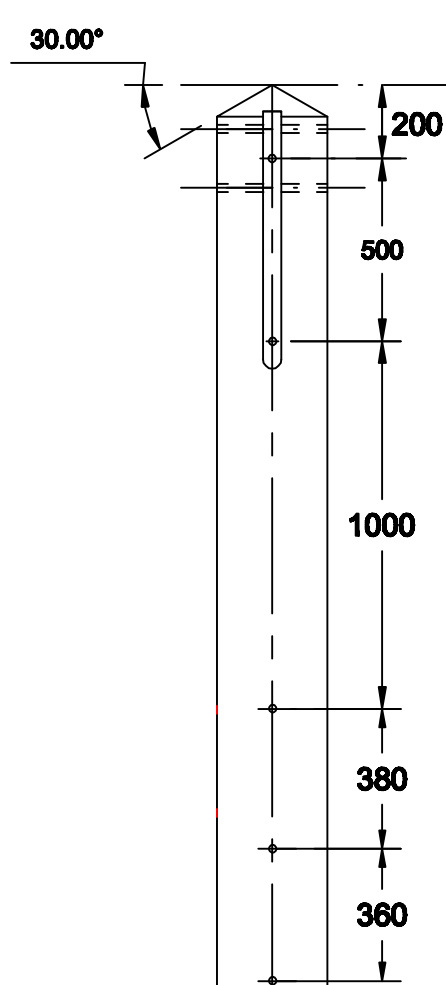


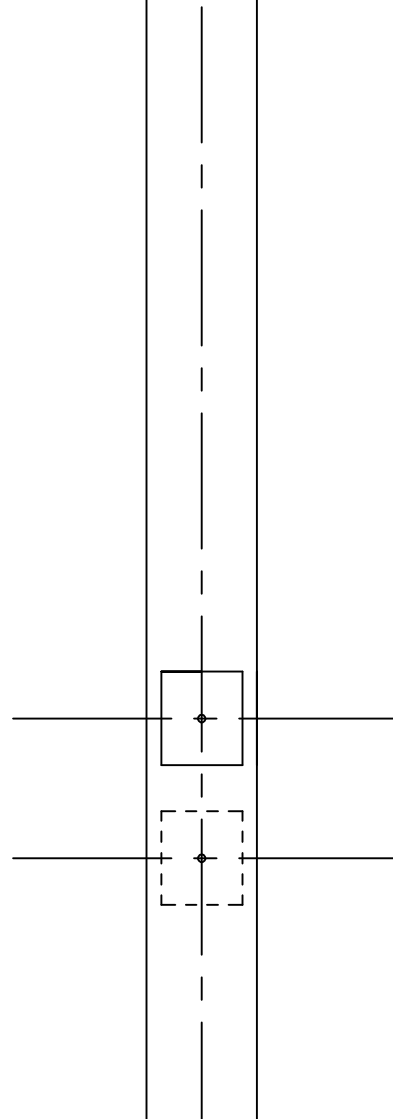

DETAIL 'A'
SCALE 1:10

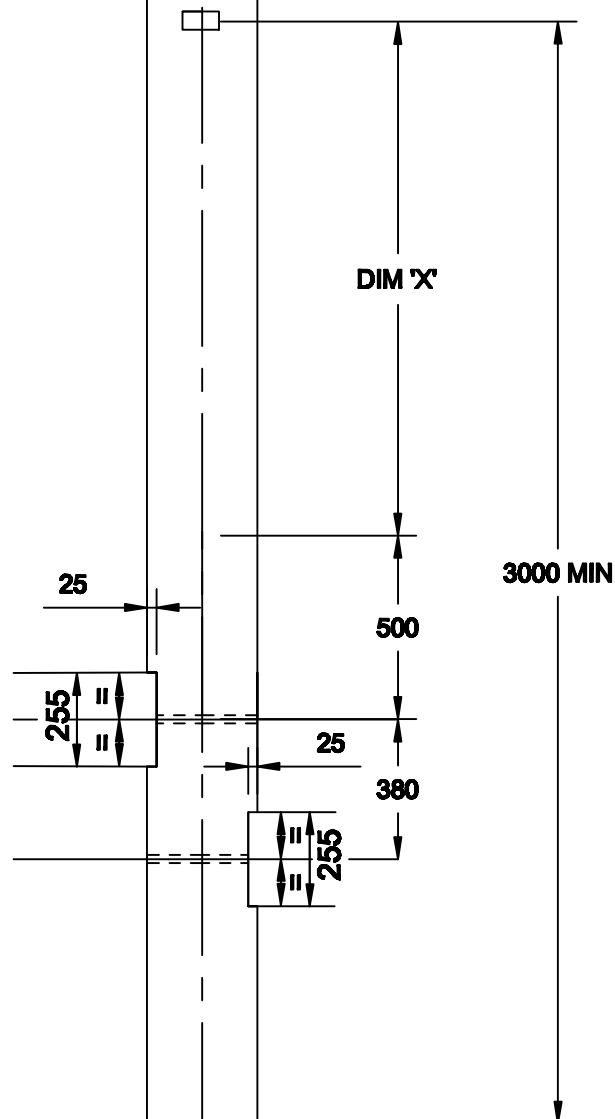

POLE SIZE TO BE IMPRESSED
ON POLE BUTT

NOTES

1. CLASS OF POLE TO BE 'STOUT ONLY'
2. ALL HOLES TO BE 22mm DIA. DRILLED AT RIGHT ANGLES TO VERTICAL CENTRE LINE OF POLE. ALL DRILLING AND CUTTING TO BE DONE STRICTLY TO TEMPLATE PRIOR TO PRESERVATION TREATMENT.
3. POLE BUTT TO BE CUT AT RIGHT ANGLES TO AXIS OF POLE
4. POLE TO BE NOTCHED AND DRILLED FOR DUPLICATE 250 x 125 BAULKS

POLE LENGTH (m)	DIM 'X' (m)
9.5	1900
10.0	1900
10.5	1900
11.0	1900
11.5	1700

ALL DIMENSIONS SHOWN ARE IN MILLIMETRES UNLESS OTHERWISE STATED

NEDL		NEDL, Manor House, Station Road, Houghton le Spring, DH4 7LA.	
Prepared by J.L.W.		11/20kV OVERHEAD LINES	
Checked G.H.		DRILLING, SCARFING AND MARKING FOR AUTO-RECLOSER NULEC 'U' SERIES ON SINGLE INTERMEDIATE POLE	
Date issued 28.8.01		Drg.No. 1 09 109 1310	
Mod.		Sheet No. 9	
		Revised	
		Scale 1:20 (A2)	