
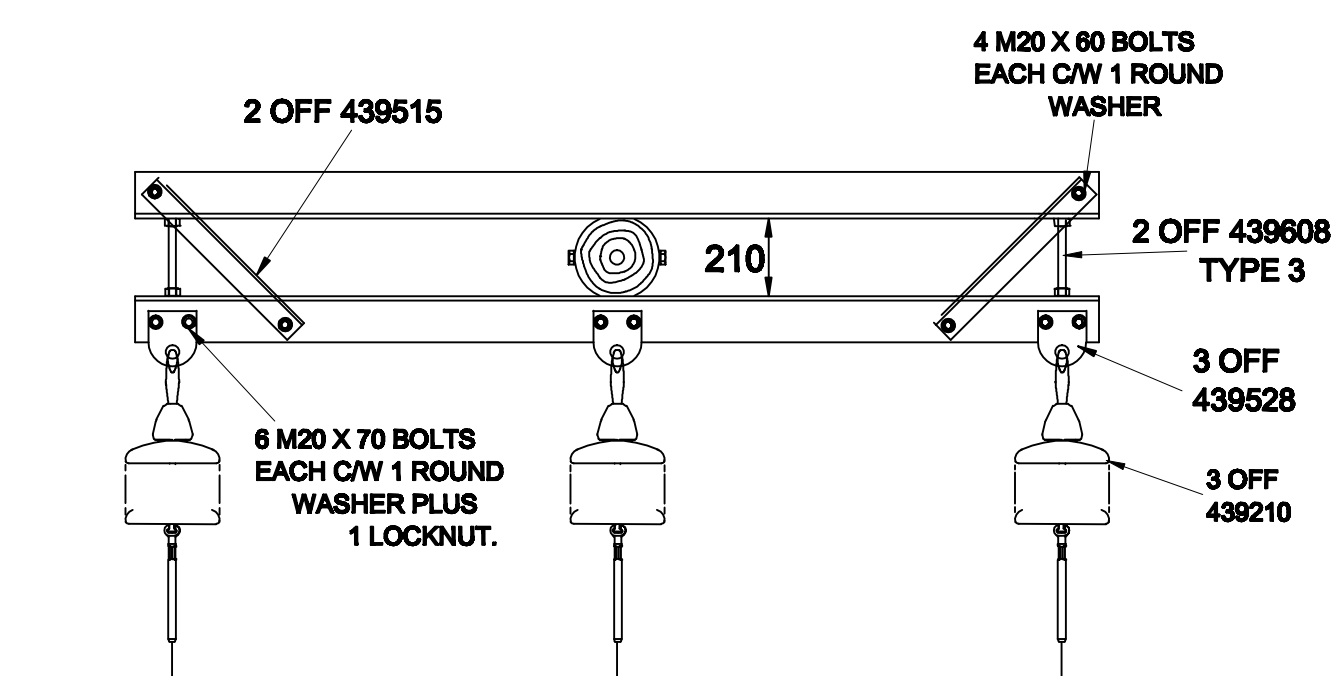
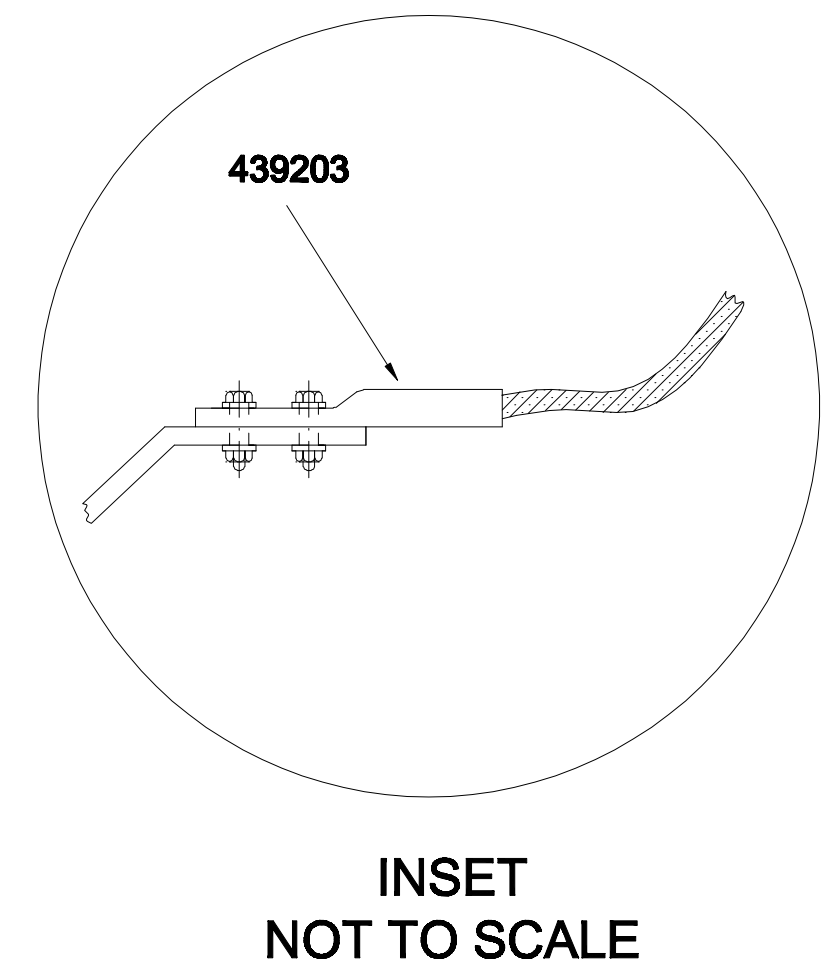
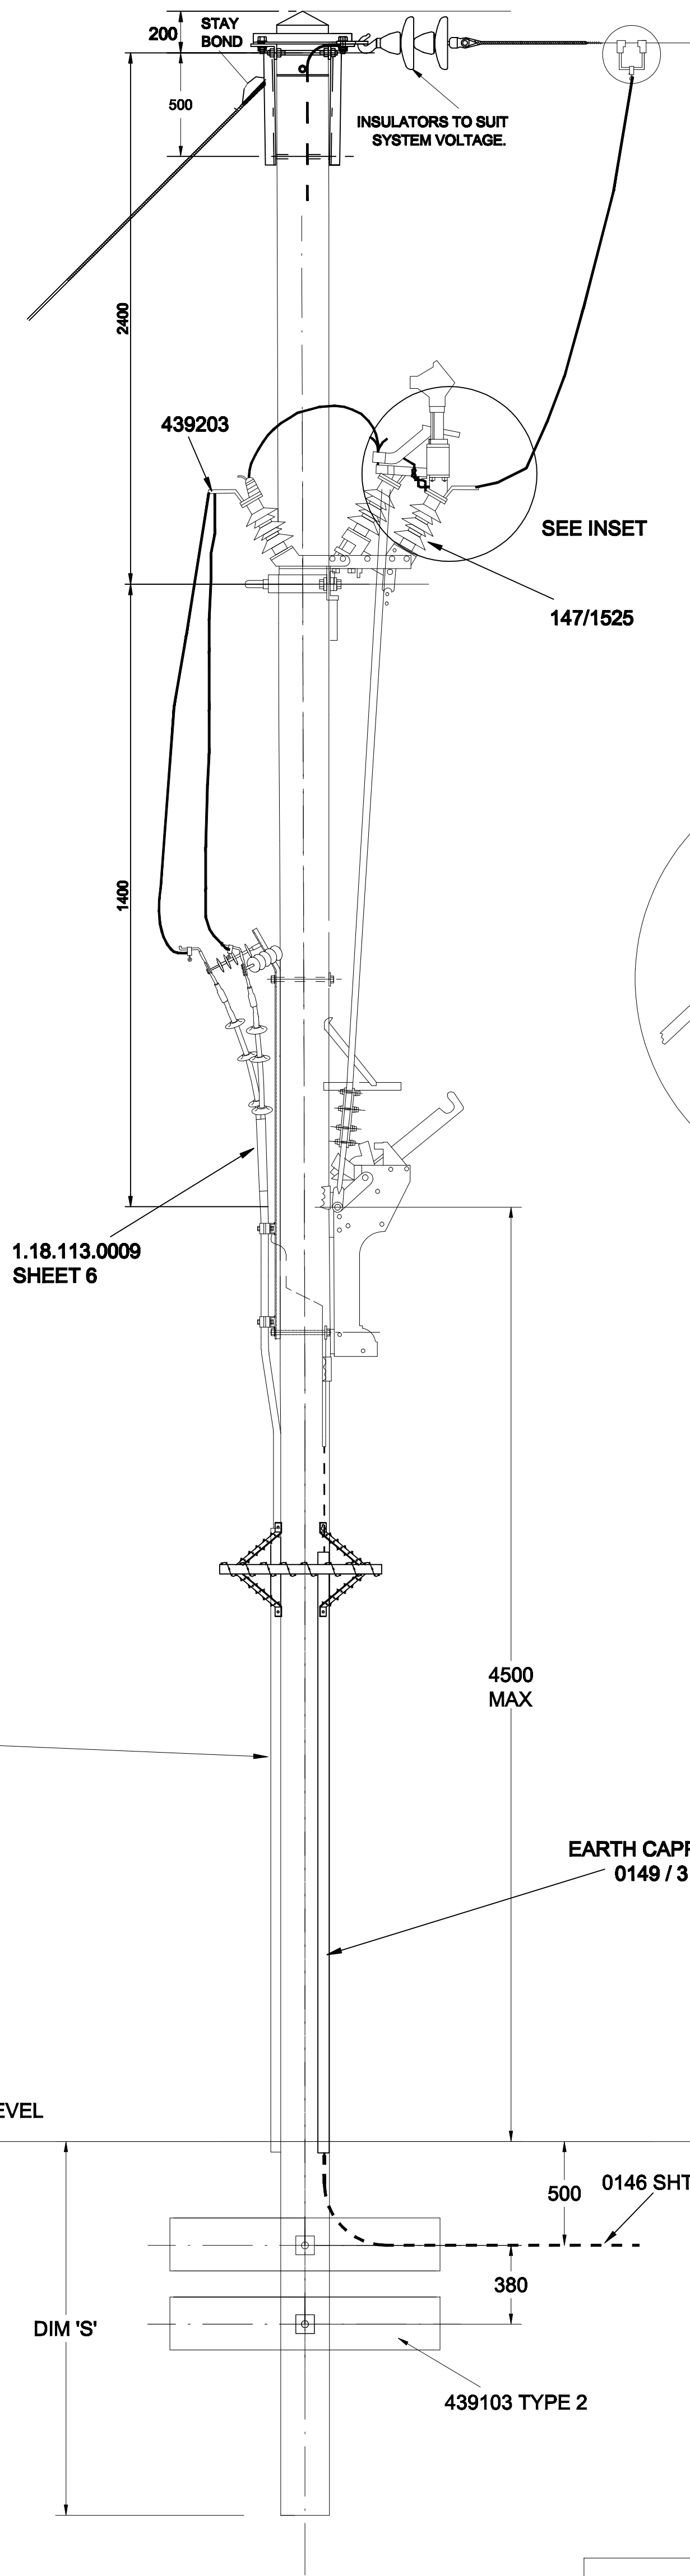


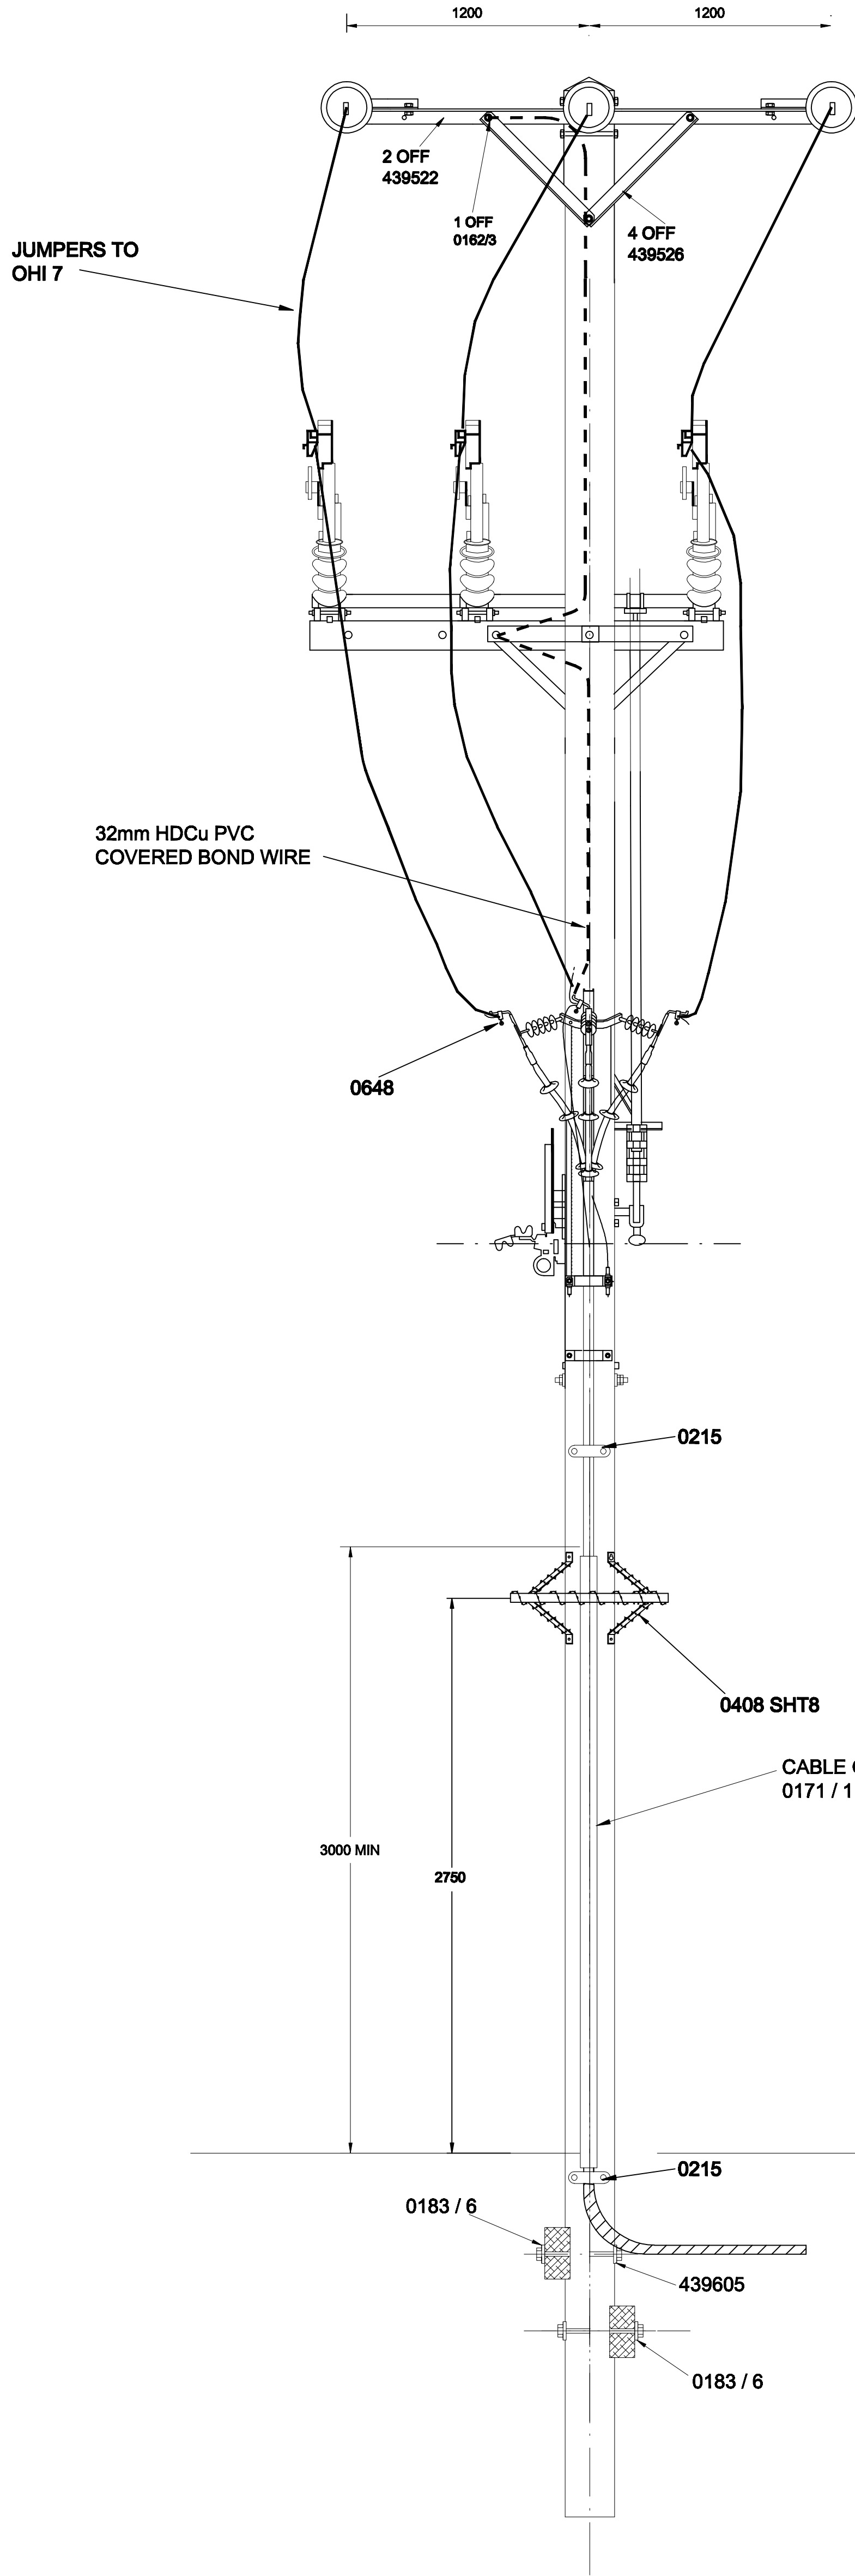

- NOTES:
1. STANDARD POLE LENGTH 11.0m.
 2. FIT 2 M20 POLE BOLTS WITH 2 WASHERS 439605 AT POLE TOP.
 3. TERMINATION TO SUIT CONDUCTOR TYPE
 4. ALL POLE BOLTS TO BE M20 EXCEPT WHERE OTHERWISE STATED.
 5. DETAIL DRAWINGS PREFIXED 43.... REFER TO E.S.I. DRGS. AND OTHER DETAIL DRGS. REFER TO 1.09.101. SERIES
 6. ALL UNUSED BOLT HOLES SHALL BE PLUGGED.

POLE LENGTH (m)	SINKING DEPTH DIM 'S' (m)
11.5 TO 12.0	1.9
13.0 TO 14.0	2.1
15.0	2.4

ALL DIMENSIONS SHOWN ARE IN MILLIMETRES UNLESS OTHERWISE STATED.

CE Electric UK		Lloyds Court, 78 Grey Street, Newcastle Upon Tyne, NE1 6AF	
Manufacturer Details		H.V OVERHEAD LINES (11KV, 20KV AND 33KV SYSTEMS)	
Sheet No. 5	Scale 1:20	SINGLE POLE TERMINATION WITH ABSD AND CABLE TERMINATION	
Prepared By Janis Webb	Grid Reference	Type OVERHEAD	POLES
Revised 31/01/07	Ref No. C927315	Historic Drg.No.	1091100937
Date Issued 02/03/06	Checked By S SALKELD	Revision B	Notes