
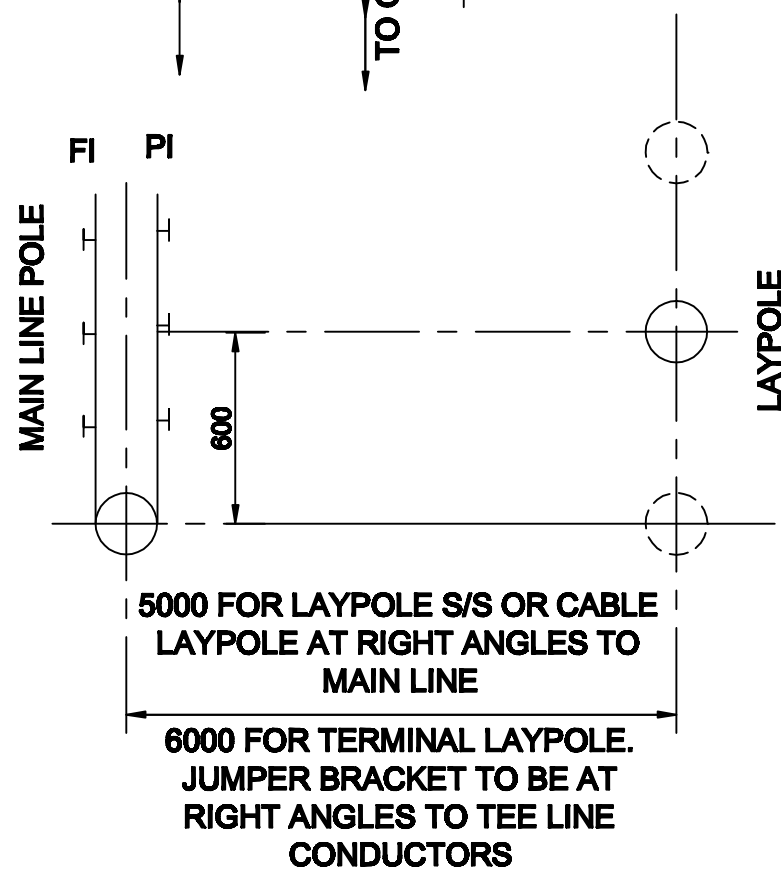


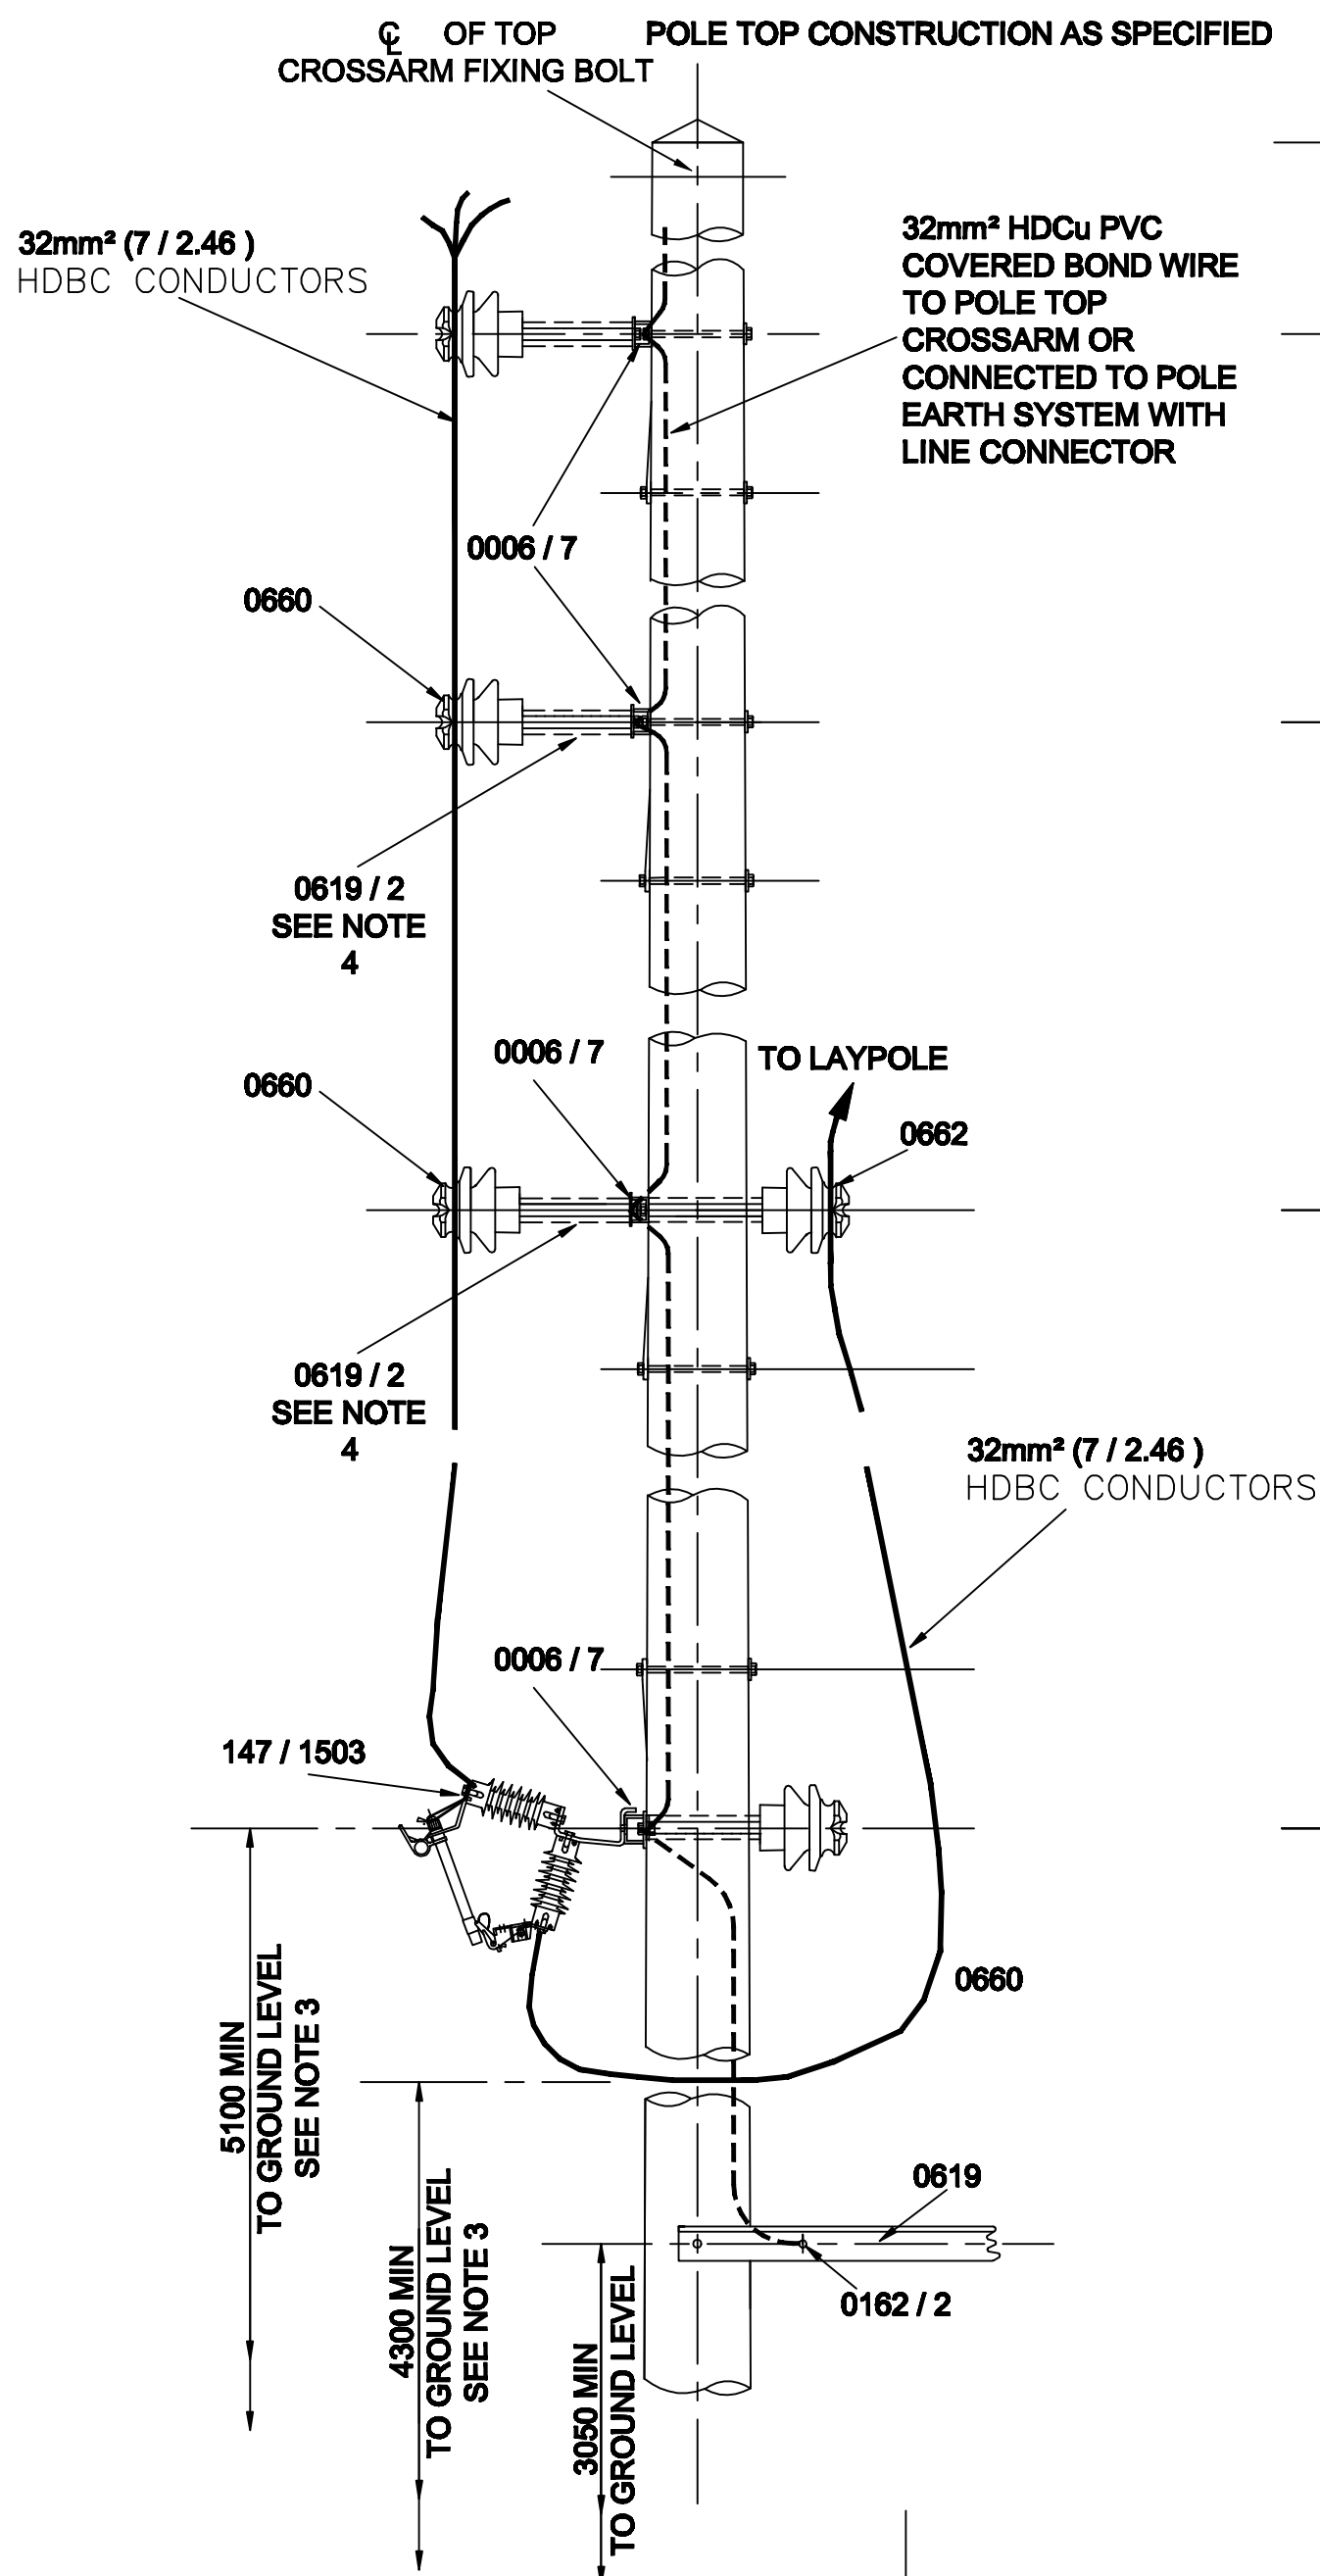


DETAIL 'A'

NORMAL POSITION OF LAYPOLE FROM MAIN LINE POLE

NOTES

1. ALL HOLES IN POLE TO BE 22mm DIA. POLE BOLTS TO BE M20 WITH 1 CURVED WASHER TO DRG. No 439605
2. EXISTING POLE TO BE DRILLED & NOTCHED 12mm DEEP FOR CHANNELS ON SITE
3. AT ROAD CROSSING SUPPORTS MINIMUM LINE CONDUCTOR REGULATION CLEARANCES MUST BE PROVIDED TO THE LOWEST JUMPER CONDUCTOR AND THE DIMENSIONS BETWEEN BRACKETS ADJUSTED ACCORDINGLY
4. PILOT PINS TO DRG. No 1.09.101.0619 / 2 ON EARTHED POLES. ALL PILOT PINS TO BE FITTED WITH A TUBULAR BIRDCUARD.

ALL DIMENSIONS SHOWN ARE IN MILLIMETRES UNLESS OTHERWISE STATED

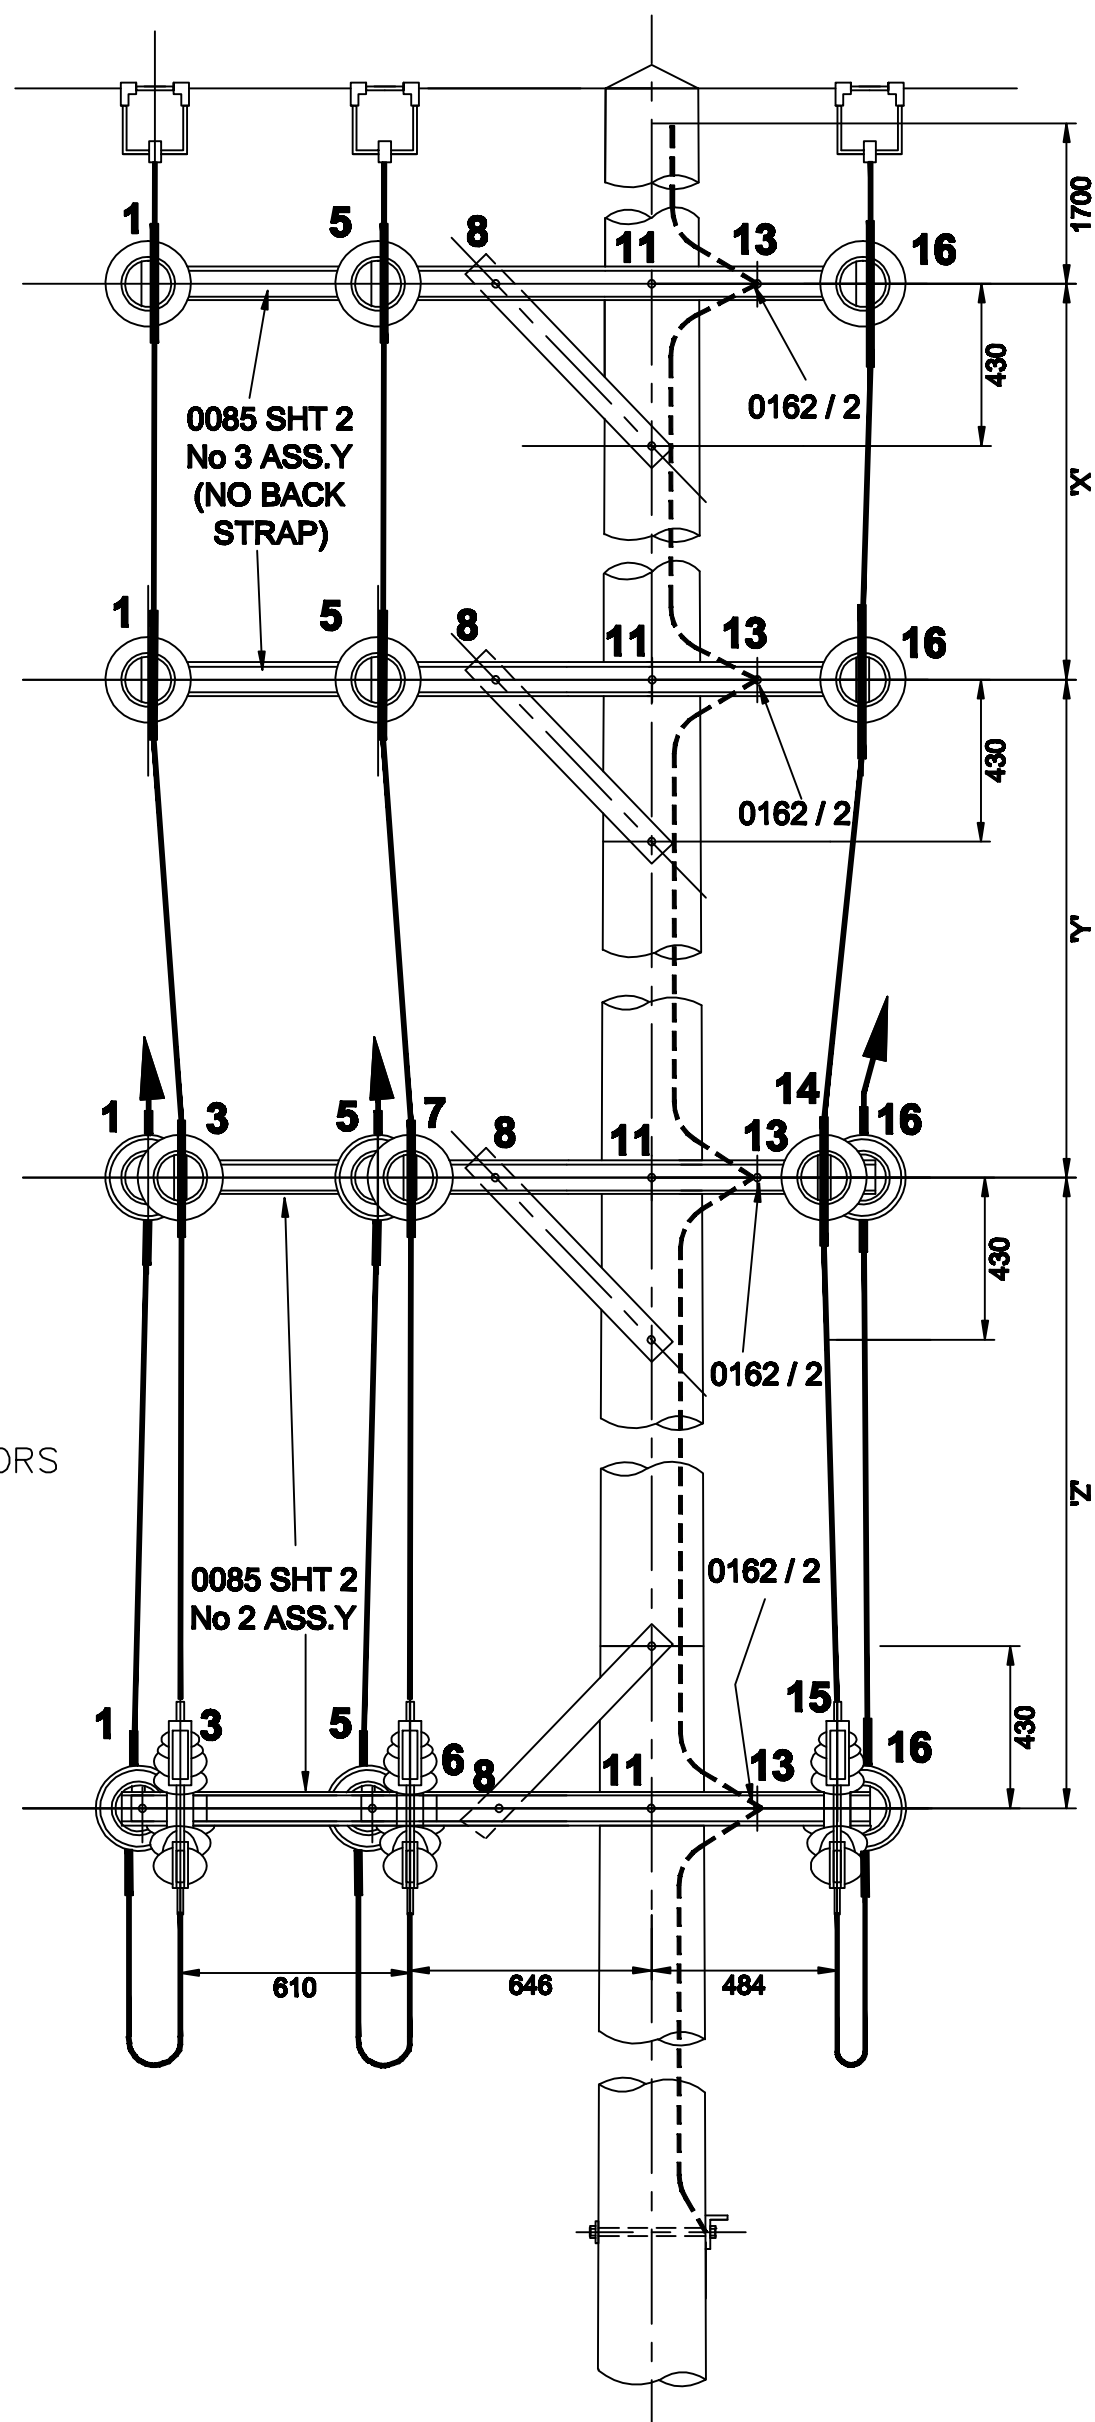

POLE LENGTH		DIMENSIONS		
		'X'	'Y'	'Z'
FEET	METRES	mm	mm	mm
32	-	-	-	1200
-	10.0	-	-	1400
34	-	-	-	1800
-	10.5	-	-	1900
36	-	-	-	2100
-	11.0	-	-	2200
-	11.5	-	1300	1400
38	-	-	1300	1400
-	12.0	-	1600	1600
40	-	-	1700	1700
42	-	-	1700	2000
-	12.0	-	1900	2000
45	-	1500	1500	1600
-	14.0	1600	1700	1600
48	-	1800	1800	1800
-	15.0	1950	2000	2000
50	-	2000	2000	2100
-	16.0	2200	2200	2200

NB DIMENSIONS 'X' & 'Y' ARE APPROXIMATE (SEE NOTE 3)

THIS DRAWING ALSO REFERRED TO IN WORKS SPEC REF No 04 / 256

		Lloyds Court, 78 Grey Street, Newcastle Upon Tyne, NE1 6AF		
		11KV & 20KV OVERHEAD LINES ARRANGEMENT OF 3 PHASE TEE - OFF STRAIGHT LINE POLE TO LAYPOLE WITH FUSE UNITS (2 FUSES AT ONE SIDE OF POLE)		
Manufacturer Details		Type	OVERHEAD LINES	
Sheet No. 1	Scale 1:20	Ref No.	C101777	Historic Drg.No.
Prepared By Janis.Webb	Grid Reference	Revision	F	Notes
Revised 09/03/06	Checked By G HAMMEL			
Date Issued 10/03/99				

1091121061