
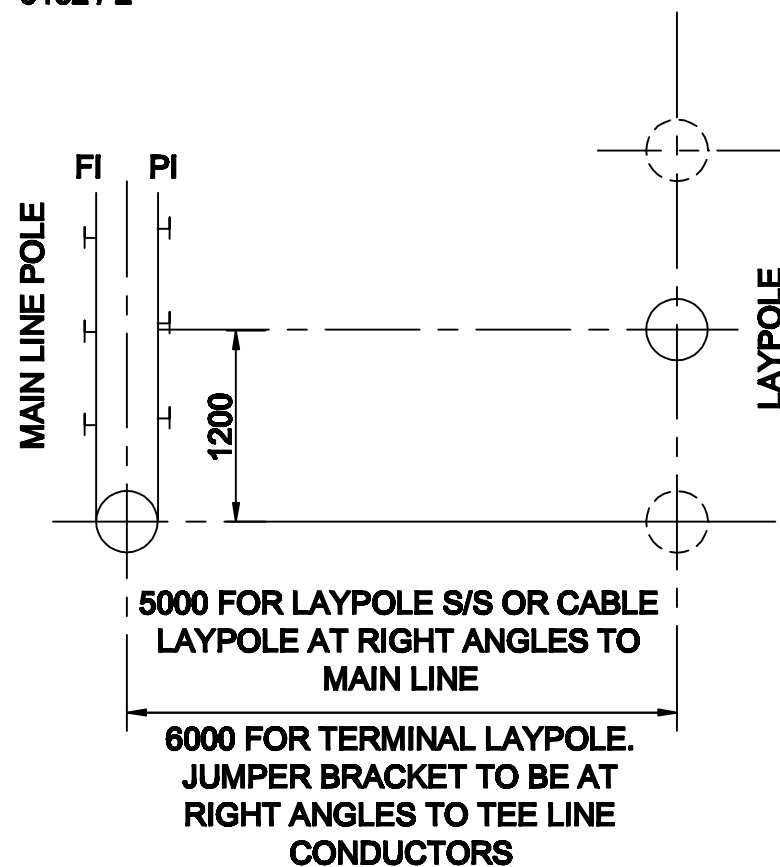
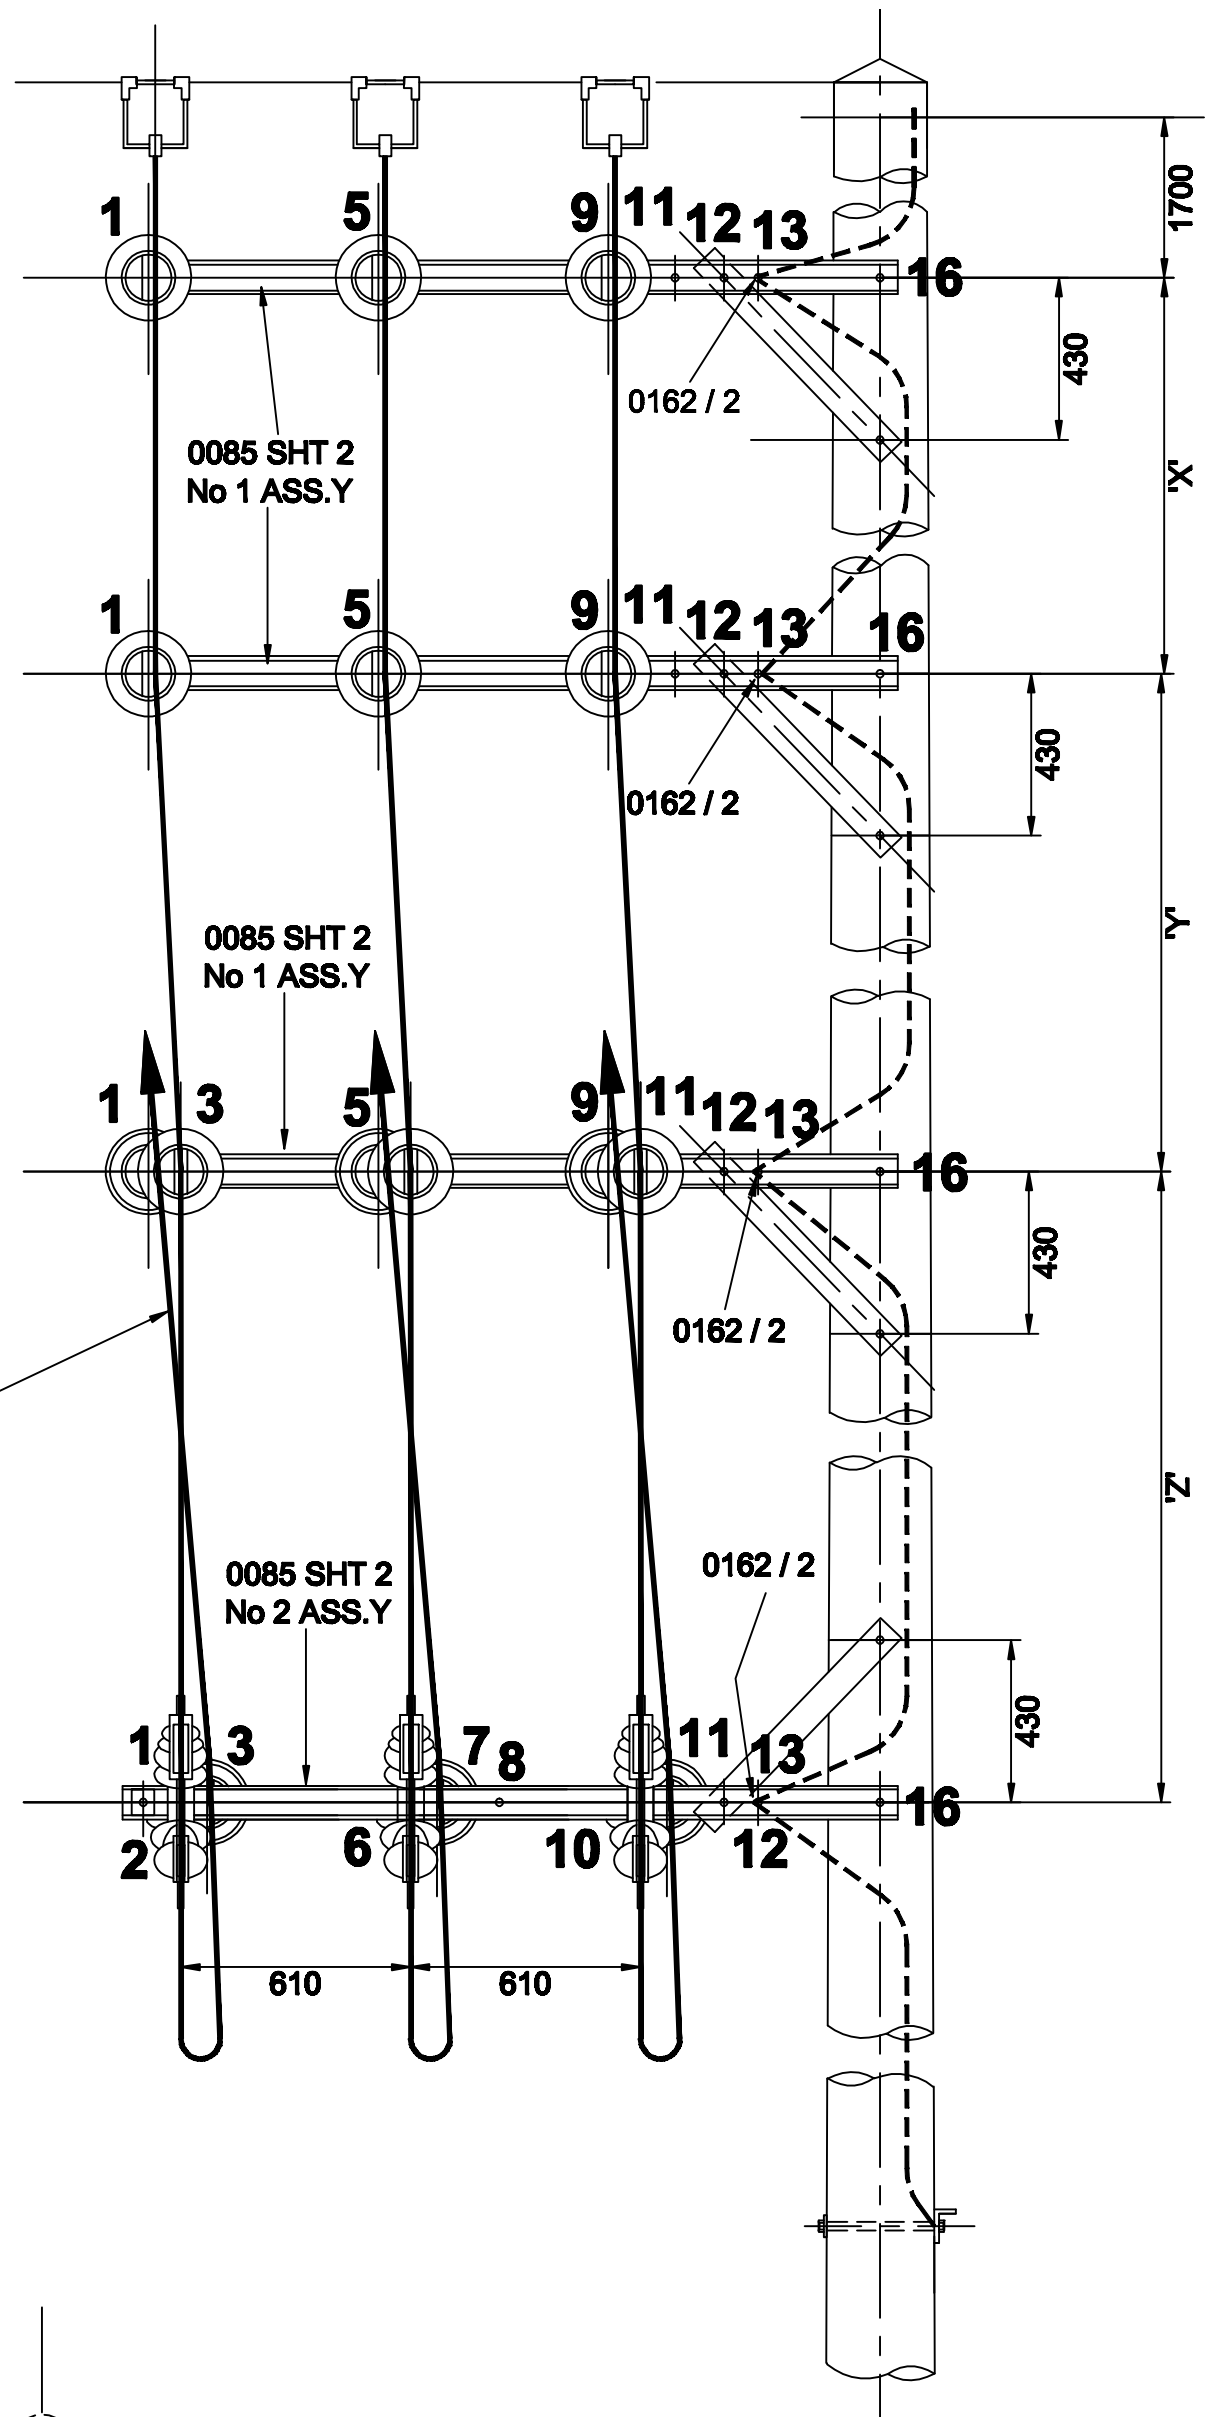


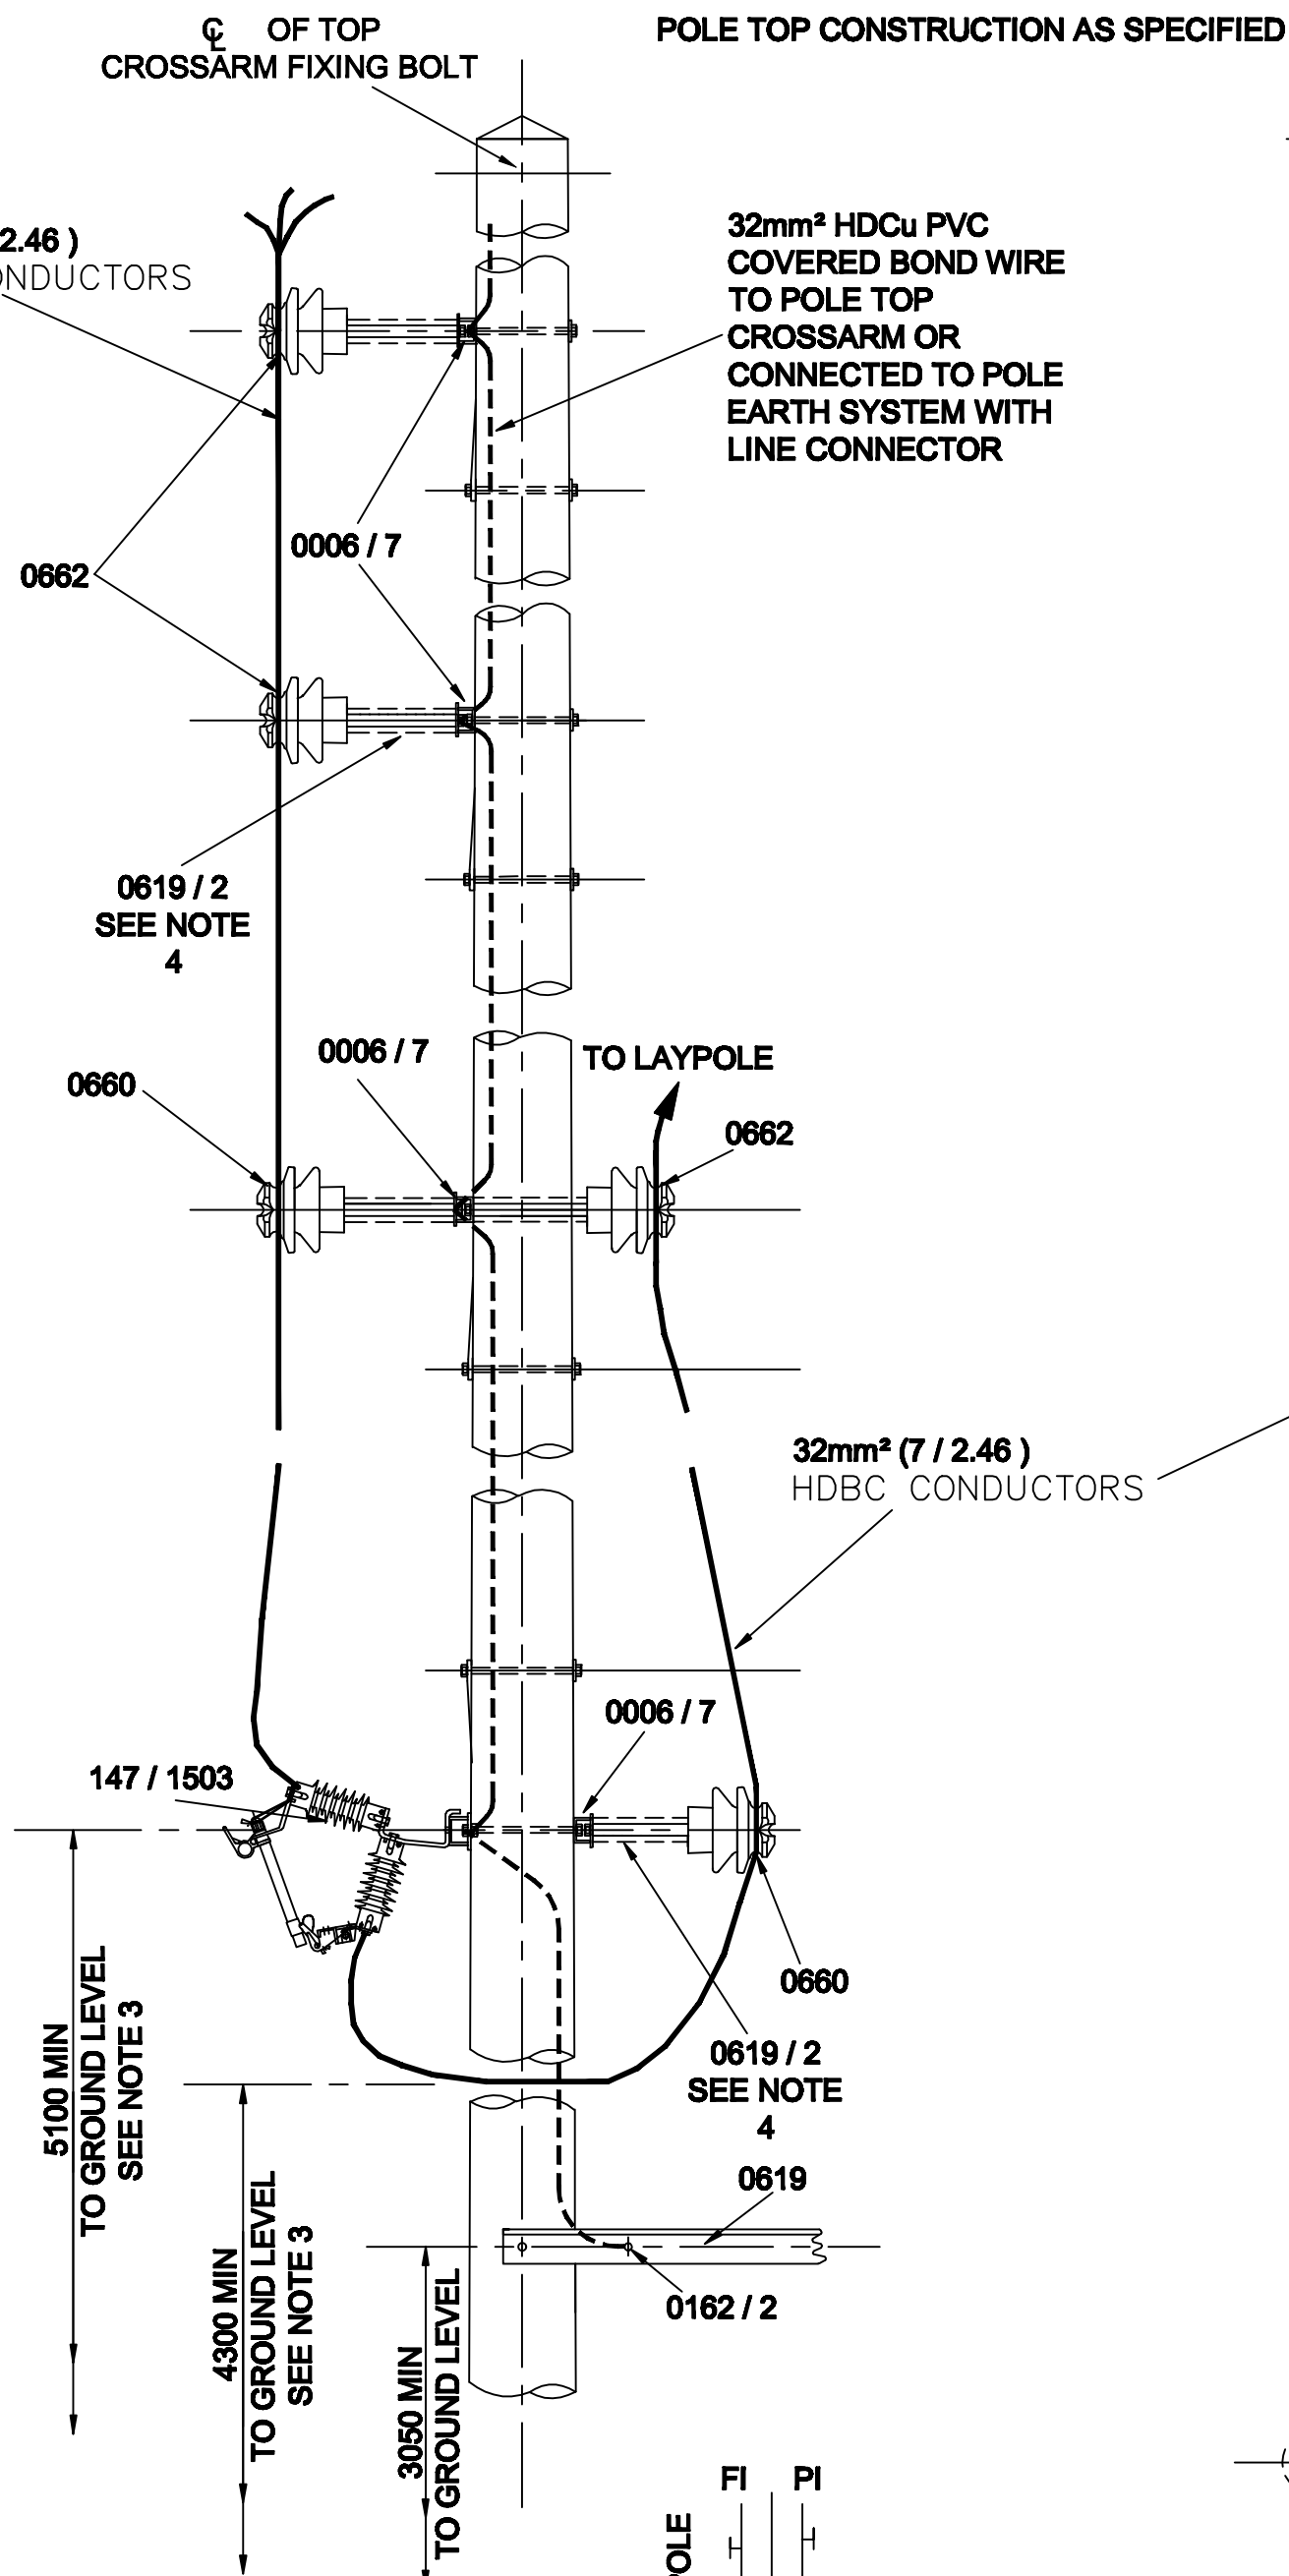

POLE LENGTH		DIMENSIONS		
		'X'	'Y'	'Z'
FEET	METRES	mm	mm	mm
32	-	-	-	1280
-	10.0	-	-	1500
34	-	-	-	1880
-	10.5	-	-	2000
36	-	-	-	2150
-	11.0	-	-	2200
-	11.5	-	1300	1400
38	-	-	1400	1400
-	12.0	-	1650	1600
40	-	-	1700	1700
42	-	-	1800	2000
-	12.0	-	1950	2000
45	-	1500	1530	1600
-	14.0	1600	1750	1600
48	-	1850	1850	1850
-	15.0	1950	2000	2000
50	-	2000	2000	2150
-	16.0	2200	2300	2150

NB DIMENSIONS 'X' & 'Y' ARE APPROXIMATE (SEE NOTE 3)

NOTES

- ALL HOLES IN POLE TO BE 22mm DIA. POLE BOLTS TO BE M20 WITH 1 CURVED WASHER TO DRG No 439605
- POLES TO BE DRILLED AND NOTCHED 12mm DEEP FOR CHANNELS
- AT ROAD CROSSING SUPPORTS MINIMUM LINE CONDUCTOR REGULATION CLEARANCES MUST BE PROVIDED TO THE LOWEST JUMPER CONDUCTOR AND THE DIMENSIONS BETWEEN BRACKETS ADJUSTED ACCORDINGLY
- PILOT PINS TO DRG. No 1.09.101.0619 / 2 ON EARTHED POLES. ALL PILOT PINS TO BE FITTED WITH TUBULAR BIRDCUARD

NORMAL POSITION OF LAYPOLE FROM MAIN LINE POLE

THIS DRAWING ALSO REFERRED TO IN WORKS SPEC REF Nos 04 / 257

ALL DIMENSIONS SHOWN ARE IN MILLIMETRES UNLESS OTHERWISE STATED

 CE Electric UK		Lloyds Court, 78 Grey Street, Newcastle Upon Tyne, NE1 6AF			
Manufacturer Details		11KV & 20KV OVERHEAD LINES ARRANGEMENT OF 3 PHASE TEE-OFF STRAIGHT LINE POLE TO LAYPOLE WITH FUSE UNITS (3 FUSES AT ONE SIDE OF POLE)			
Sheet No. 1	Scale 1:20				
Prepared By Janis.Webb					
Type		LINES			
Revised 09/03/06	Grid Reference	Ref No.	C101778	Historic Drg.No.	1091121063
Date Issued 10/03/99	Checked By G HAMMEL	Revision E	Notes		