

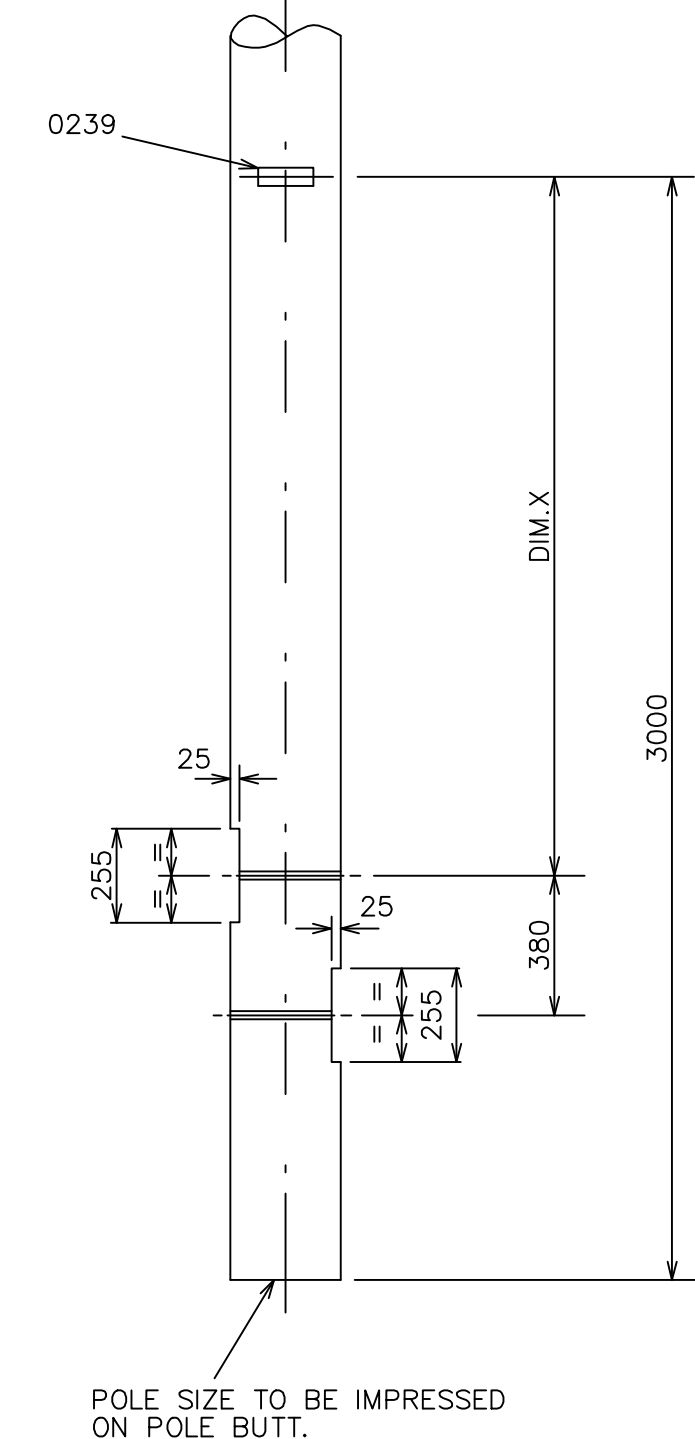


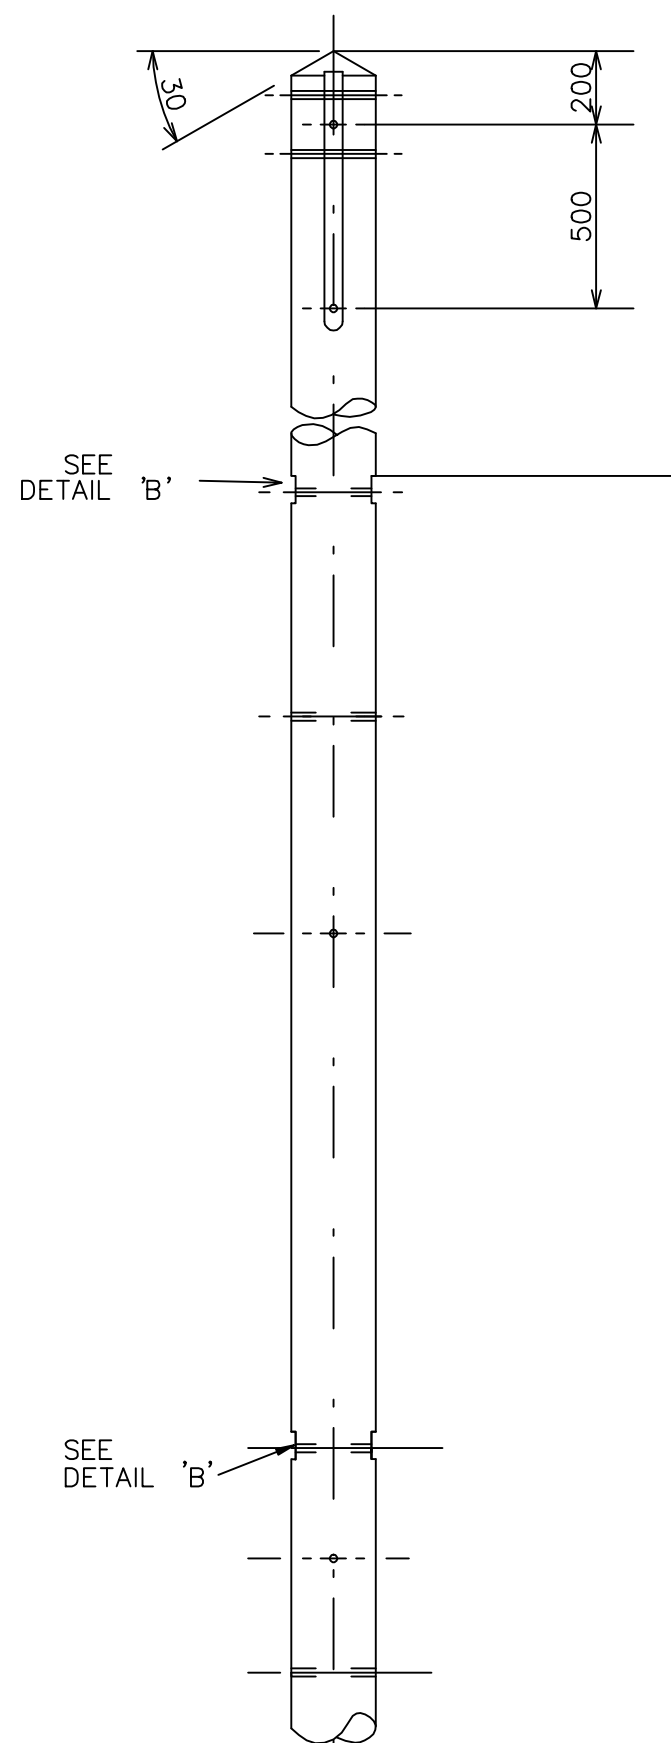

POLE SIZE TO BE IMPRESSED ON POLE BUTT.

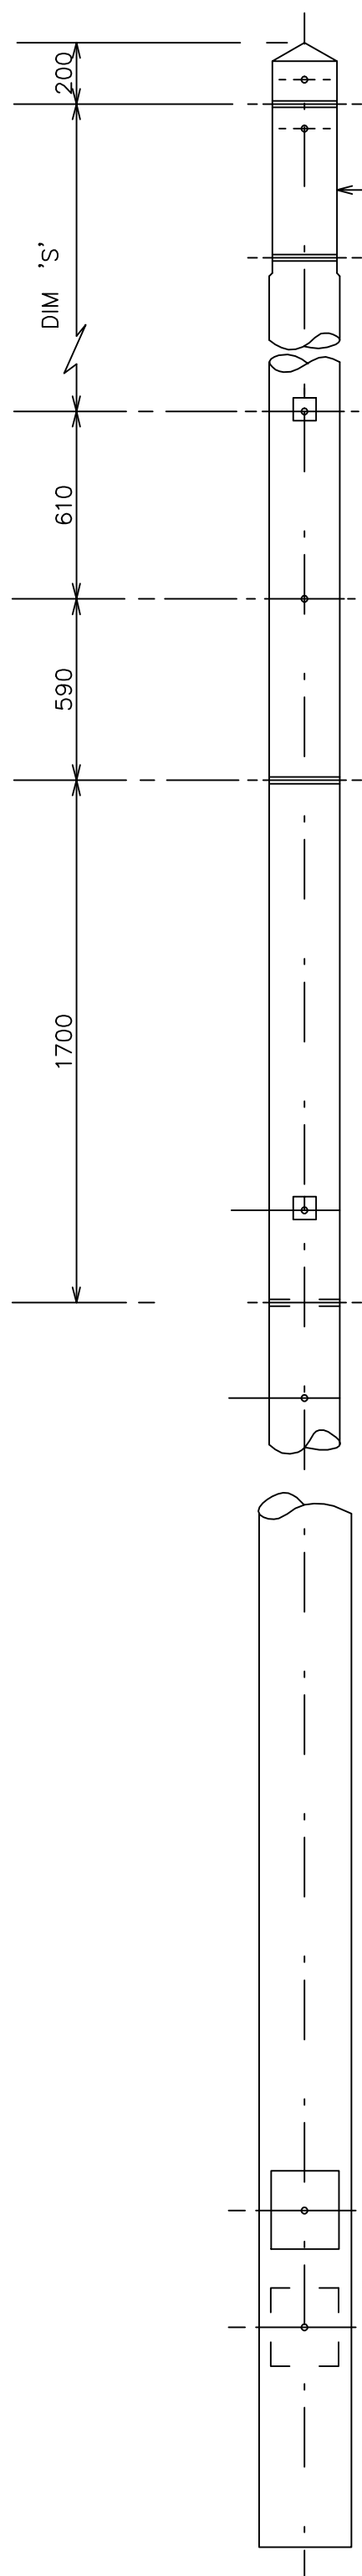


SEE DETAIL A

SCARFING TO BE CUT TO GIVE A FLAT ON BOTH FACES OF POLE, THE ENDS CHAMFERED OFF AS SHOWN.

45 CHAMFER

DETAIL 'A'

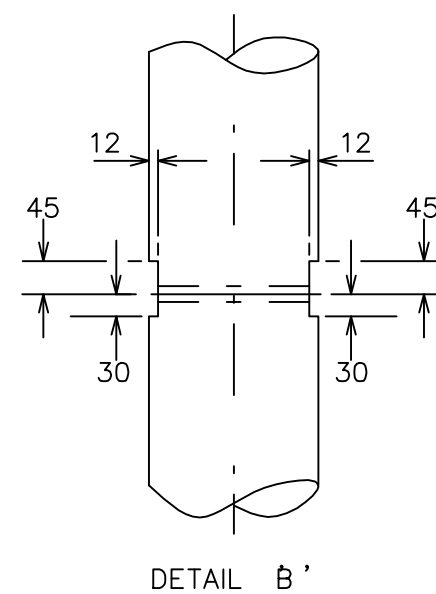

DETAIL 'B'

NOTES.

1. ALL HOLES TO BE 22mm DIAMETER, DRILLED AT RIGHT ANGLES TO VERTICAL CENTRE LINE OF POLE. ALL DRILLING AND CUTTING TO BE DONE STRICTLY TO TEMPLATE PRIOR TO CREOSOTING.
2. POLE BUTT TO BE CUT AT RIGHT ANGLES TO AXIS OF POLE.
3. ALL POLES TO BE NOTCHED AND DRILLED FOR 250 X 125 BAULKS.
4. POLE GRADE TO BE STOUT.

POLE LENGTH	DIM 'S' mm	DIM 'X' mm
11.0m	2000	1900
12.0m	2800	1400

ALL DIMENSIONS SHOWN ARE IN MILLIMETRES UNLESS OTHERWISE STATED.

		NEDL, Manor House, Station Road, Houghton le Spring, DH4 7LA.	
		11kV OVERHEAD LINES DRILLING, SCARFING AND MARKING FOR DRG.No.1.09.112.1069 SHEET 7	
Prepared by J.B.	Drg.No.	1 09 112 1069	Sheet No. 8
Checked M.W.	Date Issued FEB'92		Revised 12.2000
		Scale 1:20 & 1:10	