
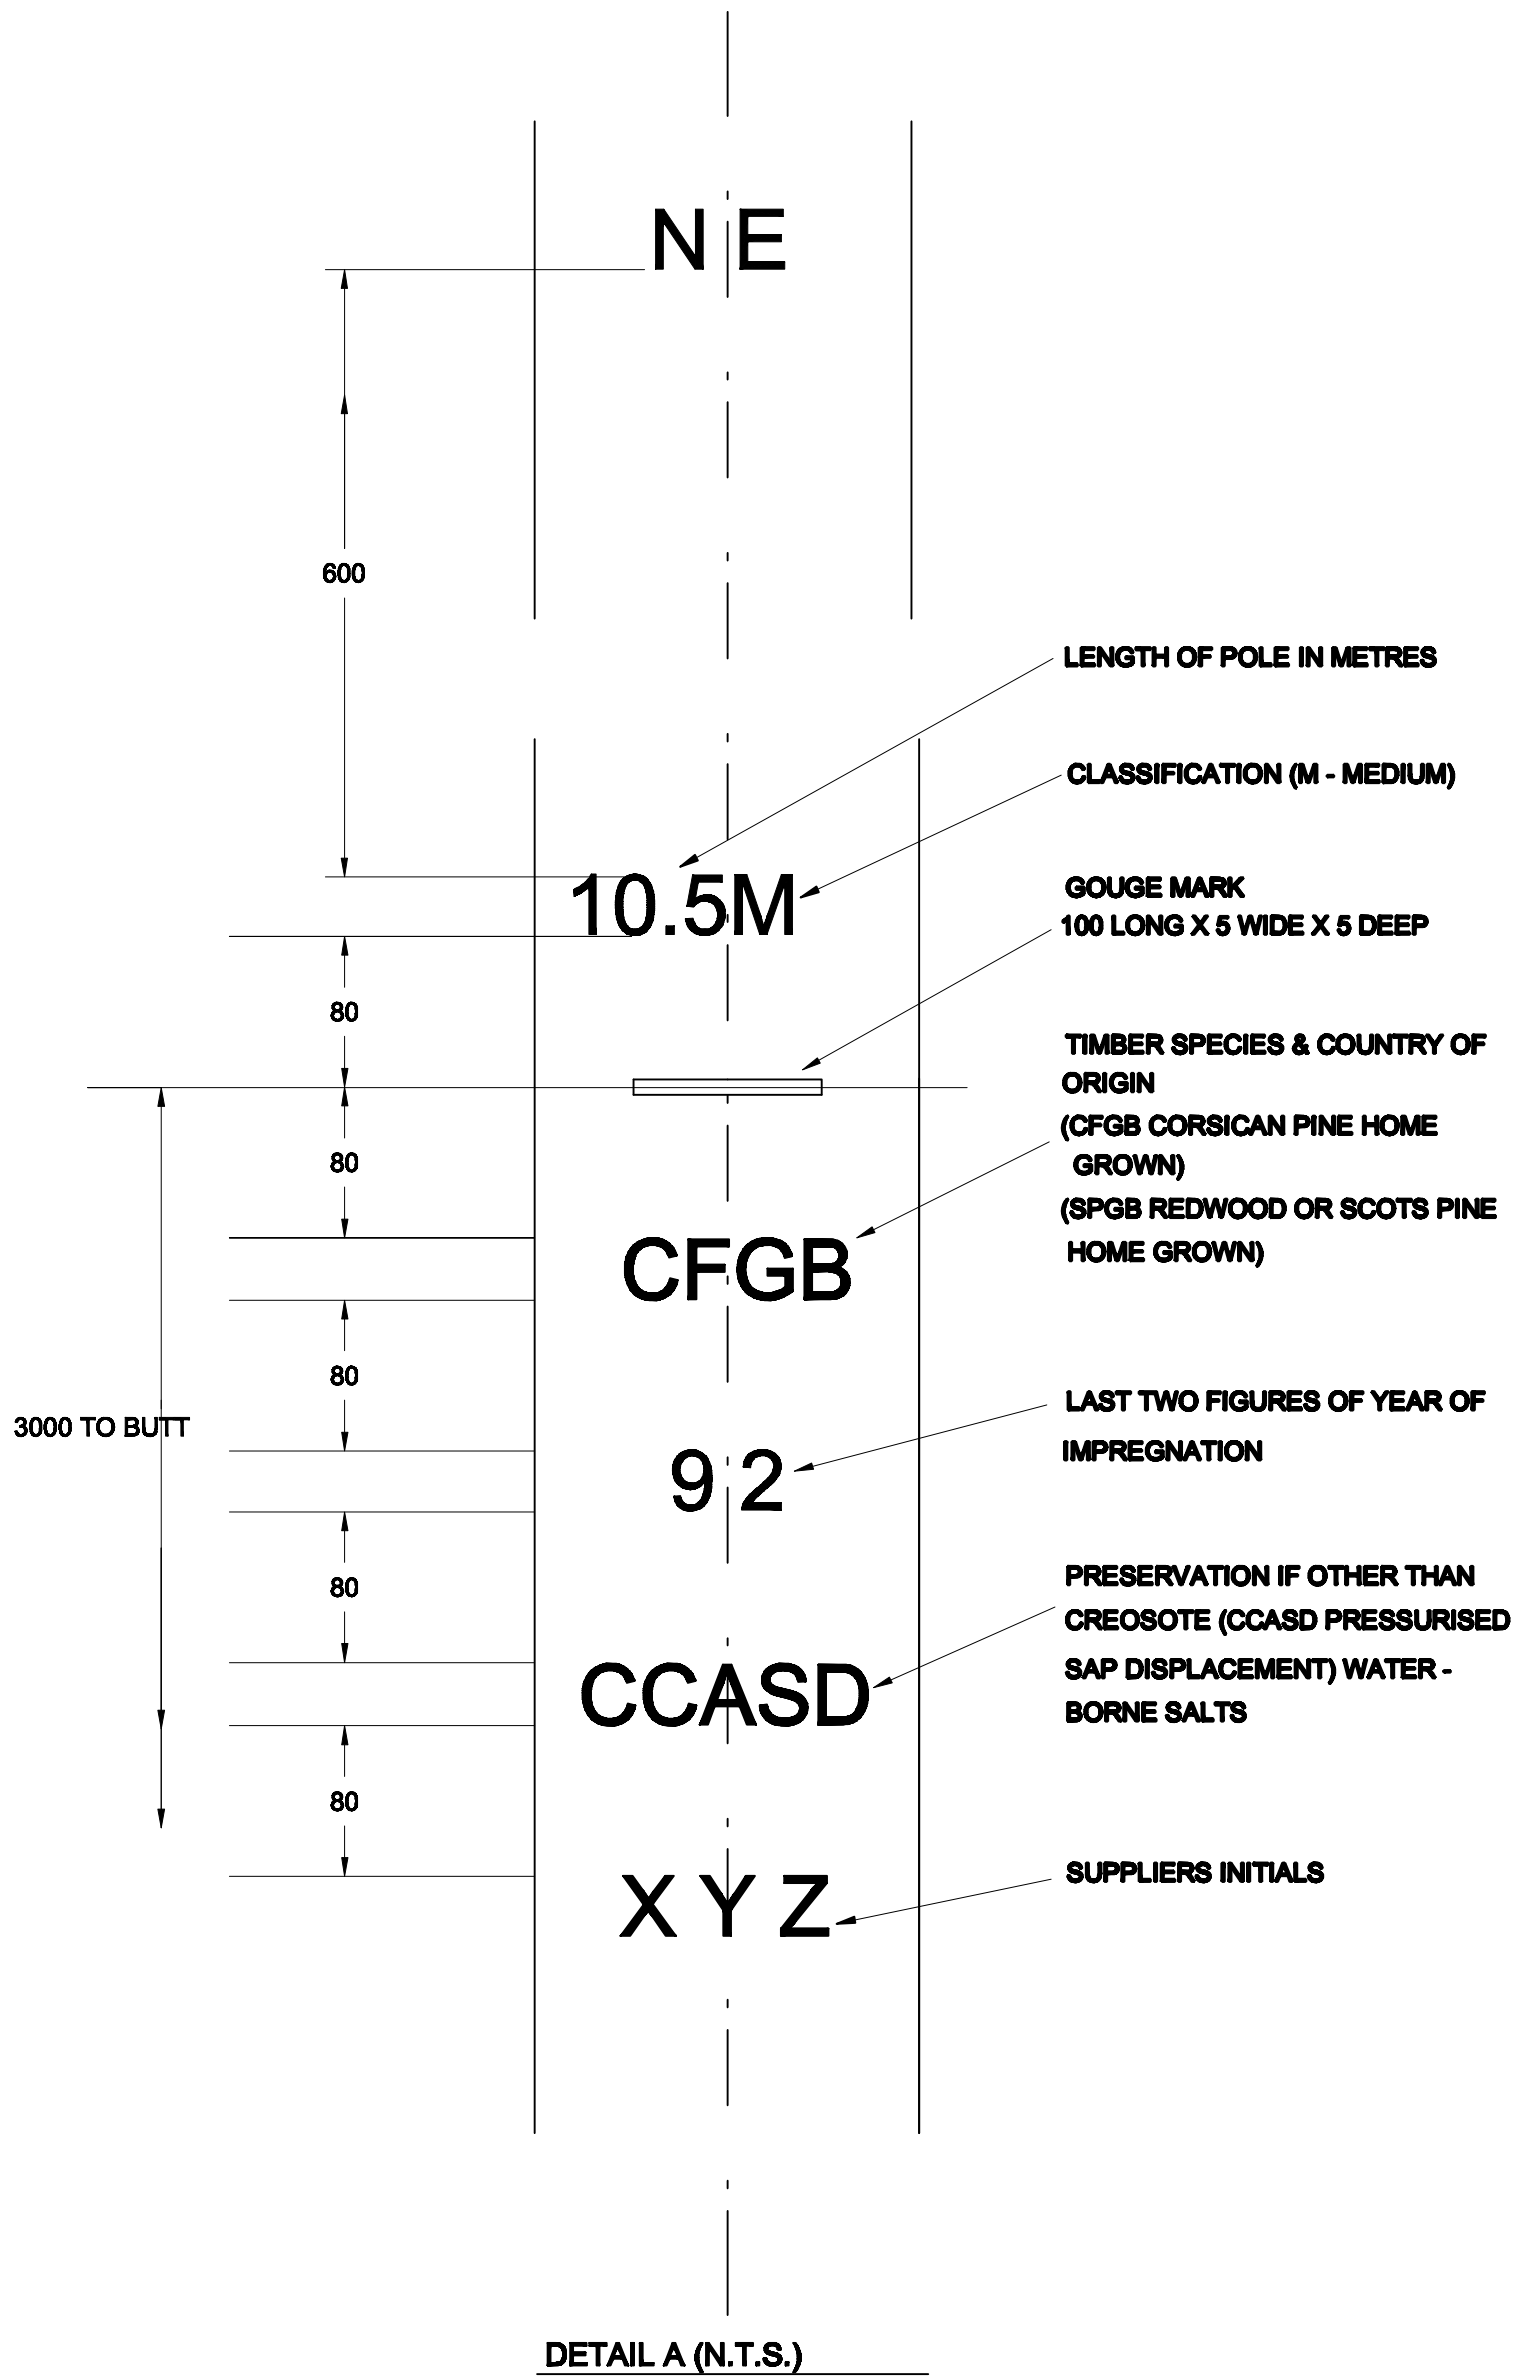


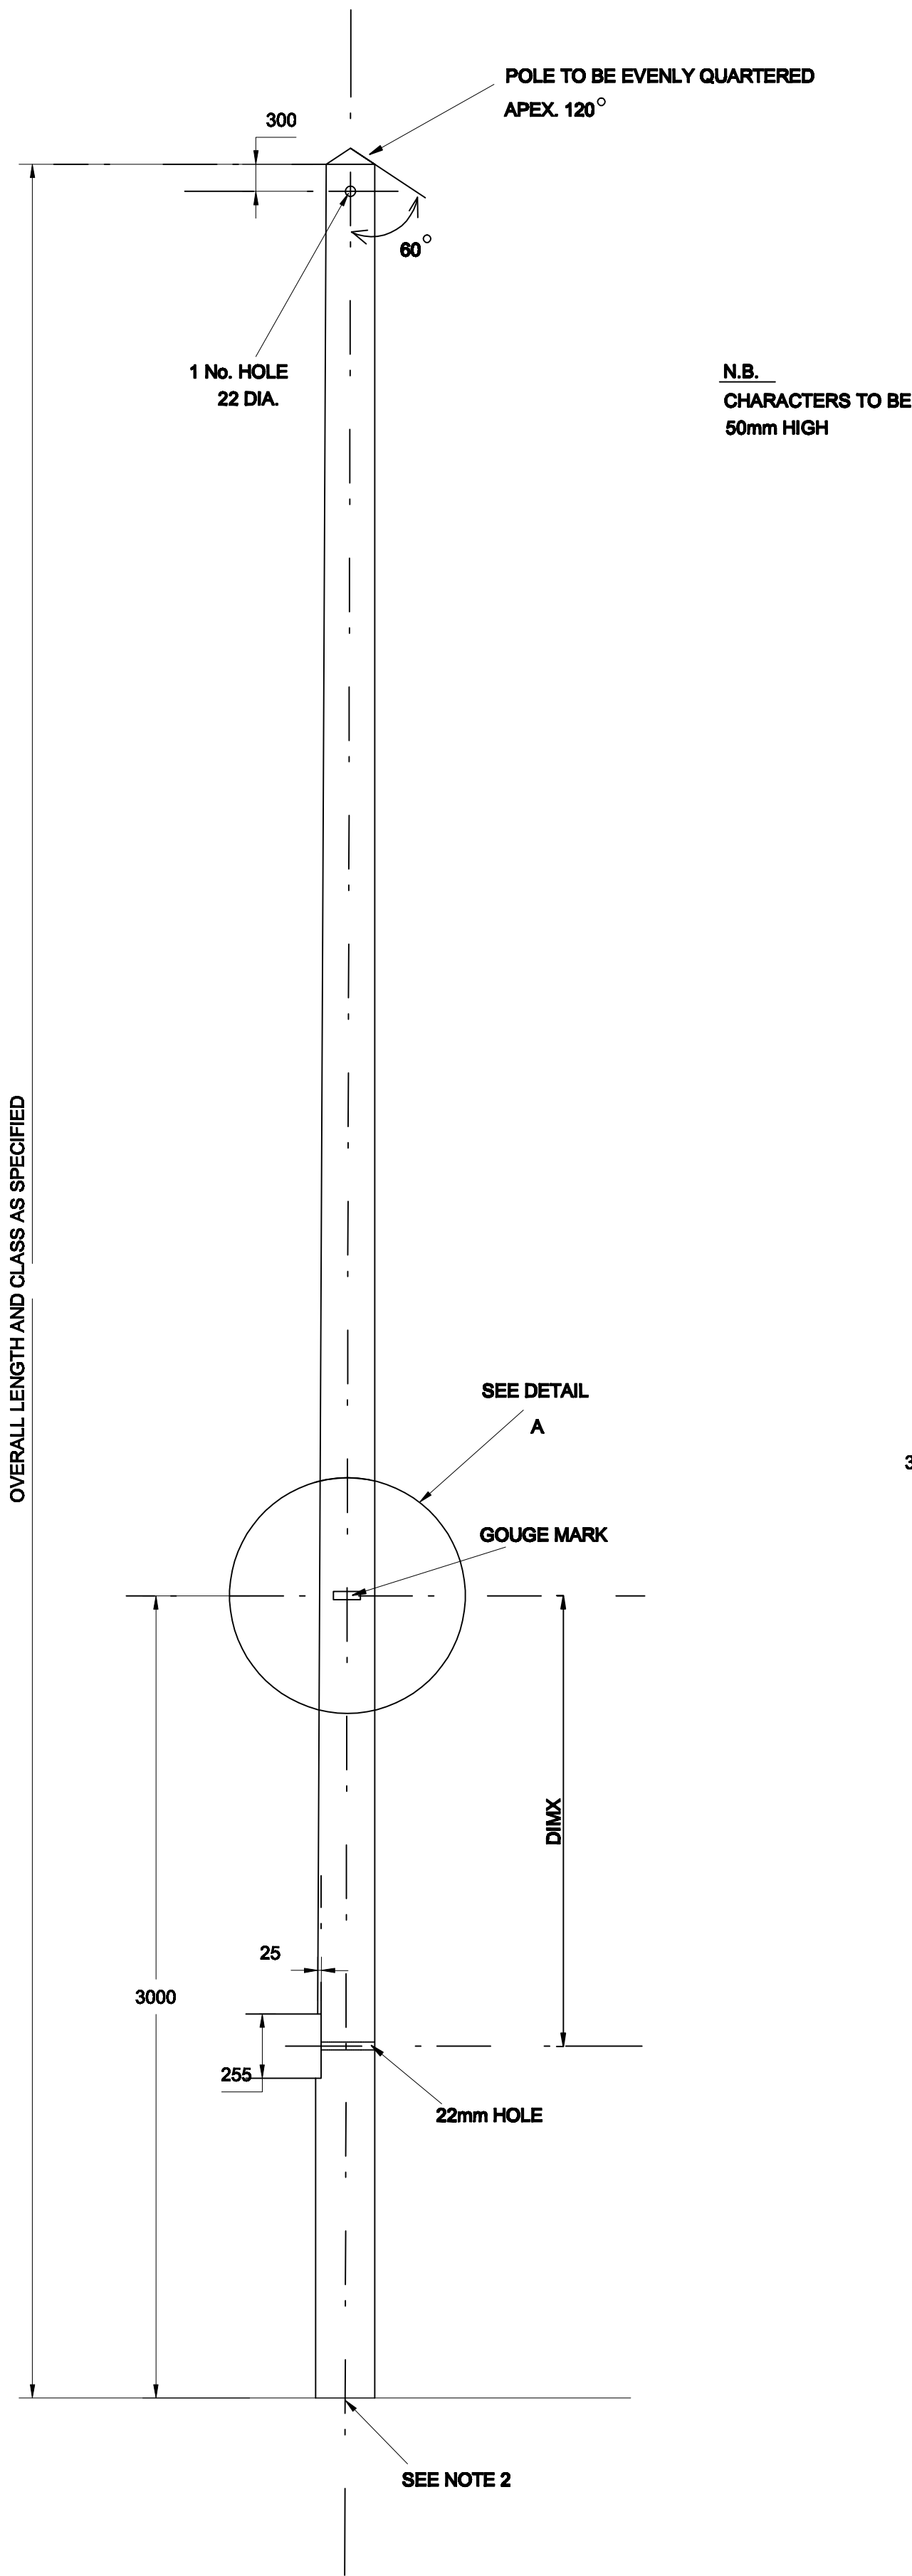

- NOTES
- POLES TO BE HOME GROWN SOFTWOOD TREATED BY PRESSURISED SAP DISPLACEMENT (SALT TREATMENT)
 - POLE LENGTH CLASSIFICATION & SUPPLIERS NAME OR MARK TO BE IMPRESSED ON BUTT END GRAIN
 - BASED ON E.S.I. STD. 43-88 APPENDIX N AND E.S.I. DRG No.431021

POLE LENGTH (m)	DIMENSION 'X' (mm)	SINKING DEPTH (mm)
9.0 - 11.0	1900	1600
12.0	1700	1800
13.0 - 14.0	1400	1800

ALL DIMENSIONS SHOWN ARE IN MILLIMETRES UNLESS OTHERWISE STATED

		Lloyds Court, 78 Grey Street, Newcastle Upon Tyne, NE1 6AF	
Manufacturer Details		LV OVERHEAD LINES DRILLING AND MARKING OF WOOD POLES FOR ABC CONSTRUCTION	
Sheet No. 4	Scale 1:20	Type OVERHEAD LINES	
Prepared By Janis.Webb		Ref No. C101821	Historic Drg.No. 1091193301
Revised 10/04/06	Grid Reference	Revision G	
Date Issued 17/03/05	Checked By S SALKELD	Notes	