


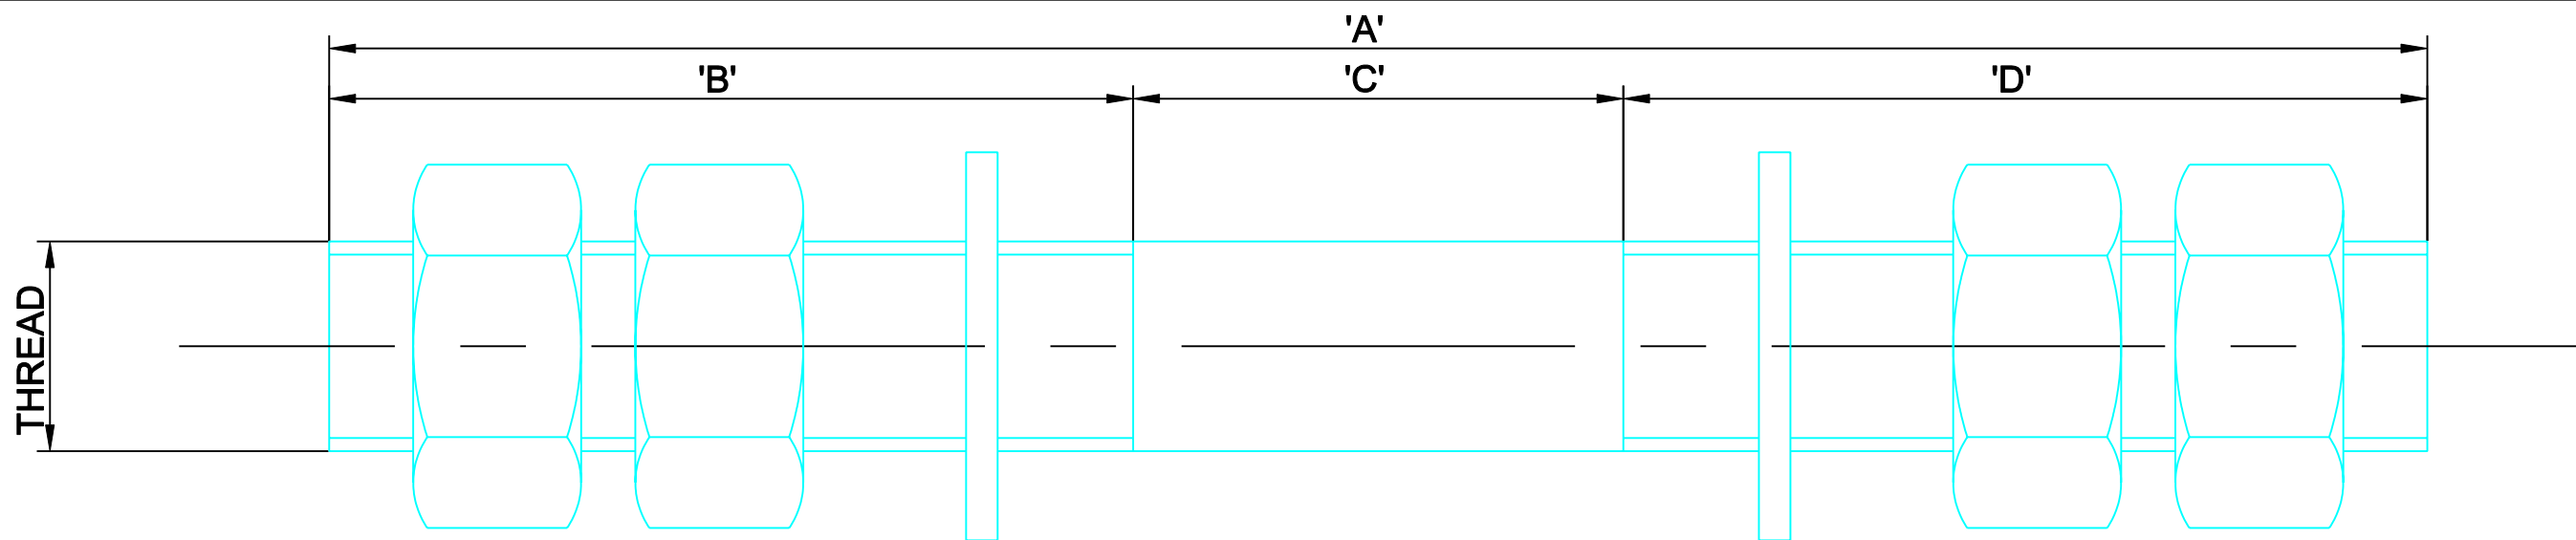

□□Ô□

ITEM No.	THREAD	'A'	'B'	'C'	'D'
1	M20	1200	200	800	200
2	M20	980	190	600	190
3	M20	940	295	350	295
4	M20	360	95	170	95
5	M20	700	250	200	250
6	M16	514	107	300	107
7	M16	554	107	340	107
8	M16	474	107	260	107
9	M20	550	125	300	125
10	M20	800	250	300	250
11	M20	450	125	200	125

NOTES

1. TIE ROD MATERIAL: STEEL TO B.S. 4190, STRENGTH GRADE DESIGNATION 4.6 & SHALL MEET REQUIREMENTS AS SHOWN IN B.S. 4190 TABLE 14.
2. TIE RODS SHALL BE SUPPLIED WITH FOUR FULL NUTS TO B.S. 4190 & TWO PLAIN WASHERS TO B.S. 4320.
3. ALL ITEMS SHALL BE GALVANISED TO B.S. 729 AFTER FABRICATION.

 CE Electric UK		Lloyds Court, 78 Grey Street, Newcastle Upon Tyne, NE1 6AF			
Manufacturer Details		OVERHEAD LINES M20 & M16 TIE ROD SCHEDULE			
Sheet No. 29	Scale N.T.S.				
Prepared By TREVOR R. WILKIN					
Revised 28/03/2007 - TRW	Grid Reference	Ref No.	62470B	Historic Drg.No.	1 09 101 0675
Date Issued 08/06/2006	Checked By DAVE MARSHALL	Revision 3	Notes REF. No. CORRECTED		