


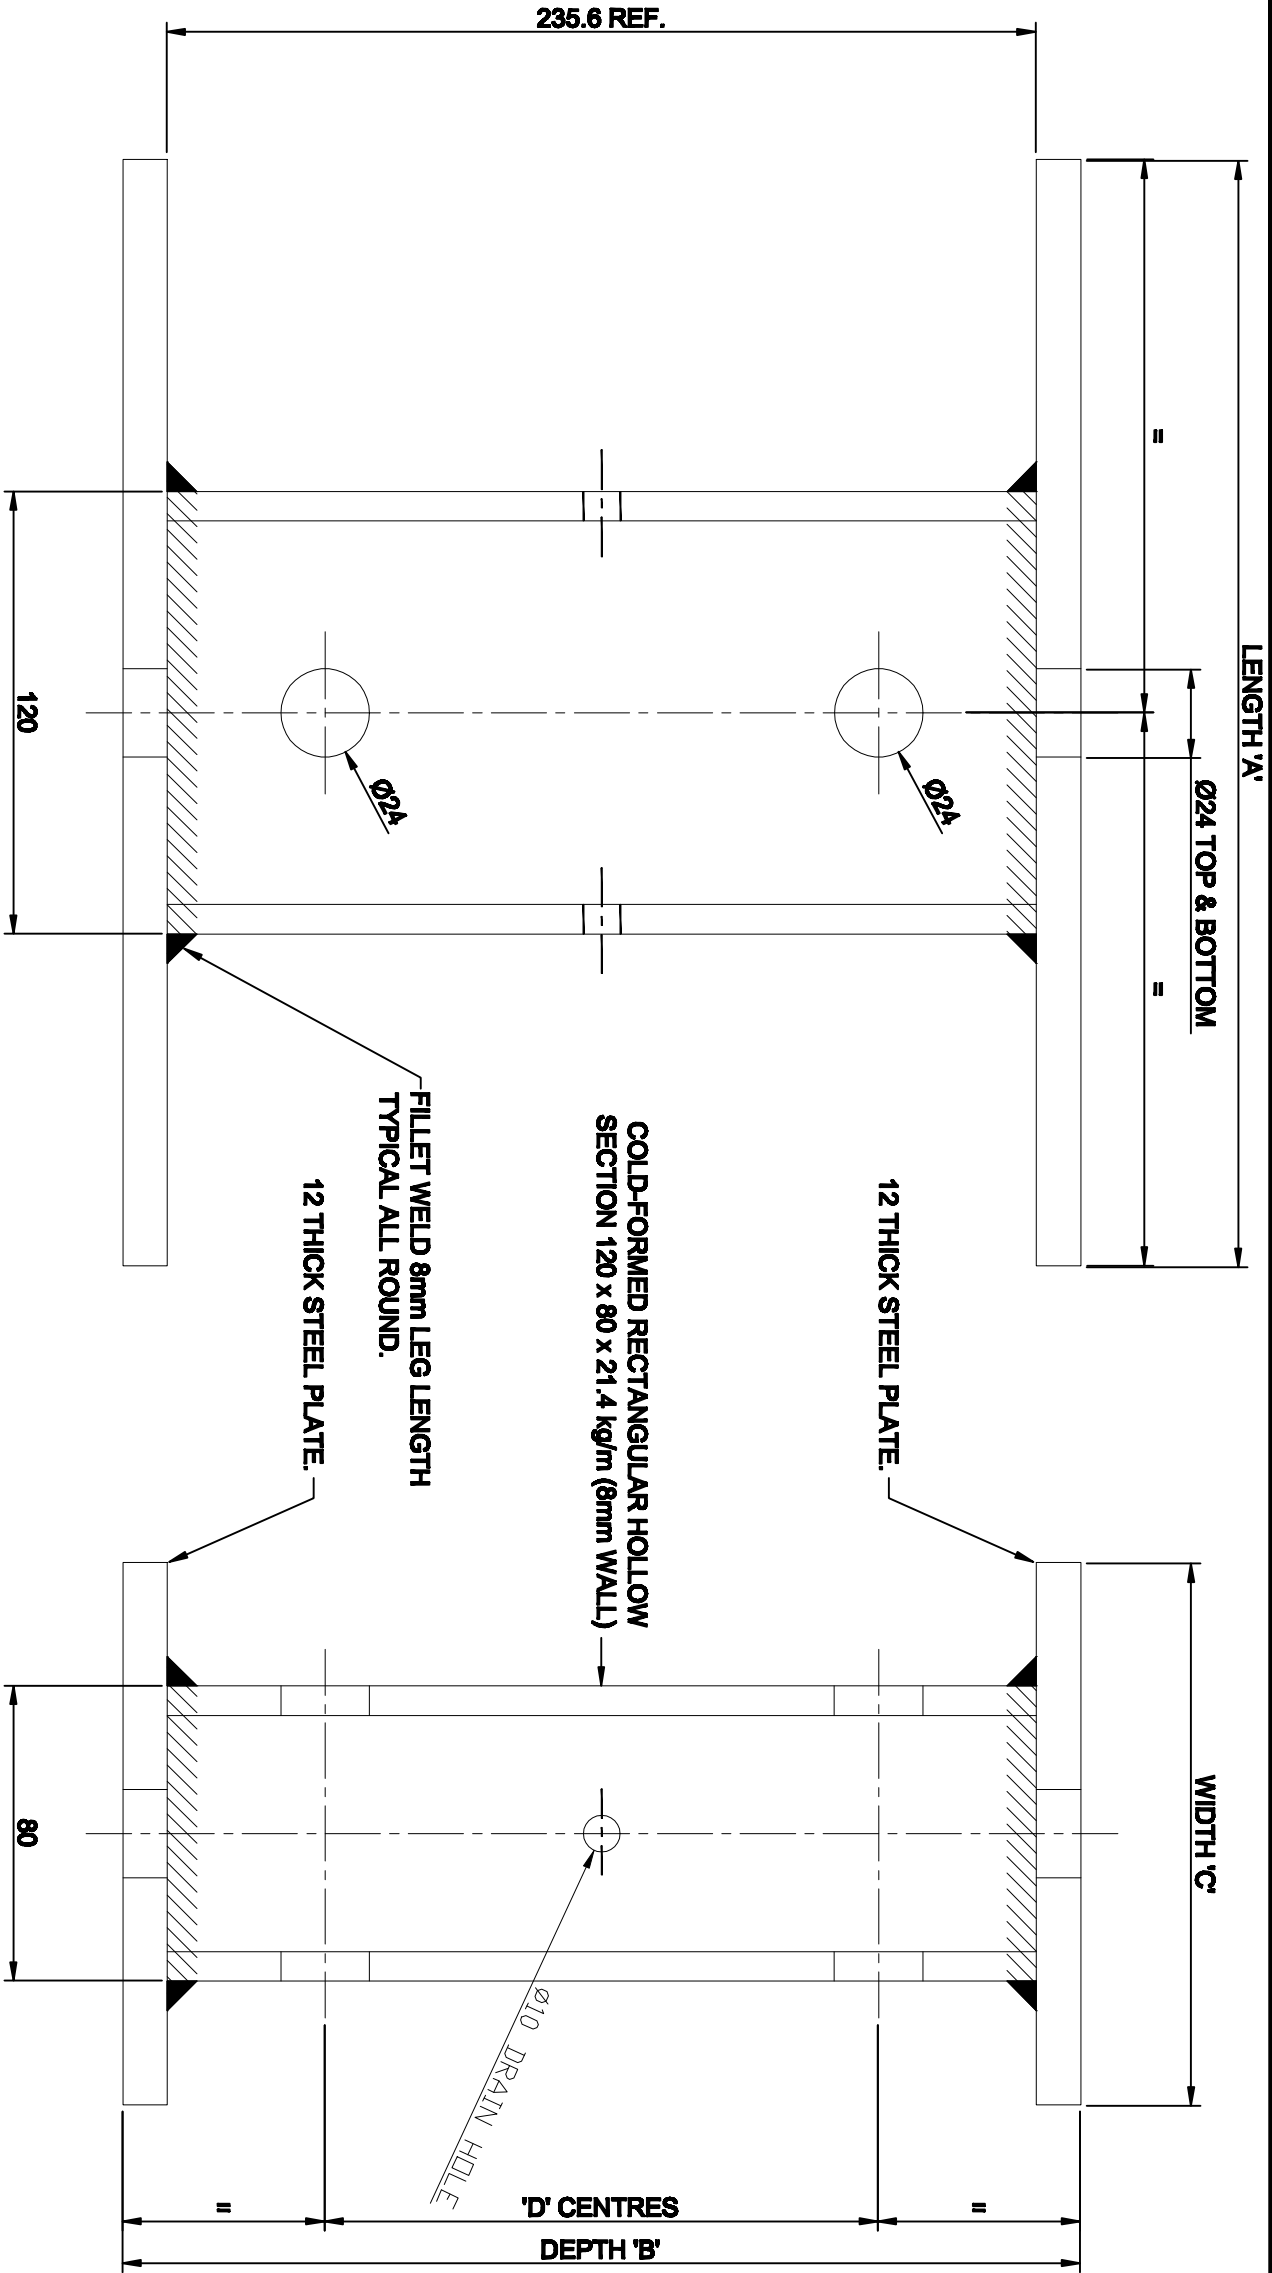

ITEM No.	LENGTH 'A'	DEPTH 'B'	WIDTH 'C'	'D' CENTRES	SHEAR BLOCK LOCATION	
1	270	280	147	150	MEDIUM & STOUT POLE BASE (BURIED)	
2	200	280	147	150	STOUT POLE APEX	
3	170	280	147	150	MEDIUM POLE APEX	
.	.	.	.	.	.	
.	.	.	.	.	.	
.	.	.	.	.	.	

NOTES

- ALL DIMENSIONS ARE IN MILLIMETRES.
- THE Ø24 HOLES AT THE TOP & BOTTOM ARE FOR RELIEF OF GALVANIZING PRESSURE.
- WHOLE SHEAR BLOCK TO BE HOT DIP GALVANIZED AFTER COMPLETION OF ALL DRILLING & WELDING.

CE Electric UK Lloyds Court, 78 Grey Street, Newcastle Upon Tyne, NE1 6AF			132KV OVERHEAD LINES RUTTER TYPE POLE HEAVY DUTY WELDED SHEAR BLOCK SCHEDULE USING RECTANGULAR HOLLOW SECTION		
Manufacturer Details					
Sheet No.	39	Scale	1:2		
Prepared By		Joan Oakley			
		Type OVERHEAD			
Revised	02/08/11	Grid Reference			
Date Issued	13/06/07	Checked By		G HAMMILL	
Revision A		Notes			
Ref No.		C949241		Historic Drg.No.	
				1091010675	