


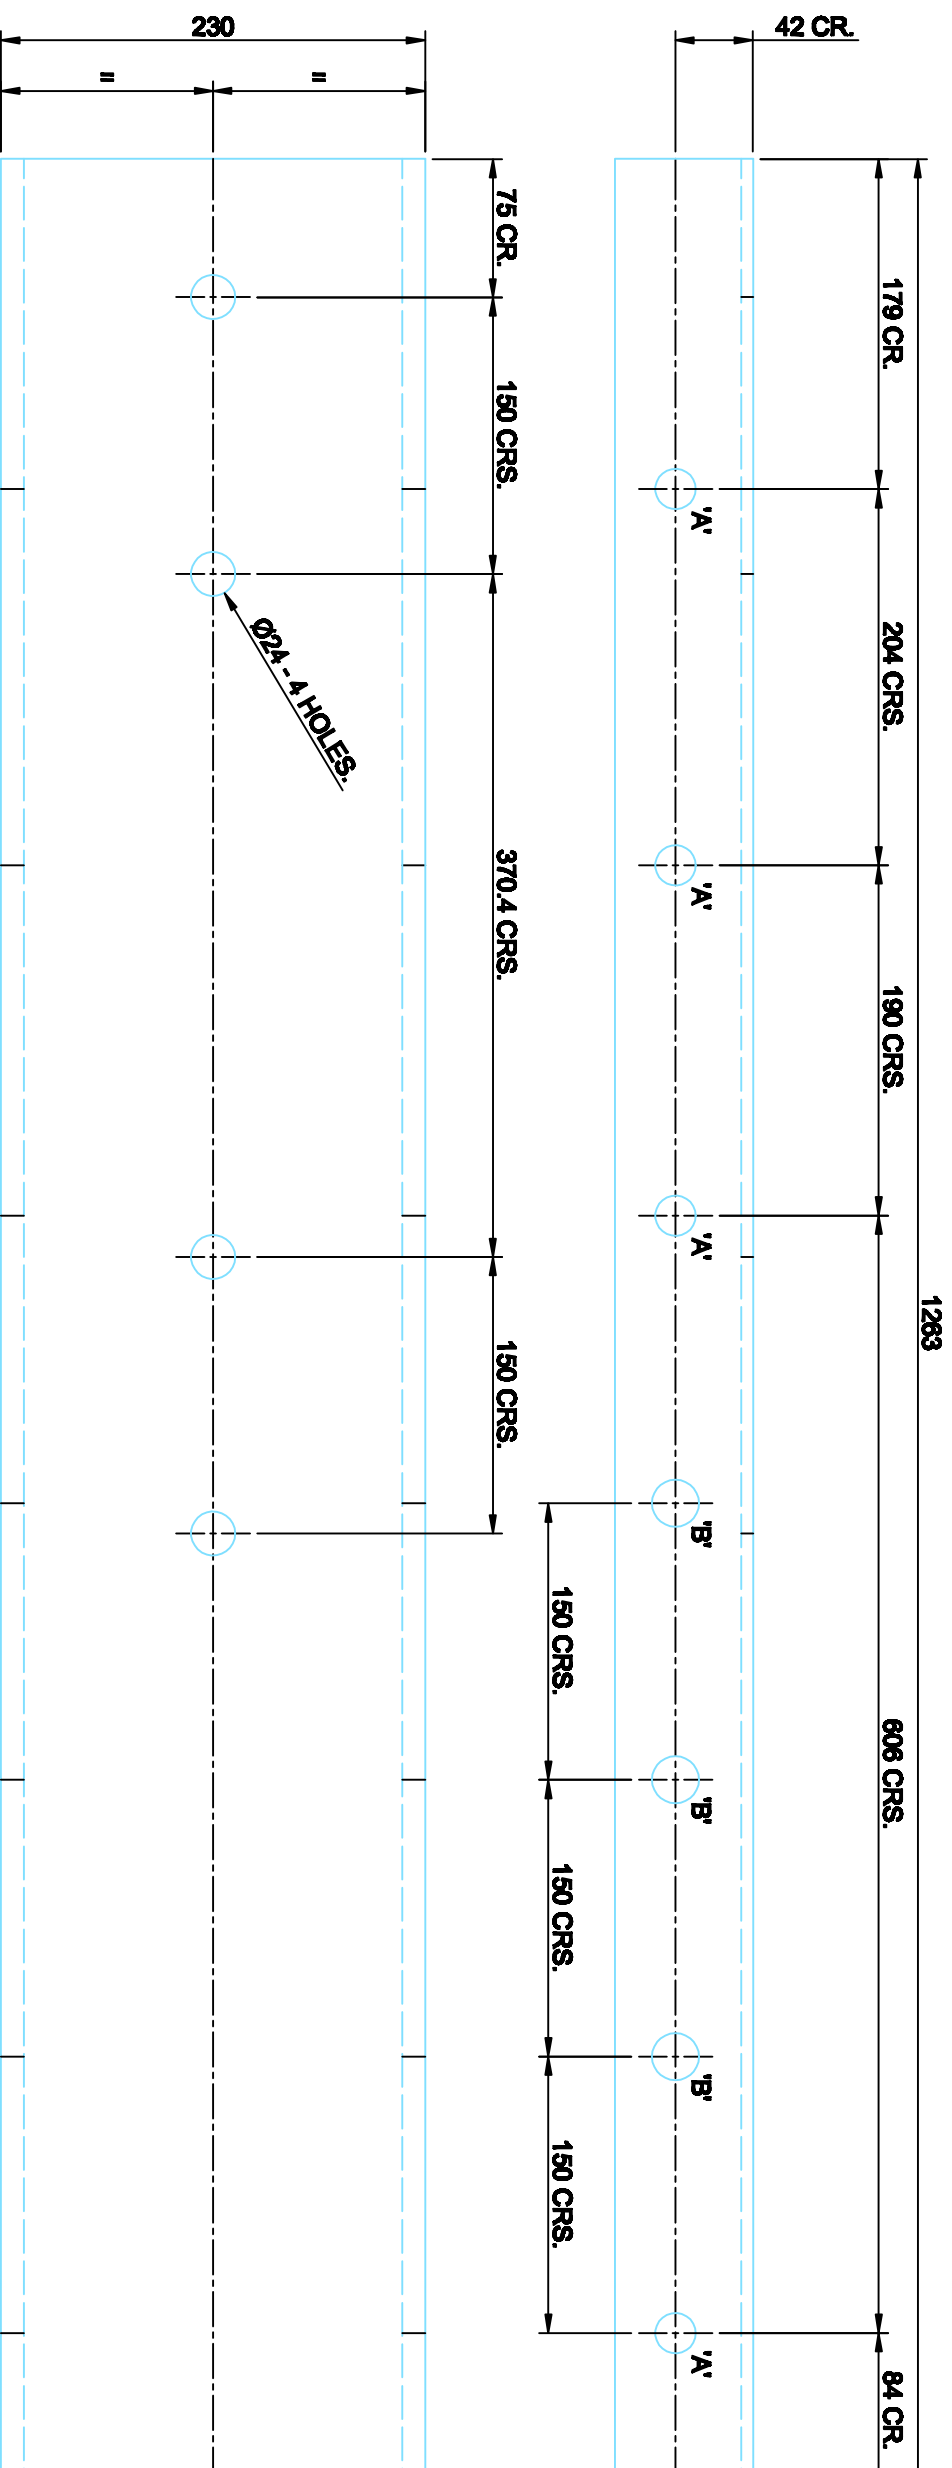

ITEM 10. 1263 LONG x 230 WEB x 75 FLANGE (25.7 kg/m) PARALLEL FLANGE CHANNEL TO B.S. 4 PART 1: 1993.

**HOLES MARKED 'A' ARE Ø22 DRILLED THROUGH BOTH FLANGES.
HOLES MARKED 'B' ARE Ø26 DRILLED THROUGH BOTH FLANGES.**

SCALE 1:4

CE Electric UK		Lloyds Court, 78 Grey Street, Newcastle Upon Tyne, NE1 6AF		
Manufacturer Details				
Sheet No. 10	Scale AS SHOWN			
Prepared By Janis Webb		Type OVERHEAD	132KV OVERHEAD LINE SHORT CROSSARM SUPPORT CHANNEL FOR IN LINE POLES ITEM NO.10	
Reviewed 10/08/07	Grid Reference			
Date Issued 19/08/07	Checked By G HAMMEL			
Revision A Notes				
Ref No. C949337		Historic Drg.No.	DOCUMENT_sub_class 1091010675	